F-439

LANDBRUGSMINISTERIET
JORDBRUGSDIREKTORATET
Sankt Annæ Plads 19, 1250 København K.
Telefon: (01) 15 61 31

SEKRETARIATET FOR
STATENS JORDLOVSUDVALG

J. nr. (anføres i svarskrivelsen)
481-82-2229

Dato (anføres i svarskrivelsen)
- 3 NOV. 1982

Deres skrivelse

Dato

Retten i Middelfart
Algade 6
5500 Middelfart

Hoslagt fremsendes kopi af jordbrugsdirektoratets skrivelse af d. d. til

Advokat Flemming Neidhardt
Ejby St.

INDGÅET
- 4 NOV. 1982
DOMMEREN I MIDDELFART

P.U.V.
e.b.

A. Strømberg

A. Strømberg
fm.

DSS 88303718
40_F_439
Bulk Sort / Hvid
306892

LANDBRUGSMINISTERIET
JORDBRUGSDIREKTORATET
SEKRETARIATET FOR STATENS JORDLOVSUDVALG
Sankt Annæ Plads 19, 1250 København K.
Telefon: (01) 15 61 31

Jr. nr. 481-82-2229
Bedes anført i svarskrivelsen

-3 NOV. 1982

Advokat Flemming Neidhardt
Algade 7
5592 Ejby St.

Ansøger: Villy Henning Hansen
Ansøgningens dato: 13/1o 1982 (j. nr. E 7871)
Den landbrugsejendom, der ønskes erhvervet:
matr.nr. 4h Mosegaard by, Balslev

Ejendommens areal: 1.3156 ha ejendomsværdi: 19o.ooo kr.
heraf grundværdi: 19.3ookr.

Der ansøges om dispensation fra bestemmelserne i landbrugslovens § 16, stk. 1 nr. 5 og 6 om en landmandsuddannelse og jordbrug som væsentligste erhverv.

Som begrundelse er i ansøgningen anført, at Deres klient i længere perioder har arbejdet ved landbruget.

Det er under sagens behandling i juni måned d.å. i statens jordlovsudvalg oplyst, at ejendommen ikke kan anses for en bæredygtig driftsenhed, og det skønnes, at der ikke er behov for arealer fra ejendommen til supplering af andre landbrugsejendomme efter landbrugslovens regler.

vend

A-R-1

Det er ved sagens afgørelse forudsat, at betingelserne i landbrugslovens § 16, stk. 1, iøvrigt er opfyldt, herunder at erhververen inden 6 mdr. efter erhvervelsen tager fast bopæl på ejendommen og selv driver den i sin helhed, samt at erhververen, dennes ægtefælle og børn under 18 år ikke er ejer eller medejer af anden landbrugsejendom.

Under de foreliggende omstændigheder meddeler statens jordlovsudvalg i medfør af § 18 i landbrugsministeriets bekg.nr. 603 af 30. nov. 1978 af lov om landbrugsejendomme tilladelse til, at Villy Henning Hansen erhverver adkomst på landbrugsejendommen matr.nr. 4h Mosegaard by, Balslev.

P.U.V.
e.b.

Såfremt der ved nærværende skrivelse er meddelt tilladelse til erhvervelse af en landbrugsejendom på nærmere angivne betingelser, er eventuelle betingelser ikke til hinder for adkomstdokumentets lysning uden frist, jfr. landbrugslovens § 26, stk. 2.

Der skal, hvis tilladelse er meddelt, ikke i forbindelse med adkomstdokumentets tinglysning afgives erklæring til kommunen, jfr. herved landbrugsministeriets bekendtgørelse nr. 650 af 15. december 1978 om dokumentation ved tinglysning af dokumenter vedrørende landbrugsejendomme.

I henhold til bekendtgørelse nr. 488/1975 om administrationen af visse bestemmelser i lov om landbrugsejendomme kan de i bekendtgørelsens § 1 angivne afgørelser indbringes for landbrugsministeriet. Eventuel klage bør indgives senest 4 uger fra nærværende skrivelses dato.

Matr. nr. 4 h Mosegård By, Balslev

Stempel kr. 3780

Akt: Skab nr. F 439.
(udfyldes af dommerkontoret)

Købers/Kreditors bopæl

Gade og hus nr. Mosegårdvej 15

Anmelder:

ADVOKATERNE
THØGER HJ. JENSEN
ERIK BRODERSEN
MIDDELFART (09) * 41 00 75

Betinget skøde

Underskrevne Helge Christiansen, Bues Gyde 14, Bubbel, 5592 Ejby erkender herved at have solgt - betinget af købesummens berigtigelse og opfyldelse af de i nærværende betingede skøde iøvrigt indeholdte bestemmelser - til medunderskrevne Villy Hansen, Vestermosevej 5, 5580 Nr. Åby den Mosegårdvej 15 beliggende ejendom, som er skyldsat under:

Matr.nr. 4 h, Mosegård by, Balslev, af areal 1 ha. 3.156 m^2 med derpå værende bygninger, disses jord-, mur- og sømfaste dele og øvrige tilbehør, herunder støbegods, centralvarmeanlæg tilsluttet oliefyr med kældertank, fast badeværelsesinventar med spejle og hylder, faste lamper i køkken og badeværelse, udvendige lamper samt alle slags ledninger og installationer, hegn, træer og beplantninger og iøvrigt alt ejendommen rette tilliggende og tilhørende.

Justitsministeriets genpartspapir
Jydsk Papirvare A/S Viby J
1368

I handlen medfølger endvidere 1 gaskomfur med 2 gasflasker, 1 køleskab, 1 vaskemaskine, renovationsstativ og fjernsynsantenne.

De nærmere vilkår er følgende:

1.

Overdragelsen sker med alle de samme, såvel almindelige som særlige rettigheder, byrder og forpligtelser, hvormed ejendommen hidtil har været ejet, hvorved bemærkes, at den er beliggende i landzone, er noteret som landbrug og er behæftet med servitut angående:

a) bygningsafstand fra byvej, lyst 1937 og
b) vejbelysning, lyst 1953.

På tro og love erklæres, at der ikke på ejendommen findes skov eller fredskovpligtig grund. Sælger oplyser at der på ejendommen kan forekomme flyvehavre.

Overdragelsen sker iøvrigt i den stand, hvori ejendommen er og forefindes og af køber er besigtiget, og godkendt uden garanti og ansvar for mangler og fejl ved ejendommens bygninger, hvorved bemærkes, at køber specielt er gjort bekendt med mangler og fejl ved stuehusets gulve og elinstallationer.

Med hensyn til vej- og kloakgæld, udgifter til rensningsanlæg og lignende forpligtelser bemærkes, at der ifølge oplysning fra kommunen ikke påhviler ejendommen sådanne, men køber udreder og tilsvarer, hvad der fremtidig måtte blive pålignet ejendommen af byrder af nævnte art.

Sælger bekendt er der ikke udført arbejder eller afsagt kendelser vedrørende vand, vej, kloak, fortov eller rensningsanlæg og lignende, for hvilke udgifterne senere vil blive pålignet ejendommen.

Overtagelsen finder sted den 1. november 1982. Køber har dog den faktiske dispositionsret over ejendommen fra 10.10.1982 under forudsætning af samtidig betaling af første del af den kontante udbetaling.

Ejendommen henligger fra og med den 10.10.1982 for købers regning og risiko også i ildsvådestilfælde, således at køber til anordningsmæssig anvendelse hæver assurancesummen for bygningerne, der er fuld- og nyværdiforsikrede i henhold til police nr. 296-6276-90700 med Baltica, som kan overtages af køber.

Med overtagelsesdagen som skæringsdag udfærdiges sædvanlig refusionsopgørelse, hvis saldo betales kontant.

Fra og med den 10.10.1982 at regne indtræder køber i alle rettigheder og forpligtelser overfor ejendommens forsyningsselskaber, hvorved bemærkes, at ejendommen er tilsluttet Brende Mølle el-værk og Balslev vandværk.

Parterne sørger selv for aflæsning vedrørende el, vand og eventuel opmåling af olie i tanken. Afregning sker mellem parterne.

Køber respekterer, at jorden er bortforpagtet indtil efter høst 1982 samt at afgrøderne tilfalder forpagteren. Forpagtningsafgiften på kr. 1.200,00, der forfalder til betaling i december termin 1982 tilfalder køberen.

3.

Købesummen er aftalt til kr. 315.000,00, hvilke TRE HUNDREDE FEMTEN TUSINDE KRONER 00 ØRE skal berigtiges på følgende måde:

a) Køber forpligter sig til, at indfri eller overtage til forrentning fra og med overtagelsesdagen at regne, den på ejendommen hvilende gæld til:

1) Kreditforeningen Danmark, kontantlån til 20,7184% p.a. rente, ifølge pantebrev stort opr. ---------- kr. 207.000,00

2, 3 og 4) Private midler til fhv. landmand Kristian Kristensen, Kragsbjergvej 88, st.tv., Odense, ifølge 3 stk. sideordnede pantebreve på hhv. opr. kr. 22.666,66, kr. 22.666,67 og kr. 22.666,67 altså for ialt ---------- kr. 68.000,00

Køber er bekendt med vilkårerne for pantebrevene, der forrentes med 9% p.a. rente. Ved nærværende ejerskifte betales efter særlig aftale med kreditor intet ekstraordinært afdrag, men ved hvert efterfølgende betales 5% af restgældend pr. overtagelsesdagen.

b) Kontant er betalt ---------- kr. 10.000,00

c) og kontant betales senest den 29. oktober 1982 ---------- kr. 30.000,00

Købesum ialt ------- kr. 315.000,00

Når købesummen er berigtiget som foran anført, meddeles der køber endeligt skøde fri for anden gæld eller hæftelse end foran anført.

4.

De med dette skødes udfærdigelse og stempling m.v. forbundne omkostninger udreder køber og sælger i forening, indbyrdes fordelt med halvdelen til hver.

Justitsministeriets genpartpapir

Sælger betaler mæglersalæret til ejendomshandler Laur. Jensen, Ejby.

5.

Af hensyn til ægteskabslovgivningens bestemmelser bemærkes, at ejendommen ikke tjener til bolig eller erhverv for sælgers ægtefælle eller familie.

6.

Advokaterne Thøger Hj. Jensen og/eller Erik Brodersen, Middelfart, bemyndiges til at underskrive endeligt skøde.

---------- ooOoo ----------

I foranstående skødes bestemmelser er underskrevne køber enig og erklærer sig bekendt med, at den kontante ejendomsværdi pr. 1.4.1981 er ansat til kr. 190.000,00, hvoraf grundværdien udgør kr. 19.300,00.

Da køber ikke opfylder betingelserne i henhold til landbrugsloven for erhvervelse af en landbrugsejendom, vil ansøgning om dispensation være at indgive til Statens Jordlovsudvalg, men det bemærkes udtrykkelig, at nærværende handel ikke er betinget af at dispensation opnås.

Ejby, den 26/10-1982
Som køber:
Villy Hansen

Middelfart, den 2/11-1982
Som sælger:
Helge Christiansen

Til vitterlighed om underskrifternes ægthed, dateringens rigtighed og underskrivernes myndighed.

P. Vilhelmsen
kontorass.
Middelfart

J. Jacobsen
kontorasss.
Middelfart

JYPA 220012 Jydsk Papirvare A/S Viby J.

Forannævnte ejendom matr. nr. 4 b Mosgård bg, Balslev
Balslev ejerlav er under løbenr. 04294-1 pr. 1/4 1982
vurderet til kontantejendomsværdi ..... 200000 kr.
heraf kontantgrundværdi ..... 18100 kr.
Ejendommen, der hverken udgør en landejendom eller omfatter nogen del af en sådan, er ikke i matriklen noteret som en del af en samlet ejendom.
Ejby kommunes ejendomsskattekontor, d. 5/11 1982.

Hans Nielsen

Forannævnte ejendom matr. nr. 4 b
Mosgård ejerlav er under løbenr. 04294-1 pr. 1/4 1982
vurderet til kontantejendomsværdi ..... 200000 kr.
heraf kontantgrundværdi ..... 18100 kr.
Ejendommen udgør en landejendom, Matr. nr. 4 b
er i matriklen noteret som landbrug.
Ejby kommunes ejendomsskattekontor, d. 5/11 1982.

Hans Nielsen

E n d e l i g t s k ø d e

Efter at den aftalte købesum nu er berigtiget i overensstemmelse med det betingede skødes bestemmelser så endeligt skødes og overdrages den forannævnte ejendom herved til:

V i l l y H a n s e n, nu Mosegårdvej 15, 5592 Ejby,

hvem ejendommen herefter skal tilhøre fri for anden gæld eller hæftelse end foran reserveret.

Middelfart, den 9. november 1982
For sælgeren i h.t. fuldmagt
foran post 6:

Thøger Jensen

Til vitterlighed om underskrifternes ægthed, dateringens rigtighed og underskrivernes myndighed

J. Jacobsen
kontorass.
Middelfart

H. Åbroe Nielsen
kontorass.
Middelfart

INDFØRT I DAGBOGEN

09.11.82 12048

RETTEN I MIDDELFART

LYST.

Skødet er endelig.

Anm. 1) ejerpantebrev 15.000 kr.
2) -"- 20.000 kr.

QR

Justitsministeriets genpartspapir

F439

Reference: 3421072140

Afgift: DKK 7.500,- ✓

Akt: Skab nr.
(udfyldes af dommerkontoret)
Sælgerpantebrev ☐ (Sæt kryds)

Ejerlav: Mosegård By, Balslev
Matr. nr.: 4 h

Gade og husnr.: Mosegårdvej 15

Anmelder:
~~Danske Bank A/S~~
~~Kredit Service~~
~~Holmens Kanal 2-12~~
~~1092 København K~~
~~Telefon 33 44 00 00~~

Danske Bank
Bolig Service
Omprioritering
Holmens Kanal 2-12
1092 København K
Tlf. 43 39 12 56

Danske Bank A/S hæfter for disse oplysninger		
Pålydende, nyt lån	DKK	620.000,-
- Forholdsmæssigt kurstab, nyt lån	DKK	
- Indfrielsessum, indfriede lån	DKK	213.658,-
- Omkostninger, indfriede lån	DKK	250,-
- Forholdsmæssige omkostninger, nyt lån	DKK	2.775,-
Afgiftspligtigt beløb	DKK	403.416,-
Ved beregningen er anvendt kursværdier		☐
Ved beregningen er anvendt nominelle værdier		☒

3421072132-61 DK

GENPART 137162 01 0000.0041 13.04.2005 TA
7.500,00 K

Pantebrev

Debitors navn og bopæl:
Ella Hansen
Villy Hansen
Mosegårdvej 15
Balslev
5592 Ejby

erkender herved at skylde

Kreditors navn og bopæl:
Danske Bank A/S, Holmens Kanal 2-12, 1092 København K.

Lånets størrelse:
DKK 620.000,00 skriver danske kroner sekshundredetotitusinde 00/100.

Lånetype, rente- og betalingsvilkår

Lånet er et stående lån (afdragsfrit) over 30 år. Lånet skal betales tilbage på én gang 30 år efter lånets udbetaling.

Kreditor kan dog til enhver tid, når pantebrevet har løbet i mindst 10 år, med 3 måneders skriftligt varsel kræve, at debitor begynder at betale pantebrevet tilbage som et annuitetslån med variabel rente og dermed variabel ydelse og over en periode, der vil medføre, at pantebrevet vil være indfriet i sin helhed 30 år efter lånets udbetaling, og i øvrigt på vilkår som fastsat af kreditor.

Pantebrevet skal forrentes fra udbetalingsdagen med en variabel rente, der svarer til renten på indskudsbeviser, som til enhver tid er fastsat af Danmarks Nationalbank. Renten på indskudsbeviser (referencerente), er p.t. på 2,15 procent om året. Her til kommer et rentetillæg på 1,75 procentpoint, der er fastsat af kreditor. Det giver i alt en rente på p.t. 3,90 procent om året.

Rentetillægget er fast, indtil der er gået 10 år fra første termin. Herefter kan kreditor ændre rentetillægget op eller ned i overensstemmelse med kreditors til enhver tid værende ret til at ændre rente jf. kreditors "Almindelige forretningsbetingelser – forbrugere".

NB. Bopælsforandring skal meddeles kreditor
Ved forsinket betaling af renter og afdrag kan kreditor forlange kapitalen indfriet, se side 4/sidste side, pkt. 9a.

W J Christensen A/S. 1-6203-2 (03 00)

Hvis Danmarks Nationalbank ikke længere fastsætter rente på indskudsbeviser, er kreditor berettiget til at vælge en anden tilsvarende referencerente.

I pantebrevets løbetid betales alene renter, medmindre debitor begynder at betale pantebrevet tilbage.

Renten beregnes kvartalsvis bagud og betales hver 31. marts, 30. juni, 30. september og 31. december termin. Første rentebetaling er den 30. juni 2005 termin, hvor debitor betaler rente for perioden 1. april 2005 til 30. juni 2005. Sidste rettidige betalingsdag er de nævnte terminsdatoer.

Opsigelse: Debitor kan indfri pantebrevet helt eller delvis når som helst.

Den pantsatte ejendom: Matr. nr. 4 h Mosegård By, Balslev

Oprykkende panteret efter: Ingen

Respekterede servitutter m.v. (henvisning til tingbogen tilstrækkelig) Med hensyn til de servitutter og andre byrder, der nu påhviler ejendommen henvises til ejendommens blad i tingbogen.

Særlige bestemmelser:

Ejerskifte Pantebrevet forfalder til fuld indfrielse ved ejerskifte, herunder i tilfælde af tvangsauktion. Pantebrevsformular A, pkt. 8 og pkt. 10 er således fraveget i dette pantebrev. Overdragelse eller overgang til medejer, ægtefælle, registreret partner, livsarvinger eller samlever af samme eller af modsat køn, hvormed der i de seneste 2 år har været etableret et ægteskabslignende forhold med fælles folkeregisteradresse, betragtes ikke som ejerskifte.

Løbedage Hvis renten/ydelsen ikke betales rettidigt, forfalder pantebrevet til indfrielse, ligesom der påløber morarenter og gebyrer i overensstemmelse med de regler, kreditor til enhver tid har fastsat herom. Pantebrevsformular A, pkt. 2, bestemmelser om løbedage, gælder ikke for dette pantebrev.

Øvrige lånevilkår For pantebrevet gælder i øvrigt kreditors til enhver tid gældende "Almindelige forretningsbetingelser – forbrugere", i det omfang disse ikke er fraveget ved bestemmelserne i dette pantebrev.

Morarenter Hvis et beløb, som debitor skal betale ifølge dette pantebrev, ikke betales rettidigt, skal debitor betale morarenter af beløbet fra og med forfaldsdagen til den dag betalingen sker. Morarentesatsen for restancer fastsættes til kreditors til enhver tid gældende restancerente for lån.

Kreditoplysninger Debitor har ved underskrift på dette pantebrev modtaget kreditoplysninger i h.t. Kreditaftalelovens § 8a og § 8b.

Udlejningsklausul: Kreditor kan forlange kapitalen indfriet, hvis ejendommen udlejes. Opsigelse kan dog ikke ske, hvis der senest 14 dage efter påkrav stilles bankgaranti for pantebrevets terminsydelser i lejeperioden. Bestemmelsen gælder dog ikke, hvis ejendommen lejes ud til familiemedlemmer i lige linje.

Justitsministeriets genpartspapir

I øvrigt gælder Justitsministeriets pantebrevsformular A (side 4).

Hvis pantebrevet alene underskrives af debitor, erklærer denne samtidig at være ugift/ikke at leve i registreret partnerskab, eller at den pantsatte ejendom ikke er omfattet af §18 i lov om ægteskabets retsvirkninger.

Dato: 6/4-2005

Ella Hansen

Som debitor - Ella Hansen

Villy Hansen

Som debitor - Villy Hansen

Hvis debitor er gift/lever i registreret partnerskab, og den pantsatte ejendom er omfattet af § 18 i lov om ægteskabets retsvirkninger, giver medunderskrevne ægtefælle/registrerede partner samtykke til pantsætningen. (Er ægtefællen/den registrerede partner medejer og skal denne være meddebitor, skal der i stedet underskrives som debitor).

Dato: _____

_____

Som ægtefælle/som debitor og pantsætter

Til vitterlighed om ægte underskrift/underskrifter, dateringens rigtighed og underskriverens/underskrivernes myndighed.

Navn:	Michael Lindskov	Navn:	Ulla Kamp Levinsen
Stilling:	fuldmægtig	Stilling:	rådgiver
Bopæl:	Højvang 77 5270 Odense N.	Bopæl:	Stjernevænget 24 5592 Ejby
Underskrift:		Underskrift:	

W.J. Christensen A/S. 1-6203-2 (03 00)

*** * ***
* * *
* * ***
* * * Retten i Middelfart
* *** *** Tinglysningsafdelingen

Akt.nr.:
F 439

Påtegning på Pantebrev. Dkk 620.000
Vedrørende matr.nr. 4 H, Mosegård By, Balslev
Ejendomsejer: Villy Henning Hansen
Lyst første gang den: 13.04.2005 under nr. 7831
Senest ændret den : 13.04.2005 under nr. 7831

Anm:
Pantebrev Realkredit Danmark, Dkk 256.000

Retten i Middelfart den 18.04.2005

Hanne Hansen, ktfm.

Justitsministeriets genpartpapir
© JYPA 1395 NOV 1996

Matr.nr. 4h Mosegård by, Balslev og
12c Mosegård by, Balslev

Akt.: Skab F nr. 439

Anmelder:

ADVOKATFIRMAET
BISGAARD & DOLBERG A/S
E. Lumby Rasmussen's Efterfølger
Østergade 29
5610 Assens
Tlf. 64 71 16 40
FAX 64 71 16 40

Stempel kr.

Skyl. 50
7 ~~00~~
0/9

12 kV kabelanlæg Dekl.nr. 317

Transformerstation Ny 317 Mosegård Vedrører kun matrikel nr. 12c

Transformerstation 291 Mosegårdvej Vedrører kun matrikel nr. 4h

Deklaration

for elkabler med spændinger til og med 20 kV
samt transformerstation med grundareal på højst 5 m²

Undertegnede meddeler herved med bindende virkning for mig og efterfølgende ejere

An/S Vestfyns Elforsyning

(neden for betegnet "Selskabet")

eller den, til hvem Selskabet eventuelt måtte overdrage sine rettigheder, ret til på omstående ejendom(me) at anbringe ovenstående jordkabelanlæg med fornødent tilbehør.

Anlæggets og dets omtrentlige placering på ejendommen fremgår af den udleverede/vedhæftede plan.

Selskabet har ret til at efterse, vedligeholde og udskifte kabelanlægget med tilhørende transformerstation samt ret til at sikre, at transformerstationen står frit og upåvirket af omgivelserne.

Lodsejeren forpligter sig til at respektere de begrænsninger i brugen af arealet over og omkring kabelanlægget, som lovgivningen til enhver tid foreskriver.

Jorden over kabelanlægget kan altid udnyttes til dyrkning af afgrøder, herunder behandling med normale markredskaber.

Byggeri, etablering af vej, terrænændringer, grubning, dræning, boringer eller andet, hvor der er risiko for at skade kabelanlægget, og som udføres nærmere end 1 m fra kabelanlægget (vandret afstand), skal anmeldes til Selskabet senest 8 dage før påbegyndelsen, hvorefter Selskabet for egen regning påviser eller - om nødvendigt - frilægger kabelanlægget.

For byggeri til landbrugsmæssige formål flytter eller sikrer Selskabet kabelanlægget for egen regning.

Ved skovrejsning eller anden beplantning nærmere end 1 m fra kabelanlægget, skal lodsejeren kontakte Selskabet med henblik på at aftale nærmere vilkår for etablering af beplantningen.

Ved fremtidige dræningsarbejder på ejendommen er Selskabet forpligtet til at afholde merudgifter forårsaget af kabelanlæggets tilstedeværelse, såfremt Selskabet inddrages i den forudgående planlægning.

For de rettigheder Selskabet har erhvervet ved denne deklaration, yder Selskabet en éngangserstatning.

Erstatningen beregnes på grundlag af gældende landsaftale mellem landbrugsorganisationerne og Danske Elværkers Forening.

Erstatning for skader opstået ved anlæggets etablering, vedligeholdelse, udskiftning eller fjernelse opgøres på grundlag af gældende landsaftale mellem landbrugsorganisationerne og Danske Elværkers Forening.

Påtaleberettiget med hensyn til overtrædelse af denne deklarations bestemmelser er Selskabet eller den, til hvem Selskabet måtte overdrage sine rettigheder.

Nærværende deklaration er Selskabet berettiget til at lade tinglyse som servitutstiftende på ejendommen.

Med hensyn til de på ejendommen hvilende servitutter og behæftelser af enhver art henvises til tingbogen.

Deklarationen respekterer omprioritering og prioritering.

Når anlægget ikke bruges længere, og lodsejeren anmoder herom, er Selskabet forpligtet til at aflyse deklarationen og fjerne anlægget.

Dato	Ejendommens matrikelbetegnelse	Ejerens underskrift	Forhandlerens underskrift
	Matr. nr. 4h Mosegård By, Balslev	Villy Hansen	Bo Brink Hansen
30/6-95	Matr. nr. 12c Mosegård By, ~~Balslev~~	I. Kastrup Hansen formalarea placeres i det nordøstlige hjørne på grunden langt med skel det. Arealtum-gen på arealet bliver aplyst til 6-7000kv.	Bo Brink Hansen
		I henhold til § 42 i lov nr. 388 af 6. juni 1991 om planlægning, meddeles herved samtykke til tinglysning af foranstående deklaration. Tilvejebringelse af lokalplan er ikke påkrævet.	
		Ejby Kommune Teknisk Forvaltning, den 7. december 1995 Chr. Bay, afd.ingeniør	
	Matr: 4 H mfl. Mosegård By, Balslev Retten i : Middelfart Indført den : 14.12.1995 Lyst under nr.: 20295 - 96	A	

Nr. 317

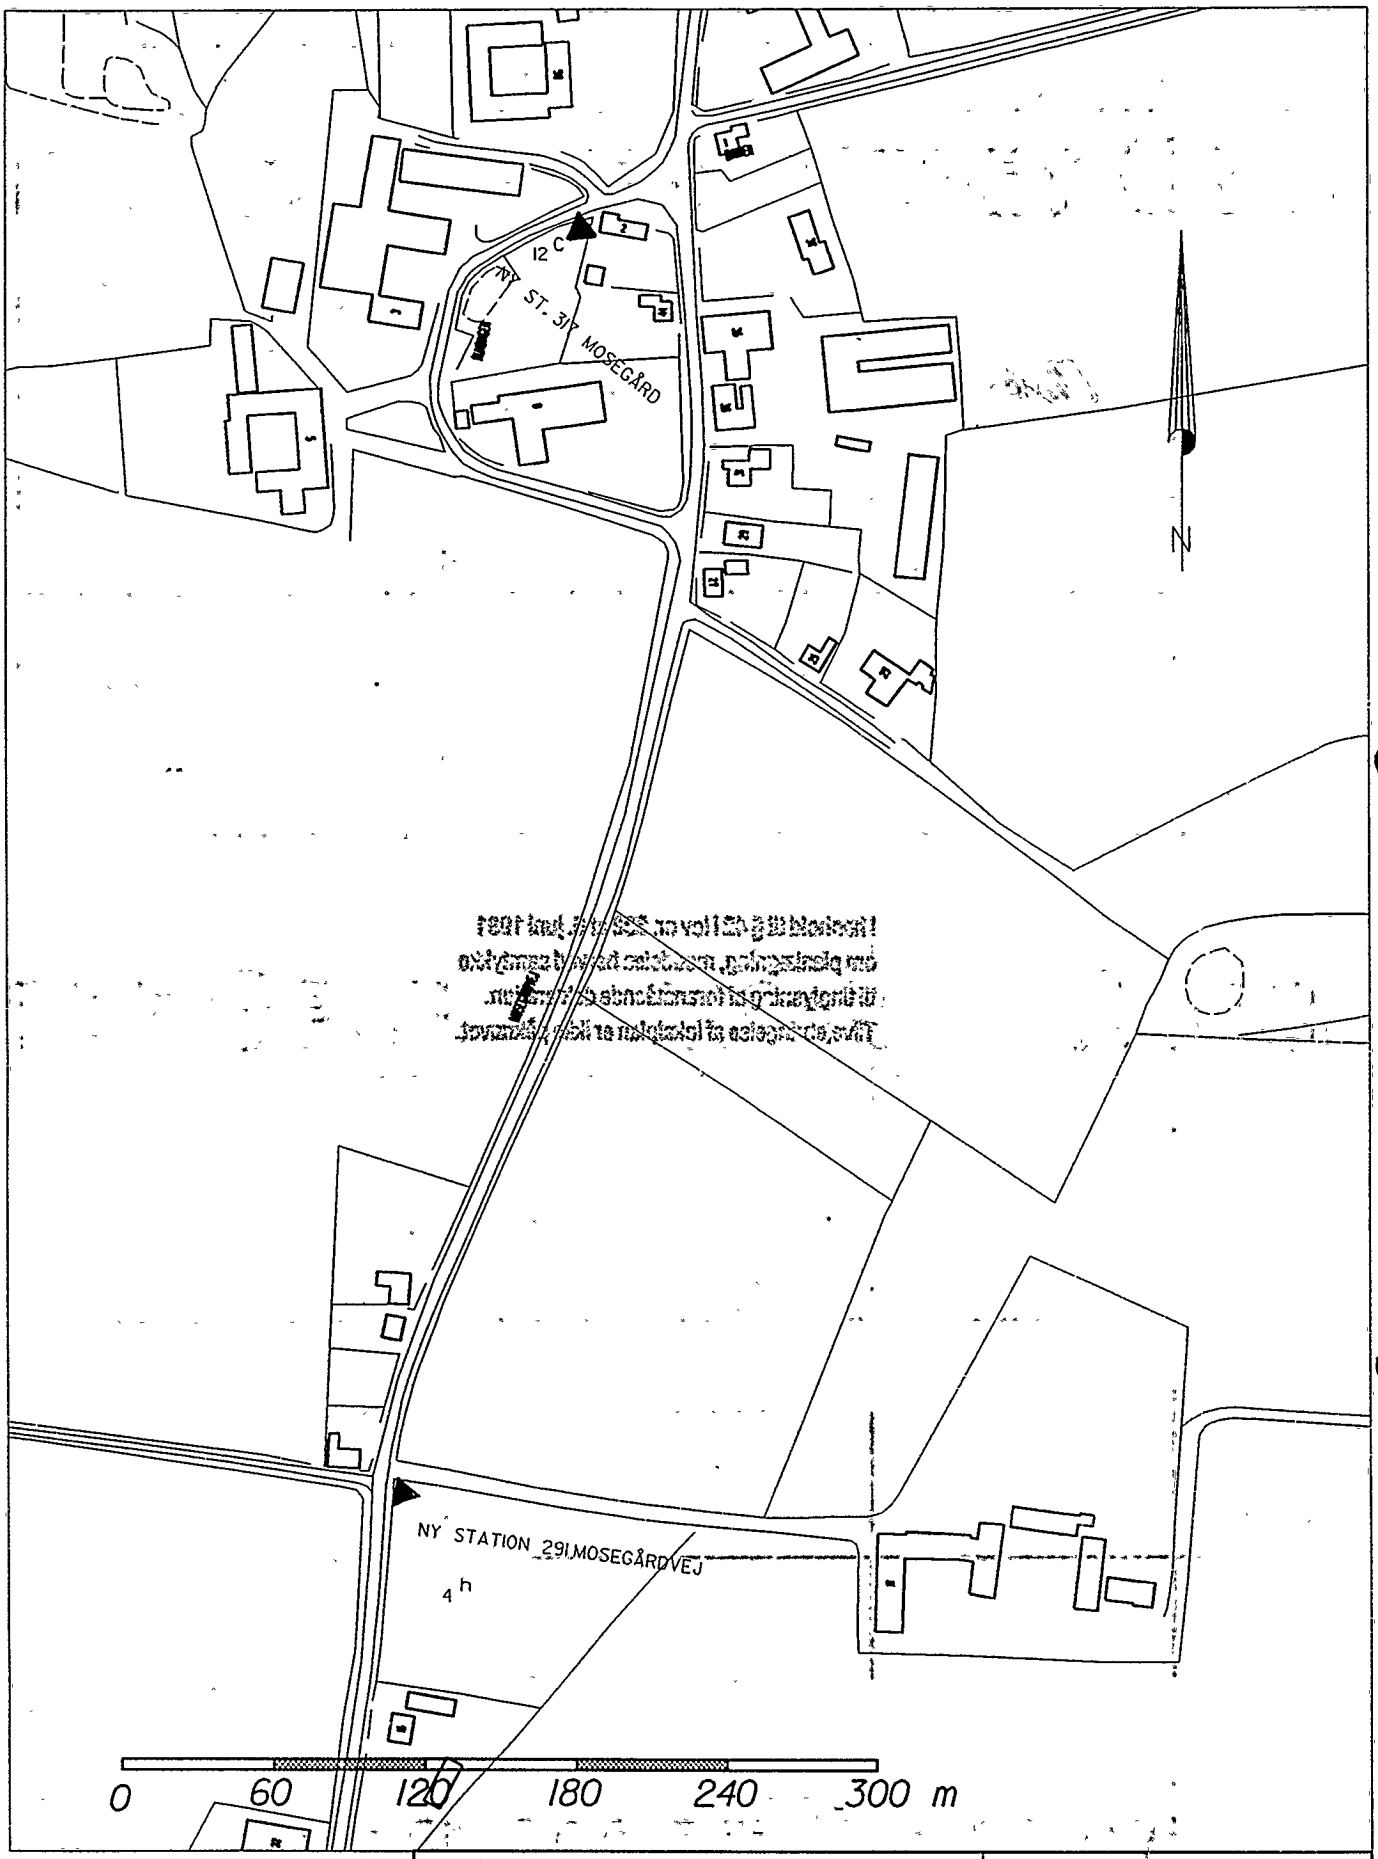

Vestfyns Elforsyning Drejervænget 1 5610 Assens Telefon 64 712177 Telefax 64 714114	Tegnet: Dato /Sign. BBH Revideret: Dato/Sign	
TINGLYSNING AF NY ST. 317 MOSEGÅRD OG NY ST. 291 MOSEGÅRDVEJ	Målestok 1:3000	Fremstillet 28. nov. 1995
	Tegn.nr. P-1209	

Akt: Skab F Nr. 439

Henvisningsblad.

Mtr. Nr., Ejerlav, Sogn: (i København Kvarter) eller (i de sønderjydske Landsdele) **Bd. og Bl. i Tingbogen, Art. Nr., Ejerlav, Sogn.**

1/4 Kr Asaregaard, Balslev Sogn

8/1 1937 Lgat Decl. se Skab D. 193.

Bestillings-Formular L

Jensen & Kjeldskov, A/S, København

Justitsministeriets genpartpapir

*** * ***
* * *
* * ***
* * * Retten i Middelfart
* *** *** Tinglysningsafdelingen

Akt.nr.: 40_F_439

Påtegning på Skifteretsattest.
Vedrørende matr.nr. 4 H, Mosegård By, Balslev
Ejendomsejer: Ella Jensine Hansen
Lyst første gang den: 24.02.2009 under nr. 1968
Senest ændret den : 24.02.2009 under nr. 1968

Lyst som endelig adkomst.

Retten i Middelfart den 26.02.2009

Rikke Thybo Nielsen

© JYPA 1395 NOV 1996

11-Mar-200918139

Justitsministeriets genpartpapir

RETTEN I ODENSE

Akt:
(Udfyldes af tinglysningskontoret)

RETTEN I ODENSE
skab nr.
DANMARKS DOMSTOLE

Sagsnr. SKS 15-2550/2008

10. november 2008

Skifteretsattest om uskiftet bo

Det attesteres, at boet efter

Navn Villy Henning Hansen	
Adresse Mosegårdvej 15, 5592 Ejby	
Født den 27. januar 1933	Død den 1. oktober 2008

den 10. november 2008 er udleveret ægtefællen

Navn Ella Jensine Hansen
Adresse Mosegårdvej 15, 5592 Ejby
Født den 28. september 1933

til uskiftet bo.

Underskrift

Benthe Witus Nielsen
kontorfuldmægtig

RETTEN I ODENSE
DANMARKS DOMSTOLE

11-Mar-200918140

STD074717-S24-ST01-K240.01-T1-L08-M14-P01-K9

© JYPA 1376 FEB 1995

Matr.nr. 4 h
Ejerlav: Mosegård by, Balslev
Beliggende: Mosegårdvej 15, 5592 Ejby

Anmelder:

home
SERVICECENTER
SYDDANMARK A/S
Odensevej 33, 1. sal · 5500 Middelfart
Tlf. 44 74 84 84 · Fax 44 74 84 99

Nærværende skifteretsattest begæres tinglyst som adkomst for Ella Jensine Hansen, Mosegårdvej 15, 5592 Ejby på ejendommen matr.nr. 4 h, Mosegård by, Balslev beliggende Mosegårdvej 15, 5592 Ejby, i forbindelse med videresalg til tredjemand.

Med hensyn til byrder og servitutter henvises til ejendommens blad i tingbogen.

Middelfart, den 23/1 - 2009

For vedkommende:

home
SERVICECENTER
SYDDANMARK A/S
Odensevej 33, 1. sal · 5500 Middelfart
Tlf. 44 74 84 84 · Fax 44 74 84 99

Justitsministeriets genpartpapir


```
*** *   ***
 *  *   *
 *  *   ***
 *  *     *  Retten i Middelfart
 *  *** ***  Tinglysningsafdelingen
```

Akt.nr.: 40_F_439

Påtegning på Skøde.
Vedrørende matr.nr. 4 H, Mosegård By, Balslev
Ejendomsejer: Bjarne Jørgensen
Lyst første gang den: 24.02.2009 under nr. 1969
Senest ændret den : 24.02.2009 under nr. 1969
Storkunde opkrævning - Dkk 8.300

Skødet er endeligt.
*
Anm: Dkk. 620.000, Pantebrev Danske Bank-Kbh.

Retten i Middelfart den 26.02.2009

Rikke Thybo Nielsen

© JYPA 1395 NOV 1996

11-Mar-200918141

Justitsministeriets genpartpapir

Akt: skab nr.
(Udfyldes af tinglysningskontoret)

Afgift kr. 8.300,00

Ejerlav: Mosegård by, Balslev

Matr. nr.: 4 h

Beliggende: Mosegårdvej 15
5592 Ejby

Købers bopæl: 5592 Ejby

SE: 86 06 44 13 - STORKUNDE

Anmelder:
MIDDELFART ADVOKATERNE
Jensen-Dahm, Gorm Pedersen &
Schroll Madsen
Tinghuset, Algade 6, 5500 Middelfart
Tlf.: 64 41 00 52
J.nr.: 6886-1/DC

Købesummen ønskes

ikke offentliggjort.

ENDELIGT SKØDE

---o0o---

Undertegnede **Ella Jensine Hansen, Mosegårdvej 15, 5592 Ejby,** sælger, skøder og endeligt overdrager herved til medundertegnede:

Bjarne Jørgensen
Mosegaardvej 30
5592 Ejby

den sælger ifølge tinglyst adkomst tilhørende ejendom matr. nr. 4 h Mosegård by, Balslev, af areal ifølge tingbogen 4.449 m^2, heraf vej 798 m^2, beliggende Mosegårdvej 15, 5592 Ejby. For overdragelsen er aftalt følgende nærmere

VILKÅR:

1.

Under det solgte, der er et enfamilieshus, er indbefattet på grunden værende bygninger med disses grund-, mur- og nagelfaste genstande, alle slags installationer, herunder varmeanlæg med oliefyr (ny overfladetank opsættes af sælger) og brændeovn, faste lamper og fast badeværelses-

11-Mar-200918142

© JYPA 1376 FEB 1995

udstyr, hegn, træer og plantninger og i det hele alt ejendommens rette tilliggende og tilhørende i enhver henseende.

I overdragelsen medfølger endvidere køleskab, keramisk komfur (Siemens), indbyningsovn (Siemens) og emhætte (Ecoline). Alle hvidevarer er fra 2006.

Medfølgende hårde hvidevarer og løsøre afleveres i gældfri og brugbar stand.

Det solgte overtages, således som det er og forefindes, og som det er køber bekendt, og med de samme almindelige og særlige rettigheder, byrder og forpligtelser, hvormed det har tilhørt sælger og tidligere ejere.

Ifølge tingbogsoplysning hviler der følgende servitutter på den solgte ejendom:

1937	Dokument om byggelinier m.v.
1995	Dokument om forsynings-/afløbsledninger m.v.

Der henvises i øvrigt til ejendommens blad i tingbogen.

2.

Ejendommen overtages den 01.04.09, fra hvilket tidspunkt det solgte henligger for købers regning og risiko.

Køber overtager risikoen for ejendommen på overtagelsesdagen eller på dispositionsdagen, hvis denne er tidligere end overtagelsesdagen. Hvis ejendommens bygninger er fuld- og nyværdiforsikrede mod brandskade, overgår risikoen herfor dog allerede til køber ved købsaftalens underskrift. Køber er da berettiget til erstatningen fra brandforsikringen efter de herom gældende regler og er forpligtet til at opfylde den indgåede handel. Sælger vedligeholder ejendommen forsvarligt i enhver henseende indtil dispositionsdagen.

Justitsministeriets genpartpapir

Det er aftalt mellem sælger og køber, at overdragelse af ejendommen kan ske før overtagelsesdagen, såfremt sælger ønsker det.

Køber er i så tilfælde forpligtet til at overtage ansvaret samt afholde udgifter til forbrugsafgifterne fra dispositionsdagen, når betingelserne i afsnit 16, punkt 2 samt afsnit 11 i købsaftalen er opfyldt.

Ejendommen er af sælger brandforsikret i Topdanmark under policenr. L 8869174077. Køber tegner selv ny forsikring til ikrafttræden den 1. april 2009.

Sælger afleverer ejendommen i ryddeliggjort stand senest på overtagelsesdagen kl. 12.00.

Med overtagelsesdagen som skæringsdag udfærdiges sædvanlig refusionsopgørelse senest 30 dage efter overtagelsesdagen. Saldo i sælgers favør forfalder 8 dage efter, at refusionsopgørelsen foreligger uden indsigelser fra parterne. Saldo i købers favør forfalder, når refusionsopgørelsen foreligger uden indsigelse fra parterne, dog tidligst ved købesummens frigivelse.

Køber kan ikke uden sælgers samtykke foretage modregning i refusionssaldoen for eventuelle mangelskrav.

3.

Sælger oplyser,

at der sælger bekendt ikke er sager eller består uopfyldte krav fra det offentlige eller private vedrørende ejendommen,

at sælger ikke har begæret ejendommen omvurderet eller indgivet klage over den fastsatte vurdering,

at der sælger bekendt ikke indenfor de seneste 10 år, dog højst i sælgers ejertid, har været konstateret eller afhjulpet skader på grund af svampe- og insektangreb, medmindre andet er oplyst i tilstandsrapporten,

at der sælger bekendt ikke påhviler ejendommen utinglyste rettigheder eller forpligtelser,

11-Mar-200918143

© JYPA 1376 FEB 1995

at al forfalden gæld vedrørende anlægsarbejder og tilslutninger til vej, fortov, fællesanlæg, fællesantenne, el, gas, vand, kloak, rensnings- og ledningsanlæg vil være betalt i forbindelse med handelens afslutning. Sælger bekendt er der ikke udført arbejder, afsagt kendelser eller truffet beslutninger af offentlige myndigheder, for hvilke udgifterne senere vil blive pålagt ejendommen,

at olietanken sælger bekendt er lovlig.

Køber er gjort udtrykkelig opmærksom på, at ejendommens olietank ikke opfylder bestemmelserne i olietanksbekendtgørelsen nr. 633 af 27. juni 2005 samt efterfølgende ændringer i bekendtgørelse nr. 818 af 22. juni 2005, idet olietanken er for gammel. Sælger sørger for opsætning/tilslutning m.v. af ny olietank og afholder alle omkostningerne hertil, ligesom sælger sørger for og afholder alle omkostninger i forbindelse med bortskafning af den gamle olietank.

Køber er bekendt med, at bygningsarealerne er fremkommet på baggrund af ejendommens BBR-ejermeddelelse. Er ejendommens arealstørrelser af afgørende betydning for køber, opfordres køber til at foretage opmåling af bygningerne forud for underskrift af dokumenterne.

Nærværende aftale er omfattet af Lov om forbrugerbeskyttelse ved erhvervelse af fast ejendom m.v.

Nærværende ejendom er omfattet af lov 2005-06-24 nr.585 om fremme af energi- og vandbesparelser i bygninger, og ifølge denne lov påhviler det sælger til køber at fremlægge energimærke og energiplan for ejendommen, dog er det aftalt, at køber accepterer indholdet heraf.

Køber har i henhold til lov nr. 391 af 14. juni 1995 om forbrugerbeskyttelse ved erhvervelse af fast ejendom m.v. forud for handlens indgåelse modtaget kopi af tilstandsrapport HE nr. 1890, Lb.nr. H-08-01890-0192, udarbejdet den 9/9 2008 af OBH Ingeniørservice A/S samt tilbud på ejerskifteforsikring, udarbejdet af Forsikringsselskabet Topdanmark den 9/9 2008.

Køber har fra sælger i et særskilt bilag modtaget sælgers uigenkaldelige løfte om at betale halvdelen af den præmie, der fremgår af en almindelig ejerskifteforsikring, der som minimum er tegnet for en 5-årig periode og med en selvrisiko på max. kr. 34.000,00.

Justitsministeriets gennemtrykspapir

Ejerskifteforsikring kan efter købers frie valg tegnes enten i det forsikringsselskab, hvorfra tilbud stammer eller i et andet forsikringsselskab. Uanset hvilket selskab køber vælger, skal forsikringen tegnes inden den frist, der fremgår af forsikringstilbuddet, og i alle tilfælde inden køber disponerer over ejendommen. Det er købers ansvar at påse, at der rettidigt er sket tegning af forsikringen.

Det er endvidere mellem parterne aftalt, at køber ikke skal kunne påberåbe sig forhold, som er opstået efter udarbejdelsen eller fornyelsen af tilstandsrapporten i det omfang disse ville være dækket af den tilbudte ejerskifteforsikring. Dette gælder dog ikke forhold, som omfattes af nødvendig vedligeholdelse, idet sælger vedligeholder ejendommen frem til overtagelsesdagen.

4.

Skat oplyser, at ejendomsværdien pr. 1/10 2007 efter kontantværdi udgør kr. 880.000,00, heraf grundværdi kr. 134.500,00.

Parterne erklærer sig bekendt med kommuneoplysning afgivet af Middelfart kommune den 18/9 2008.

Sælger indestår for, at ejendommen ikke er pålignet gæld ud over, hvad der fremgår af kommuneoplysningen.

Alle fremtidige bidrag er sælger uvedkommende.

Køber indtræder i sælgers rettigheder og forpligtelser overfor de lokale forsyningsselskaber.

Sælger meddeler ejerskifte til de respektive værker med henblik på aflæsning af forbrugsmålere og fremsendelse af slutopgørelse. Sælger afmelder evt. PBS.

11-Mar-200918144

© JYPA 1376 FEB 1995

5.

Købesummen er aftalt til kr. 1.145.000,00, skriver kroner enmillionethundredefiretifemtusinde 00 øre, der skadesløst for sælger berigtiges på følgende måde:

A. Kontant udbetaling:		
Køber har deponeret hos Home	kr.	60.000,00
B. For restkøbesummen stiller køber bankgaranti, der på overtagelsesdagen den 01.04.09 afløses af en kontant deponering i sælgers pengeinstitut Danske Bank, Algade 4, 5592 Ejby. Beløbet deponeres på en særskilt konto indtil der foreligger endeligt tinglyst anmærkningsfrit skøde til køber.	kr.	1.085.000,00
Købesum i alt	**kr.**	1.145.000,00

I forbindelse med købers eventuelle optagelse af ejerskiftelån er køber berettiget til at foretage stempeloverførsel fra de realkreditlån, som sælger indfrier i forbindelse med handlen.

6.

Køber er ansvarlig for, at ejendomsskat m.v., som forfalder efter overtagelsesdagen, betales rettidigt, og dette gælder uanset, om opkrævningskortene måtte lyde på købers eller sælgers navn.

Opmærksomheden henledes på, at dette også er tilfældet, selv om køber ikke har modtaget betalingskort.

Justitsministeriets gæppartpapir

Akt: skab nr.
(Udfyldes af tinglysningskontoret)

Omkostningerne ved nærværende skødes registrering betales af parterne i det indbyrdes forhold fordelt med halvdelen til hver.

Sælger alene betaler omkostningerne ved fjernelse af pantehæftelser, der ikke skal overtages af køber og mæglersalær.

Hver part betaler egen advokat.

Middelfart, den

Ejby, den 07-12-2008

Som sælger:

Som køber:

Ella Jensine Hansen

Bjarne Jørgensen

Til vitterlighed om underskriftens ægthed, dateringens rigtighed og underskrivers myndighed for så vidt angår sælger:

Navn: Else Marie NISSEN
Else Marie Nissen

Stilling: PENSIONIST
Pensionist

Bopæl: KVÆDEVÆNGET 14
Kvædevænget 14
MIDDELFART
5500 Middelfart

Navn: Hanne E. Knudsen
Hanne E. Knudsen

Stilling: FODPLEJER
Fodplejer

Bopæl: Islandsvej 4
Islandsvej 4
5500 Middelfart
5500 Middelfart

11-Mar-200918145

© JYPA 1376 FEB 1995

Forannævnte ejendom matr.nr. 4-h Mosegård by,
Balslev er under løbenr. 410-003729 pr. 01.10.2007

vurderet til ejendomsværdi 880.000 kr.
heraf grundværdi 134.500 kr.

Ejendommen der hverken udgør en landbrugsejendom eller omfatter nogen del af en sådan, er ikke i matriklen noteret som en del af en samlet ejendom.

MIDDELFART KOMMUNE
Plan & Byg, den 4. februar 2009

Anette Nørbo
Anette Nørbo

*** * ***
* * *
* * ***
* * * Retten i Middelfart
* *** *** Tinglysningsafdelingen

Akt.nr.: 40_F_439

Påtegning på Pantebrev med rentetilpasning. Dkk 916.000
Vedrørende matr.nr. 4 H, Mosegård By, Balslev
Ejendomsejer: Bjarne Jørgensen
Lyst første gang den: 28.04.2009 under nr. 4438
Senest ændret den : 28.04.2009 under nr. 4438

Anm:
Pantebrev Danske Bank-Bolig Service/Kbh, Dkk 620.000

Retten i Middelfart den 06.05.2009

Helle H. Sørensen

Justitsministeriets genpartpapir
© JYPA 1395 NOV 1996
12-May-200922149

1511698 02

Akt: skab nr.
(udfyldes af tinglysningskontoret)

Afgift: kr. 4.400,-

Ejerlav
Mosegård By, Balslev

Matr.nr.
4 h

Gade og husnr.
Mosegårdvej 15
5592 Ejby

Anmelder
Middelfart Sparekasse

Algade 69
5500 Middelfart
Tlf.nr. 64222222 / LHP

Pålydende nyt lån	kr.	916.000
- Restgæld, indfriede lån	kr.	620.000
- Omkostninger, indfriede lån	kr.	750
- Forholdsmæssige omkostninger, nyt lån	kr.	3.400
Afgiftspligtigt beløb	kr.	291.850

Ved beregningen er anvendt nominel værdi.

Pantebrev
Kontantlån med rentetilpasning
Hel eller delvis afdragsfrihed
Lånet er inkonverterbart

Debitors navn og bopæl
Bjarne Jørgensen
Mosegårdvej 30
Mosegård
5592 Ejby

GENPART 061425 02 0000.0025 28.04.2009 TA
4.400,00 K

Kreditor
Totalkredit A/S, Helgeshøj Allé 53, 2630 Tåstrup, CVR-nr. 21 83 22 78

Lånets størrelse	**Årlig rente**	**Serie**	**Løbetid**
kr. 916.000	3,0142	12 Eod	30 år

Rente- og betalingsvilkår
Renten er foreløbig ansat. Renten fastsættes ved lånets udbetaling. Renten ændres ved rentetilpasning, der sker ved refinansiering af lånets obligationsrestgæld.

Fra termin nr. 1	til termin nr. 36	er lånet afdragsfrit.
Fra termin nr. 37	til udløb	tilbagebetales lånet som annuitetslån.

Ved tilbagebetaling som annuitetslån henvises dog til afsnittet om Betalinger på lånet i pantebrevets særlige bestemmelser. Hele lånets restgæld refinansieres hvert år med virkning fra en 1. oktober. Refinansieringshyppigheden kan ændres efter aftale mellem debitor og Totalkredit. Totalkredit kan beslutte, at refinansieringstidspunktet ændres, jf. afsnittet om Refinansiering i pantebrevets særlige bestemmelser. Bidrag 0,1250% kvartårligt beregnet af lånets restgæld.

Dette pantebrev kan ikke overdrages til eje eller pant eller gøres til genstand for individuel retsforfølgning.

NB! Bopælsforandring skal meddeles til kreditor. Ved forsinket betaling af renter eller afdrag kan kreditor forlange kapitalen indfriet, se sidste side, pkt. 9a.

Justitsministeriets genpartpapir.
2414002 2009-04-01-15.04.29 PR 1511698 02
12-May-200922150
267 G Reihdar Hansen ApS . Tlf. 63 11 00 12

Forfaldstidspunkter
Terminsydelserne på lånet forfalder hver den

11. marts	for terminsperioden	1. januar - 31. marts
11. juni	for terminsperioden	1. april - 30. juni
11. september	for terminsperioden	1. juli - 30. september
11. december	for terminsperioden	1. oktober - 31. december

Ved ændring af refinansieringstidspunktet kan forfaldstidspunkterne ændres.

Opsigelse
Der henvises til afsnittene "Særlige bestemmelser" og Justitsministeriets pantebrevsformular B.

Den pantsatte ejendom

Matr.nr.	**Areal m²**	**heraf vej m²**
4 h Mosegård By, Balslev	4.449	798

Oprykkende panteret efter

Ingen.

Respekterede servitutter m.v. (henvisning til tingbogen er tilstrækkelig)
De før den 1. januar 2009 tinglyste med undtagelse af sådanne, der efter deres indhold respekterer dette pantebrev.

Særlige bestemmelser

Vilkår for lånet
For lånet gælder de af Totalkredits bestyrelse til enhver tid fastsatte vilkår for långivningen og obligationsudstedelsen. Henvisningen til vedtægterne i Justitsministeriets pantebrevsformular B skal forstås som en henvisning til bestemmelser fastsat af Totalkredits bestyrelse med hjemmel i Totalkredits vedtægter.

Der henvises i øvrigt til de til debitor udleverede "Almindelige forretningsbestemmelser" i Långuiden samt "Særlige bestemmelser" i nærværende pantebrev. Såfremt ejendommen har flere ejere, skal samtlige tiltræde pantebrevet som solidarisk hæftende debitorer.

Lånet udløber den 30. september i det år, der ligger 29 år efter lånets udbetaling. Udbetales lånet i perioden 1. september til 30. september, udløber lånet dog den 30. september i det år, der ligger 30 år efter lånets udbetaling. En eventuel restgæld ved lånets udløb forfalder til betaling den 11. september i udløbsåret. Totalkredit kan beslutte, at refinansieringstidspunktet ændres, jf. afsnittet om Refinansiering i pantebrevets særlige bestemmelser.

Lånets obligationer er emitteret i Nykredit Realkredit (Totalkredit).

Dette lån er ydet i Totalkredits kapitalcenter F. Lånet og pantebrevet overføres uden yderligere vedtagelse til Totalkredits kapitalcenter E, når den garanti, der er stillet for tinglysning af dette pantebrev, frigives af Totalkredit. Overførslen af lån og pantebrev sker dog under alle omstændigheder senest 6 måneder efter lånetilbudets udstedelse. Vilkårene for lånet forbliver uændret gældende ved overførslen til Totalkredits kapitalcenter E.

Lånet er ydet uden supplerende lovbestemt sikkerhed, medmindre andet er anført.

Pantebrevet kan ligge til sikkerhed for lån finansieret ved udstedelse af særligt dækkede obligationer eller særligt dækkede realkreditobligationer.

Lånet kan derfor blive udbetalt i en anden serie end anført på pantebrevets forside.

Debitors hæftelse
Debitor hæfter over for Totalkredit såvel med det pantsatte som personligt for lånet.

2414002 2009-04-01-15.04.29 PR 1511698 02

Justitsministeriets genpartpapir.

Betalinger på lånet
Lånet tilbagebetales som et annuitetslån.

Forudsat Totalkredits accept, kan der dog inden for lånets løbetid bevilges afdragsfrihed i en eller flere perioder i overensstemmelse med den til enhver tid gældende lovgivning. I de perioder, hvor der ikke er afdragsfrihed, tilbagebetales lånet som annuitetslån.

Lånets restgæld forfalder til fuld betaling i lånets sidste termin, og restgælden kan højst udgøre summen af de ikke betalte afdrag i de afdragsfrie perioder.
Ved en renteperiode forstås tidsrummet fra lånets udbetaling henholdsvis ordinære refinansiering frem til tidspunktet for den efterfølgende ordinære refinansiering henholdsvis lånets udløb.

Debitor er, indtil lånet er fuldstændigt afviklet, forpligtet til at forrente og afdrage lånet samt betale bidrag ved kontant at indbetale ydelserne i overensstemmelse med vilkårene for lånet. En ordinær terminsydelse består af rente, afdrag og bidrag. Renten beregnes af den til enhver tid værende restgæld.

Renten er foreløbig ansat og fastsættes af Totalkredit ved lånets udbetaling og ved eventuel senere refinansiering på basis af Totalkredits salg af det nødvendige obligationsbeløb.

Ydelserne på lånet fastsættes således, at der opnås dækning for rente og indfrielse af de i anledning af lånet udstedte obligationer, bortset fra det beløb, der ved en renteperiodes udløb skal refinansieres samt for bidrag, jf. dog afsnittet om refinansiering.

Længden af lånets første terminsperiode fastsættes ved lånets udbetaling og bliver oplyst i forbindelse med udbetalingen. Lånets første terminsydelse betales som en forholdsmæssig ydelse regnet fra udbetalingsdagen frem til afslutningen af terminsperioden.

I lånets sidste termin betales den fornødne ydelse til fuld afvikling af lånet, herunder til indfrielse af de obligationer, som ligger bag lånet. Der betales rente og bidrag indtil udgangen af terminen.

En terminsydelse skal betales kontant senest sidste rettidige betalingsdag. Sidste rettidige betalingsdag er fastsat til den sidste bankdag i forfaldsmåneden. Totalkredit kan i øvrigt fastsætte betalingssted og -form for ydelser på lånet, og kan herunder fastsætte, at debitors anvendelse af visse betalingsformer kun kan ske mod betaling af et gebyr til Totalkredit.

Ved ændring af refinansieringstidspunktet, jf. nedenstående afsnit om Refinansiering, kan Totalkredit samtidig bestemme, at forfaldsdagen og sidste rettidige betalingsdag for terminsydelser ændres.

Morarenter og gebyrer
Betales en terminsydelse ikke senest sidste rettidige betalingsdag, skal der betales morarenter. Tilsvarende gælder, hvis indfrielsesbeløb ikke betales rettidigt. Morarenten beregnes af det forfaldne beløb. Morarenten beregnes p.t. med 1,40% pr. påbegyndt måned regnet fra forfaldsdagen indtil betaling sker. Totalkredit fastsætter beregningsprincippet og morarentesatsen, der begge kan ændres uden varsel.

Totalkredit kan fastsætte regler om betaling af gebyrer for udsendelse af erindrings- og misligeholdelsesbreve o.lign. samt for andre serviceydelser m.v. i forbindelse med lånet. Totalkredit kan til enhver tid og uden varsel ændre størrelsen af fastsatte gebyrer samt fastsætte nye gebyrbelagte ydelser.

Totalkredit kan i øvrigt bestemme, at der ved en eventuel refinansiering skal betales kurtage, kursskæring el.lign. samt gebyr. Debitor skal underrettes herom mindst 1 måned før et refinansieringstidspunkt.

Bidrag
Som en del af ydelserne betales et bidrag, hvis størrelse og beregningsmåde fastsættes af Totalkredit. Bidragets størrelse oplyses i forbindelse med udbetaling af lånet.

Bidrag og beregningsprincipper kan ændres efter Totalkredits beslutning. Meddelelse herom vil i såfald blive givet til debitor med mindst 3 måneders varsel forud for en termin.

Totalkredit kan desuden fastsætte specielle bidragssatser og/eller beregningsprincipper for særlige lån eller grupper af lån. Meddelelse om ændringer i bidraget og/eller beregningsprincipperne herfor kan gives i en

2414002 2009-04-01-15.04.29 PR 1511698 02

12-May-200922151

267 G Reihdar Hansen ApS . Tlf. 63 11 00 12

terminsopkrævning. Ændres bidraget, ændres terminsydelsen i forhold hertil.

Refinansiering
Lånets restgæld refinansieres som angivet under "Rente- og betalingsvilkår". Hvis lånet udbetales i september måned, sker 1. refinansiering 1 år senere end angivet.

Totalkredit fastsætter, hvilke obligationer en refinansiering skal ske på basis af og fastsætter i øvrigt vilkårene for refinansieringen.

For lån, hvor hele lånets restgæld skal refinansieres med aftalte mellemrum, kan det i tilfælde af særlige kursforhold ved lånets udbetaling og/eller refinansiering være nødvendigt, at Totalkredit med virkning fra en 1. oktober i år, hvor der ikke skal ske refinansiering, udsteder yderligere obligationer i lånets løbetid, hvorved lånets obligationsrestgæld øges, og således at det er denne forøgede obligationsrestgæld, der skal afdrages henholdsvis indfries. En sådan udstedelse af yderligere obligationer medfører en ændring af lånets kontantrente set i forhold til den ved udbetalingen henholdsvis refinansieringen fastsatte kontantrente.

Hvis en sådan yderligere udstedelse af obligationer er nødvendig, vælger Totalkredit, i hvilke fondskoder obligationerne skal udstedes.

For lån, hvor der årligt skal refinansieres en andel af lånets restgæld, kan denne andel under særlige kursforhold være forskellig fra den aftalte.

Forudsat Totalkredits accept kan debitor i forbindelse med en ordinær refinansiering ændre størrelsen af den del af lånets restgæld, der skal refinansieres samt aftale ændring af lånets terminsantal. Det kan herunder for lån, hvor hele restgælden refinansieres, aftales, at der fremover skal ske årlig refinansiering af en del af lånets restgæld. Totalkredit fastsætter hvilke ændringer, der kan indgås aftale om. For lån, hvor der årligt skal ske refinansiering af en andel af lånets restgæld, vil ændringer normalt kun kunne gennemføres over en årrække. Indgås aftale om ændringer, vil dette medføre, at der frem til tidspunktet, hvor ændringerne er endeligt gennemført, ikke kan aftales yderligere ændringer, og at der i perioden vil blive refinansieret varierende andele af lånets restgæld.

Aftaler mellem debitor og Totalkredit om ændringer i forbindelse med en refinansiering kan kun ske, hvis debitor underskriver et dokument med angivelse af de ændrede vilkår. En sådan aftale er endvidere betinget af, at aftalen indgås, inden de af Totalkredit fastsatte frister herfor.

Totalkredit kan - med minimum 2 måneders varsel til et refinansieringstidspunkt - bestemme, at refinansieringstidspunktet, som for tiden er med virkning fra 1. oktober, ændres til en anden dato. Ændring af refinansieringstidspunktet kan ske således, at den førstkommende renteperiode enten bliver kortere eller længere. Herefter vil lånet blive refinansieret med samme interval som anført på pantebrevets forside. Totalkredit kan dog senere på ny - med samme varsel - træffe bestemmelse om ændring af refinansieringstidspunktet.

I forbindelse med en ordinær refinansiering kan der endvidere etableres afdragsfrihed, jf. ovenstående afsnit om Betalinger på lånet.

Indfrielse
Lånet er inkonverterbart og kan således kun indfries ekstraordinært ved indlevering af obligationer til Totalkredit svarende til lånets obligationsrestgæld og indfrielsestidspunkt, jf. dog nedenstående afsnit om indfrielse i en september måned forud for en refinansiering. Ved indfrielse med obligationer skal disse være af samme fondskoder som de bag lånet liggende obligationer. Delvis ekstraordinær indfrielse kan kun ske forholdsmæssig i de enkelte fondskoder bag lånet. Ved delvis indfrielse sker der en regulering af ydelsen på lånet. Ekstraordinær indfrielse kan kun ske mod betaling af et af Totalkredit fastsat gebyr.

Ekstraordinær indfrielse på tidspunktet for en refinansiering dvs. en refinansiering med virkning fra en 1. oktober skal ske med mindst 1 måneds varsel, dvs. senest den 31. august. Der kan ikke foretages ekstraordinær indfrielse i den sidste måned forud for tidspunktet for en refinansiering, dvs. i september måned. Totalkredit kan ændre disse frister.

Ved ekstraordinær indfrielse på tidspunktet for en refinansiering kan låntager indfri refinansieringsbeløbet kontant ved betaling af det beløb, der kræves til indløsning af obligationsbeløbet til pari.

Ved en ændring af refinansieringstidspunktet, jf. ovenstående afsnit om Refinansiering, ændres tidspunkterne for indfrielse tilsvarende.

2414002 2009-04-01-15.04.29 PR 1511698 02

Justitsministeriets genpartpapir.

Beregning af indfrielsesbeløb foretages med bindende virkning af Totalkredit og mod betaling af et gebyr. Ved indfrielse med obligationer skal obligationerne være overført til og registreret på Totalkredits depotkonto i Værdipapircentralen senest på indfrielsesdagen.

Ved indfrielse med kontantbeløb skal indfrielsesbeløbet være Totalkredit i hænde på det tidspunkt, der fastsættes af Totalkredit. Totalkredit kan ved kontantindfrielse stille krav om, at der stilles en efter Totalkredits skøn betryggende sikkerhed for kontantbeløbets betaling.

Hvis de på lånet frem til indfrielsestidspunktet betalte renter og afdrag er mindre end de frem til indfrielsestidspunktet påløbne renter på den bag lånet liggende obligationsrestgæld, skal forskelsbeløbet - samtidig med indleveringen af obligationer - kontant indbetales til Totalkredit. Hvis de på lånet frem til indfrielsestidspunktet betalte renter og afdrag er større end de frem til indfrielsestidspunktet påløbne renter på den bag lånet liggende obligationsrestgæld, godtgøres låntager forskelsbeløbet. Ved delvis ekstraordinær indfrielse reguleres forskelsbeløbet forholdsmæssigt.

Ved fuldstændig eller delvis ekstraordinær indfrielse pr. en anden dag end første dag i en terminsperiode skal der betales forholdsmæssig ydelse til indfrielsesdagen.

Forfald og opsigelse
Lånet forfalder helt eller delvist til øjeblikkelig indfrielse uden varsel, hvis:

- ejendommen overgår til anden anvendelse, der ville have medført en anden låntype, lavere lånegrænse, lavere værdiansættelse, eller kortere løbetid end den, hvortil lånet er ydet. Debitor har pligt til at underrette Totalkredit om ændret anvendelse,

- lånet er et forhåndslån, og garantibetingelserne ikke opfyldes, eller lånet for den pågældende ejendomskategori ikke efter endelig værdiansættelse og låneudmåling opnår sikkerhed inden for de i realkreditloven fastsatte maksimale lånegrænser, eller byggeriet ikke påbegyndes eller afsluttes inden henholdsvis 6 og 24 måneder efter låneudbetalingen, jf. bekendtgørelse om realkreditinstitutters udlån mod midlertidig garanti m.v.,

- ejendommens lovlige anvendelse hviler på en ikke personlig dispensation med en restløbetid, der enten er ubestemt eller mindre end det tilbudte låns, og ejendommen inden lånets udløb overgår til en anden ejendomskategori. Debitor har pligt til at underrette Totalkredit om ændret anvendelse.

Totalkredit kan uden varsel opsige lånet til øjeblikkelig indfrielse, hvis:

- ejendommen uden Totalkredits forudgående samtykke udlejes for en leje, der ikke giver dækning for terminsydelserne på dette og foranstående lån,

- der sker helt eller delvist ejerskifte af den pantsatte ejendom.

Særlig opsigelsesgrund
Hvis lånsøger fortier oplysninger eller afgiver urigtige oplysninger i låneansøgninger, skemaer m.v., og disse oplysninger har indflydelse på låneudmålingen eller værdiansættelsen, betragtes dette som en svigtende forudsætning for Totalkredit, der uden varsel kan ophæve låneaftalen eller opsige lånet til hel eller delvis indfrielse.

Fuldmagt
Debitor giver ved sin underskrift på pantebrevet Totalkredit bemyndigelse til for debitors regning ved refinansiering at forsyne pantebrevet med påtegning om lånets vilkår, herunder hovedstol, rentevilkår og låntype og lade denne tinglyse.

Debitor giver ved sin underskrift på pantebrevet Totalkredit bemyndigelse til at indhente oplysninger om ejendommen i Bygnings- og Boligregisteret (BBR), sålænge Totalkredit har pant i ejendommen.

Force majeure
Totalkredit er erstatningsansvarlig, hvis Totalkredit på grund af fejl eller forsømmelser opfylder aftalte forpligtelser for sent eller mangelfuldt. Selv på de områder, hvor der gælder et strengere ansvar, er Totalkredit ikke erstatningsansvarlig for tab, som skyldes

2414002 2009-04-01-15.04.29 PR 1511698 02

12-May-2009 22152

267 G Reihdar Hansen ApS . Tlf. 63 11 00 12

- nedbrud i/manglende adgang til it-systemer, eller beskadigelser af data i disse systemer, der kan henføres til nedennævnte begivenheder, uanset om det er Totalkredit selv eller en ekstern leverandør, der står for driften af systemerne,
- svigt i Totalkredits strømforsyning eller telekommunikation, lovindgreb eller forvaltningsakter, naturkatastrofer, krig, oprør, borgerlige uroligheder, sabotage, terror eller hærværk (herunder computervirus og -hacking),
- strejke, lockout, boykot eller blokade, uanset om konflikten er rettet imod eller iværksat af Totalkredit selv eller dens organisation, og uanset konfliktens årsag. Det gælder også når konflikten kun rammer dele af Totalkredit,
- andre omstændigheder, som er uden for Totalkredits kontrol.

Totalkredits ansvarsfrihed gælder ikke, hvis
- Totalkredit burde have forudset det forhold, som er årsag for tabet, da aftalen blev indgået eller burde have undgået eller overvundet årsagen til tabet
- lovgivningen under alle omstændigheder gør Totalkredit ansvarlig for det forhold, som er årsag til tabet.

Medvirken til retablering af lån ved låneomlægning
Hvis omlægningen af lån i ejendommen ikke gennemføres som forudsat, kan Totalkredit - uanset årsagen hertil - uden varsel kræve lånet/lånene retableret i ejendommen i en panteretsstilling inden for rammerne for det/de indfriede lån. Debitor er i så fald forpligtet til at medvirke til at tilpasse lånet/lånene med hensyn til hovedstol, reguleret restgæld, afdragsprofil og løbetid.

Debitor giver Totalkredit bemyndigelse til at underskrive de til retablering af prioritetsstilling m.v. nødvendige dokumenter, påtegninger m.v.

Kreditoplysninger
Debitor bekræfter ved sin underskrift på pantebrevet at have modtaget kreditoplysninger i henhold til lov om kreditaftaler.

Overdragelse af pantebrev
Dette pantebrev kan ikke overdrages til eje eller pant eller gøres til genstand for individuel retsforfølgning.

Ovenstående er dog ikke til hinder for, at et formidlende pengeinstitut, som har stillet supplerende sikkerhed for lånet, indtræder i panteretten i henhold til nærværende pantebrev i tilfælde af det formidlende pengeinstituts ekstraordinære indfrielse af lånet. Ved en sådan indtrædelse i panteretten som følge af et formidlende pengeinstituts indfrielse, forbliver pantebrevets vilkår om indfrielse og opsigelse uændrede i forhold til efterstående pant- og udlægshavere.

Ovenstående er endvidere ikke til hinder for, at pantebrevet overdrages til Nykredit Realkredit A/S, såfremt koncernforbindelsen mellem Nykredit Realkredit A/S og Totalkredit A/S måtte ophøre.

Ovenstående er endvidere ikke til hinder for, at lånet og pantebrevet overdrages til et andet koncernforbundet kreditinstitut, som finansierer lånet ved udstedelse af særligt dækkede obligationer, jf. reglerne i lov om finansiel virksomhed om fælles funding, og der kan i så fald videregives oplysninger om låntager mellem Totalkredit og det koncernforbundne kreditinstitut. Betalinger efter dette pantebrev skal i så fald fortsat ske til Totalkredit, medmindre låntager modtager særskilt meddelelse om andet betalingssted fra koncernforbundne kreditinstitut.

Ovenstående er endvidere ikke til hinder for, at dette lån, der er ydet i Totalkredits kapitalcenter F, af Totalkredit til enhver tid uden yderligere vedtagelse, kan overføres sammen med lånets pantebrev til Totalkredits kapitalcenter E. Overførslen af lån og pantebrev sker dog under alle omstændigheder senest 6 måneder efter lånetilbuddets udstedelse.

Gældsovertagelse ved ejerskifte
Totalkredit kan efter ansøgning bevilge gældsovertagelse af lånet til en ny ejer af den pantsatte ejendom, men Totalkredit forbeholder sig ubegrænset ret til at afslå bevilling af gældsovertagelse.

I øvrigt gælder Justitsministeriets pantebrevsformular B (sidste side).

Fuldmagt til udstedelse af elektronisk realkreditpantebrev
Dette dokument indeholder vilkårene for et lån i Totalkredit og en aftale om pant i fast ejendom til sikkerhed for

2414002 2009-04-01-15.04.29 PR 1511698 02

Justitsministeriets genpartpapir.

lånet. Panteretten sikres ved tinglysning af et pantebrev.

Al tinglysning forventes at blive digitaliseret i første halvår af 2009. Det betyder, at frem til digitaliseringen er indført, vil tinglysning ske ved fysisk fremsendelse af dette dokument til tinglysning. Efter digitalisering af tinglysningssystemet, kan tinglysning kun ske på grundlag af elektroniske pantebreve. Det er derfor nødvendigt, at der på grundlag af dette dokument udstedes et elektronisk realkreditpantebrev med det indhold og layout, som efter lovgivningen er påkrævet for at tinglyse den aftalte panteret.

Debitor giver derfor ved sin underskrift Totalkredit og formidlende pengeinstitut bemyndigelse til at udstede, signere og tinglyse et elektronisk realkreditpantebrev i overensstemmelse med denne aftale, men er samtidig opmærksom på, at det kan blive nødvendigt, at debitor skal underskrive nye dokumenter, for at tinglysning af panteretten kan ske.

Hvis pantebrevet kun underskrives af debitor:
Jeg erklærer samtidig at være ugift, eller at ejendommen ikke omfattes af § 18 i lov om ægteskabets retsvirkninger.

Middelfart den 21/4 20 09

Bjarne Jørgensen

Bjarne Jørgensen

Pantsætningen tiltrædes af medunderskrevne ægtefælle. Hvis ægtefællen er medejer underskrives som debitor og pantsætter.

(Ægtefælles underskrift)

Til vitterlighed om underskriftens(-ernes) ægthed, dateringens rigtighed og underskriverens(nes) myndighed:

Navn	Lene Harders Pedersen	Navn	
Stilling	Ekspeditionsmedarbejder	Stilling	Dorthe Jensen Erhvervsmedarbejder
Adresse	Brovejen 131	Adresse	Strandvejen 66
Postnr./By	5500 Middelfart	Postnr./By	5500 Middelfart
Underskrift		Underskrift	

Hvis en anden end debitor har endelig adkomst på ejendommen:
Som adkomsthaver tillader jeg herved, at pantebrevet tinglyses med ubetinget panteret.

den 20 .

Som endelig adkomsthaver

Underskrift

2414002 2009-04-01-15.04.29 PR 1511698 02

12-May-200922153

267 G Reihdar Hansen ApS . Tlf. 63 11 00 12

1511698 02

Til vitterlighed om underskriftens(-ernes) ægthed, dateringens rigtighed og underskriverens(nes) myndighed:

Navn	Navn
Stilling	Stilling
Adresse	Adresse
Postnr./By	Postnr./By
Underskrift	Underskrift

2414002 2009-04-01-15.04.29 PR 1511698 02

Justitsministeriets genpartpapir

*** * ***
* * *
* * ***
* * * Retten i Middelfart
* *** *** Tinglysningsafdelingen

Akt.nr.: 40_F_439

Påtegning på Ejerpantebrev med medd. Dkk 500.000
Vedrørende matr.nr. 4 H, Mosegård By, Balslev
Ejendomsejer: Bjarne Jørgensen
Lyst første gang den: 22.05.2009 under nr. 5664
Senest ændret den : 22.05.2009 under nr. 5664

Retten i Middelfart den 03.06.2009

Pia Richter Røgild

© JYPA 1385 NOV 1996

09-Jun-2009 2746

MIDDELFART SPAREKASSE
- vi har overskud til dig

Afgift DKK 8.900,00

Akt: Skab nr.
(udfyldes af tinglysningskontoret)

Ejerlav: Mosegård By, Balslev
Matr. nr: 4 H, parcelnr. 15
Gade og husnr.: Mosegårdvej 15

Anmelder:
Middelfart Sparekasse
Middelfart afdeling
Algade 69
5500 Middelfart
Tlf.nr. 64222222 LHP

Ejerpantebrev
(fast ejendom)

Debitor(er)s navn(e) og bopæl(e)	Bjarne Jørgensen Mosegårdvej 15 Balslev 5592 Ejby
	giver herved
Kreditor	mig/os selv eller den, til hvem nærværende ejerpantebrev måtte blive overdraget, panteret i nedennævnte ejendom uden personlig hæftelse.
Gældens størrelse kr.	Kr. 500.000,00 skriver kroner femhundredetusinde 00/100
Rente- og betalingsvilkår	Ved tvangsauktion over den/de pantsatte ejendom(me), forrentes ejerpantebrevet fra tvangsauktionstidspunktet til betaling finder sted. Renten udgør 10,00 % pr. år over Nationalbankens officielle udlånsrente på tvangsauktionstidspunktet.
Opsigelse	Med 14 dages varsel kan såvel kreditor som debitor opsige gælden.
Den pantsatte ejendom	Matr. nr.: 4 H Mosegård By, Balslev, parcelnr. 15

GENPART 061426 02 0000.0025 28.04.2009 TA
8.900,00 K

NB. Bopælsforandring skal meddeles til kreditor. Ved forsinket betaling af renter og afdrag kan kreditor forlange kapitalen indfriet, se sidste side, punkt 9 a.

09-Jun-2009 82747

Justitsministeriets genpartpapir.

Oprykkende panteret efter kr. 916.000,00 30 årigt rentetilpasningslån, Totalkredit A/S, med 10 års afdragsfrihed.

Respekterede servitutter m.v. Med hensyn til de ejendommen nu påhvilende servitutter og andre byrder henvises til ejendommens blad i tingbogen.

Særlige bestemmelser Meddelelser ifølge retsplejelovens kapitel 51 og andre meddelelser, der efter loven skal sendes til pantekreditor bedes sendt til:

Middelfart Sparekasse, Middelfart afdeling, Algade 69, 5500 Middelfart,

der iøvrigt bemyndiges til på mine vegne at underskrive påtegninger af enhver art på nærværende pantebrev, herunder kvitterings-, transport-, moderations- og relaksationspåtegninger.

I tilfælde af, at den pantsatte ejendom eller væsentlige dele heraf skifter ejer, kan kreditor uanset foranstående opsigelsesbestemmelser forlange kapitalen indfriet straks. Den i pantebrevet sædvanemæssige tekst - Justitsministeriets pantebrevsformular A pkt. 10 - indeholdte tvangsauktionsklausul gælder ikke for dette pantebrev.

I øvrigt gælder Justitsministeriets pantebrevsformular A, se sidste side.

Dato 21/4-2009

Underskrifter

Bjarne Jørgensen

Bjarne Jørgensen

For så vidt pantebrevet alene underskrives af debitor, erklærer denne samtidig at være ugift, eller at ejendommen ikke omfattes af lov om ægteskabets retsvirkninger § 18.

For så vidt debitor er gift, erklærer medunderskrevne ægtefælle samtykke til pantsætningen. Er ægtefællen medejer, underskrives som debitor og pantsætter.

Vitterligheds-påtegning Til vitterlighed om ægte underskrift/underskrifter, dateringens rigtighed og udstederens/udstedernes myndighed:

Underskrift	Underskrift
Navn (i blokbogstaver)	Navn (i blokbogstaver)
Stilling Lene Harders Pedersen Ekspeditionsmedarbejder	Stilling Gitte Brandt Ekspeditionsmedarbejder
Adresse Brovejen 131 (i blokbogstaver)	Adresse Skarøvænget 3 (i blokbogstaver)
Postnr./by 5500 Middelfart (i blokbogstaver)	Postnr./by 5500 Middelfart (i blokbogstaver)

Justitsministeriets genpartpapir

*** * ***
* * *
* * ***
* * * Retten i Middelfart
* *** *** Tinglysningsafdelingen

Akt.nr.: 40_F_439

Påtegning på Pantebrev. Dkk 620.000
Vedrørende matr.nr. 4 H, Mosegård By, Balslev
Ejendomsejer: Bjarne Jørgensen
Lyst første gang den: 13.04.2005 under nr. 7831
Senest ændret den : 18.05.2009 under nr. 5405

Aflyst af Tingbogen den 18.05.2009

Retten i Middelfart den 29.05.2009

Dorte Betzer Nielsen

10-jun-2009 9660008

© JYPA 1395 NOV 19

Justitsministeriets genpartpapir

Tinglysningsafgift DKK 0,00.

Allonge til pantebrev opr. DKK 620.000,00 med pant i matr. nr. 4 H Mosegård By, Balslev.

Anmelder: Danske Bank
Bolig Service
Ejerskifte, Sælger
Holmens Kanal 2-12
1092 København K
Telefon 45 13 52 90

Dette pantebrev kvitteres herved til aflysning af tingbogen.

Denne påtegning er anført pantebrevets side 7.

AFLYST

København, den 2. april 2009

Danske Bank

Carsten Frederiksen

John Hansen

10-Jun-2009 09:09

© JYPA 1393 MAJ 1995