DSS 88303686
40_B_649
Bulk Sort / Hvid
314220

Justitsministeriets genpartpapir

Akt: Skab nr. B - 649
(udfyldes af dommerkontoret)

2-2726-62

Matr.nr. 1 o m.fl. Billeshave Hvd., mfl.
Strib-Røjleskov

Beliggende: Ny Billeshavevej 4
5500 Middelfart

Anmelder: Adv. Flemming Borch
Langegade 12
5300 Kerteminde

Akt. 8819
Ekp. 500

BETINGET SKØDE

Undertegnede Karl Gunnar Jeppesen, Ny Billeshavevej 4, 5500 Middelfart, sælger, overdrager og betinget skøder herved til medundertegnede

Karl Erik Jeppesen
Ny Billeshavevej 4
5500 Middelfart

den mig tilhørende ejendom, matrikuleret under -

matr.nr. 1 o Billeshave Hvd., Strib-Røjleskov,	af areal	6 ha. 0.283 m^2	
matr.nr. 1 v Billeshave Hvd., Strib-Røjleskov,	af areal	4 ha. 6.709 m^2	
matr.nr. 38 b Røjle by, Røjle	af areal	3.203 m^2,	
matr.nr. 22 a Røjle by, Røjle	af areal	1 ha. 8.602 m^2,	heraf vej 325 m^2
matr.nr. 69 f Røjle by, Røjle	af areal	1 ha. 0.542 m^2,	heraf vej 375 m^2
Areal i alt		13 ha. 9.339 m^2,	heraf vej 700 m^2

Ejendommen er i tingbogen noteret som landbrugsejendom, og beliggende i landzone.

Overdragelsen finder sted på følgende af parterne vedtagne vilkår:

Jypa A/S Viby J

§ 1.

Ejendommen overdrages, således som den nu er og forefindes, og som den er køber bekendt, med de på ejendommen værende bygninger og disses grund-, mur- og nagelfaste tilbehør, herunder alle ledninger og installationer til ejendommens forsyning med el, vand og varme, samt alt i beboelsesbygningen værende inventar/ løsøre.

Overdragelsen omfatter endvidere besætning, beholdninger og driftsinventar, således som disse aktiver nærmere er specifiseret i sælgers årsregnskab pr. ultimo 199o, samt avl på roden.

§ 2.

Ejendommen overdrages med de samme rettigheder, byrder, servitutter og forpligtelser, hvormed den har tilhørt sælger, idet bemærkes, at der på ejendommen er tinglyst følgende byrder:

1957: Bygningsafstand,
1956: Dekl. i henhold til statshusmandsloven, benyttelsesindskrænkninger,
1966: Kendelse vedr. afløb ved Billeshave,
1968: Vedligeholdelse, drift, tilsyn m.m.,
1974: Overenskomst ang. etablering og fremtidig ren- og vedligeholdelse af afløbsledning for spilde- og overfladevand fra 1 n,
1932: Vej til fælles afbenyttelse for matr.nre. 22 a, 24, 47 a, 68 og 69,
1951: Dekl., hvorefter ejendommen undergivet de i lov nr. 339 af 9/6 1948 § 15 - 21 stk. 1 + 3 og § 25 fastsatte vilkår for statshusmandsbrug,
1953: Elmaster,
1955: Rørledning,
1957: Bygningsafstand,
1975: Kloakering af områder i og ved Røjle-Mose,
19o3: Vandstandsregulering i Røjle-Mose,
1974: Anbringelse af kabler i trace.

I øvrigt henvises til ejendommens blad i tingbogen.

§ 3.

Ejendommen og de øvrige aktiver overtages af køber **den 31.december 199o**, fra hvilken dato aktiverne henligger for købers regning og risiko.

§ 4.

Med overtagelsesdagen som skæringsdag udarbejdes sædvanlig refusionsopgørelse vedrørende renter, skatter og afgifter m.v. og refusionssaldoen berigtiges kontant på anfordring.

Justitsministeriets genpartpapir

Køber forpligter sig til at afgive erklæring til toldvæsnet om overtagelse af eventuelle momsreguleringsforpligtelser vedrørende investeringsgoder, således om disse forpligtelser måtte blive beregnet af parternes regnskabsfører.

Efterbetaling fra Mejeriselskabet Danmark for leverancer indtil udgangen af september 199o tilfalder sælger, medens efterbetaling for leverancer fra 1.oktober 199o tilfalder køber.

Med virkning fra overtagelsesdagen oppebærer køber alle af ejendommen flydende indtægter, og tilsvarer alle af ejendommen gående udgifter.

§ 5.

Købesummen for ejendommen og de øvrige aktiver er foreløbig aftalt til **kr. 1.o62.5oo,-** (skriver kroner enmillion sekstitotusinde femhundrede oo øre), der berigtiges således:

A. Køber overtager den på ejendommen hvilende prioritetsgæld til -

1. Nykredit, opr.kr. 49.ooo,- til rente 7% p.a. og med statutmæssige forpligtelser, pr. 11. december 199o uaflyst nedbragt til — kr. 15.537,32

2. Dansk Landbrugs Realkreditfond, opr.kr. 1oo.ooo,- til rente 12% p.a. og med statutmæssige forpligtelser, pr. 1.oktober 199o uaflyst nedbragt til — kr. 76.662,-

3. Den Danske Bank, Middelfart, iflg. "omlægningslån" (kontonr. 112671), med restgæld pr. 31.december 199o — kr. 1o4.89o,94

B. Køber optager ejerskiftelån i Dansk Landbrugs Realkreditfond med pålydende — kr. 3oo.ooo,-
til rente 1o% p.a. og med løbetid 3o år.

Sælger afholder de med den nævnte prioritering forbundne omkostninger, og modtager obligationer/ låneprovenu, når lånet er berigtiget.

Den del af købesummen, der berigtiges ved optagelse af det nævnte ejerskiftelån, forrentes af køber fra overtagelsesdagen med 1o% p.a. til sælger eller realkreditinstitut, afhængig af tidspunktet for lånets effektuering.

C. Ved købers udstedelse af gældsbrev til sælger på nærmere mellem parterne aftalte vilkår berigtiges — kr. 135.4o9,74

D. Køber har kontant betalt til sælger — kr. 3o.ooo,-

Transport — kr. 662.5oo,-

Jypa A/S Viby J

Transport	kr. 662.5oo,-
E. Ved gave fra sælger til køber berigtiges idet køber berigtiger den heraf flydende gaveafgift.	kr. 4oo.ooo,-
KØBESUM I ALT	kr. 1.o62.5oo,-

Parterne forbeholder sig at genforhandle købesummen, når værdien af besætning, beholdninger og driftsinventar kan opgøres pr. 31/12 199o, idet en eventuel regulering af købesummen vil være at berigtige kontant.

På ejendommen hæfter endvidere 3 stk. ejerpantebreve med pålydende henholdsvis kr. 55.ooo,-, kr. 25.ooo,- og kr. 2o.ooo,-, hvilke ejerpantebreve tiltransporteres køber.

§ 6.

Køber indtræder fra overtagelsesdagen i sælgers rettigheder og forpligtelser overfor lokale forsyningsværker.

Gæld, der afvikles gennem forbrug, betales af køber fra overtagelsesdagen.

§ 7.

Sælger erklærer, at der på ejendommen findes ca. 2 tdl. skov, som ifølge det oplyste ikke er fredskov.

Sælger erklærer endvidere, at der på ejendommen findes spredte forekomster af flyvehavre.

§ 8.

Parterne forpligter sig gensidigt til at befordre sælgers udtræden af - og købers indtræden i - alle rettigheder og forpligtelser i henhold til leveringsaftale med Mejeriselskabet Danmark, og alle kontrakter om levering af frø og andre afgrøder.

§ 9.

Sælger oplyser, at der pr. overtagelsedato ikke vil være uopfyldte miljøkrav vedrørende ejendommen, men såfremt ejerskiftet eller den af køber påtænkte drift af ejendommen måtte udløse krav fra offentlige myndigheder i henhold til miljølovgivningen, er sådanne krav sælger uvedkommende.

Justitsministeriets genpartpapir

Sælger oplyser endvidere, at der ikke til ejendommen er ydet moderniseringsstøtte eller anden støtte/tilskud.

§ 1o.

De med handlens berigtigelse forbundne udgifter til skødestempel, tinglysningsgebyr og advokathonorar afholdes af parterne i forening med halvdelen af hver.

Køber udreder omkostninger ved gældsovertagelse, indtræden i løbende kontrakter m.m., samt omkostningerne ved udstedelse af gældsbrev til sælger.

Nærværende dokument er udstedt til opfyldelse af en bindende aftale, indgået i tidsrummet fra den 16.maj 199o til og med den 31.december 199o om overdragelse af ejerbolig til helårsbeboelse.

Til stempelefterretning erklærer parterne, at den aftalte købesum fordeler sig således:

Værdi af fast ejendom	kr.	892.5oo,-
Værdi af besætning, anslået	kr.	15o.ooo,-
Værdi af driftsmateriel m.m., anslået	kr.	2o.ooo,-
Købesum i alt	kr.	1.o62.5oo,-

Ejendomsværdi pr. september 199o	kr.	1.o5o.ooo,-
heraf stuehusværdi	kr.	2o2.ooo,-

Skødet stemples herefter således:

1,2% af kr. 892.5oo,- x $\frac{848.ooo,-}{1.o5o.ooo,-}$ =	kr.	8.649,-
o,1% af kr. 17o.ooo,-	kr.	17o,-
	kr.	8.819,-
Tinglysningsgebyr	kr.	5oo,-
I alt	kr.	9.319,-

Nærværende skøde er alene betinget af købesummens berigtigelse som foran anført og parterne bemyndiger advokat Flemming Borch, Kerteminde, til - når forudsætningerne herfor er opfyldt - at underskrive endelig skødepåtegning.

Jypa A/S Viby J

Kerteminde, den 13/11 1990
som sælger

Karl Gunnar Jeppesen

Kerteminde, den 13/11 1990
som køber

Karl Erik Jeppesen

Til vitterlighed om underskriftens ægthed, dateringens rigtighed, samt underskriverens myndighed:

Navn: Ilse Bolsen
Stilling: adv. sekr.
Bopæl: Bankegårdsvej 10
5390 Martofte

Navn: Jeannette Dreier
Stilling: adv. sekr.
Bopæl: Kohaven 19
5300 Kerteminde

Forannævnte ejendom er under regstr. nr. 00959-8 pr. 1/1 1990
vurderet til ejendomsværdi kr. 1.050.000
heraf grundværdi kr. 215.400
Ejendommen ~~udgør~~ en landbrugsejendom.
Matr. nr. 10 ~~og 10~~ Millinge Kovad g. samt 22a 28b og 69f Rejle by.
er i matriklen noteret som landbrug. Stub - Rejy skov

MIDDELFART KOMMUNES EJENDOMSSKATTEKONTOR, den 19. novbr. 1990.

Erklæring efter landbrugslovens § 17A om erhvervelse af landbrugsejendom & afgivelse af skøde modtagelse.

MIDDELFART KOMMUNE
Ejendomsskattekontoret d. 19. novbr. 1990

H. B. Jørgensen

Justitsministeriets genpartpapir

Akt: Skab nr.
(udfyldes af dommerkontoret)

Matr.nr. 1 o m.fl. Billeshave Hvd.,
Strib-Røjleskov

Beliggende: Ny Billeshavevej 4
55oo Middelfart

Anmelder: Advokat Flemming Borch
Langegade 12
53oo Kerteminde

ENDELIGT SKØDE

Da købesummen nu berigtiget i overensstemmelse med det betingede skødes § 5, meddeles herved endeligt skøde på matr.nr. 1 o og 1 v Billeshave Hvd., Strib-Røjleskov og matr.nr. 38 b, 22 a og 69 f Røjle by, Røjle, beliggende Ny Billeshavevej 4, 55oo Middelfart, til

Karl Erik Jeppesen, Ny Billeshavevej 4, 55oo Middelfart.

Kerteminde, den 13.december 199o
iflg. fuldmagt

.....
Flemming Borch

Til vitterlighed om underskriftens ægthed, dateringens rigtighed samt underskriverens myndighed:

Navn: Tilse Balsen
Stilling: adm. sekr.
Bopæl: Bankegårdsvej 10, 5390 Martofte

Navn: Jannette Dreier
Stilling: adm. sekr.
Bopæl: Kohaven 19
5300 Kerteminde

INDFØRT I DAGBOGEN
14.12.90 009594
RETTEN I MIDDELFART
LYST.

Skødet er endeligt
Rette ejerlavsbetegnelse f. s. 10. Røjle er:
Røjle lay, Strib-Røjleskov
Den i § 2 nævnte servitut lyst i 1968 er
aflyst 7/11-1990.

Jypa A/S Viby J

Annuitetslån - konvertible obligationer - kontant

Justitsministeriets genpartspapir

10

Akt: Skab B nr. 649
(udfyldes af tinglysningskontoret)

Sag nr.:
A 07661

Matr. nr. og ejerlav: 1o Billeshave Hgd., Strib-Røjleskov m.fl.

Gade og husnr.: Ny Billeshavevej 4

Pålydende, nyt lån	305.000 Kr.
Evt. forholdmæssigt kurstab, nyt lån	0 Kr.
Restgæld/Indfrielsessum indfriede lån	301.010 Kr.
Omkostninger, indfriede lån	1.045 Kr.
Forholdsmæssige omkostninger, nyt lån	2.945 Kr.
Stempelpligtigt beløb	0 Kr.
Beregnet efter kursværdier	

Anmelder:

Navn:
DEN DANSKE BANK
Adr.: Middelfart Afdeling
Algade 35-37
5500 Middelfart
Telefon 64 41 00 44
Telefax 64 41 46 44

PANTEBREV

ikke til ordre

KONTANTLÅN

Dg 7/00

Debitors navn og bopæl: Karl Erik Jeppesen,
Ny Billeshavevej 4, 5500 Middelfart

erkender herved at skylde

Kreditors navn og bopæl: **DANSK LANDBRUGS REALKREDITFOND**
NYROPSGADE 21, 1780 KØBENHAVN V.

Lånets størrelse: 305.000,00 **kr. kontantlån (annuitetslån).**

Rente og betalingsvilkår: Den til enhver tid værende restgæld forrentes med 8,00 % om året. Renten er foreløbig ansat. Lånet tilvejebringes gennem kreditors salg af et efter kursforholdene på udbetalingsdagen fornødent obligationsbeløb. Den endelige rente og terminsydelse, som debitor uden yderligere tinglysning herved forpligter sig til at erlægge, fastsættes af kreditor ved lånets udbetaling.
Lånet er afdragsfrit i den første termin efter effektueringen, hvorefter det forrentes og afdrages med lige store kvartårlige ydelser, således at det er færdigamortiseret senest 20,00 år efter udbetalingen.
Beregningsgrundlaget og satsen for risiko- og administrationsbidraget fastsættes af Dansk Landbrugs Realkreditfond, der ligeledes er berettiget til at ændre beregningsgrundlaget og satsen under lånets løbetid med virkning for fremtidige terminsydelser.
Ydelserne beregnes kvartårligt for perioden til 1. februar, 1. maj, 1. august og 1. november og forfalder til betaling bagud henholdsvis 1. januar, 1. april, 1. juli og 1. oktober.

Opsigelse: Lånet er, bortset fra ejerskifte og misligholdelse, jfr. side 2 under punkt c, uopsigeligt fra kreditors side.

Den pantsatte ejendom: 1o, 1v Billeshave Hgd., Strib-Røjleskov af areal hhv. 6,0283 ha, 4,6709 ha
22a, 38b, 69f Røjle By, Strib-Røjleskov af areal hhv. 1,8602 ha, 0,3203 ha, 1,0542 ha

Oprykkende panteret efter: Ingen.

Respekterede servitutter: De før den 15.11.1990 tinglyste servitutter og andre byrder.

NB. Bopælsforandring skal meddeles til kreditor. Ved forsinket betaling af renter og afdrag kan kreditor forlange kapitalen indfriet, se side 3, pkt. 9a.

Særlige bestemmelser:

a. Ved lånets optagelse erlægges et kontant indskud efter de af fondens bestyrelse til enhver tid fastsatte regler. Indskuddet betales ikke tilbage.

b. Lånet kan uden forudgående varsel ekstraordinært indfries eller nedbringes med obligationer svarende til obligationsrestgælden pr. indfrielsesdagen af samme serie og rentefod som de, med hvilke lånet er effektueret.
Udtrukne obligationer kan ikke benyttes til indfrielse af lånet. Obligationerne modtages til deres pålydende værdi.
Ved ekstraordinær indfrielse eller nedbringelse af lånet forfalder førstkommende ordinære afdrag til kontant betaling.
Endvidere kan lånet med 3 måneders varsel til en obligationstermin den 1/2, 1/5, 1/8 eller 1/11 ekstraordinært indfries eller nedbringes med et så stort kontantbeløb, at obligationsrestgælden kan udtrækkes og indløses til pari. Ved kontant indfrielse kan kreditor forlange, at der stilles sikkerhed af et pengeinstitut for beløbet. Kreditor foretager med bindende virkning for debitor beregning af indfrielsesbeløb og eventuelle reguleringer af lånet som følge af indfrielsen.
Samme indfrielsesvilkår gælder, hvis lånet af kreditor kræves ekstraordinært indfriet eller nedbragt i tilfælde af lånets misligholdelse eller ved ejerskifte.

c. Foruden de i efterstående formularbestemmelse punkt 9 a-f nævnte tilfælde er kapitalen med renter og andre ydelser, hvis kreditor forlanger det og uden hensyn til uopsigeligheden straks, eller til et bestemt senere tidspunkt forfalden til betaling eller inddrivelse,
dersom det af fonden skønnes, at pantet ikke vedligeholdes tilbørligt eller afklædes for besætning og inventar, således at dele af den ved ejendommens belåning pantsatte besætning eller af inventaret bortfjernes uden at blive erstattet af tilsvarende ubehæftede løsøreværdier,
dersom debitor uden kreditors samtykke oppebærer afløsningssummer eller erstatninger for til kreditor pantsatte værdier (herunder forsikringssummer, arbejdsydelser, naturalpræstationer, rettigheder knyttet til ejendommen, afståede bygninger, arealer o.l.).

d. Debitor overtager samtidig med sin underskrift på nærværende pantebrev det personlige gældsansvar for ældre lån fra fonden, som måtte indestå i ejendommen, medmindre sådan overtagelse allerede har fundet sted.

e. Såfremt lånet helt eller delvist optages til indfrielse af andre lån i ejendommen, og låneomlægningen ikke kan gennemføres som forudsat, er jeg/vi uanset årsag hertil pligtig at medvirke til at etablere en prioritetsstilling i ejendommen, hvor hovedstolen på lånet ikke er større end de regulerede restgælde på indfriede lån, og hvor lånet ikke afdrages langsommere end indfriede lån, og løbetiden på lånet ikke overstiger løbetiden på indfriede lån. Samtidig meddeler jeg/vi fuldmagt til DLR til om nødvendigt at underskrive de nødvendige dokumenter.

I øvrigt gælder Justitsministeriets pantebrevsformular B (side 3).

Middelfart den 3.5 19 94

Som debitor: Karl Erik Jeppesen

Som ægtefælle og såfremt jeg er medejer
af ejendommen som debitor og pantsætter:

Til vitterlighed om underskrifternes ægthed, dateringens rigtighed og underskrivernes myndighed. For så vidt nærværende pantebrev kun er underskrevet af debitor, attesterer vi, der nøje kender debitors forhold, tillige, at debitor er ugift eller at ejendommen ikke er omfattet af paragraf 18 i lov om ægteskabets retsvirkninger.

Navn: H.C. REINHOLDT FULDMÆGTIG	Navn:
Stilling: Brahesborg vej 49 7000 Fredericia	Stilling: Tommy Ravn fuldmægtig
Bopæl:	Bopæl: Æblevænget 26 6600 Vejen

INDFØRT I DAGBOGEN
04.05.94 011665
RETTEN I MIDDELFART
LYST.

Dørmåtte-ordning og mange mails m. [illegible] med [illegible] og [illegible] [illegible] [illegible]

Justitsministeriets genpartpapir. Til fast ejendom.

Stempel kr.

Akt: Skab nr.
(Udfyldes af dommerkontoret)

Matr. nr.

(Ejerlejlighedsnr.)

Gade og husnr.

Anmelder:

Den pantsatte ejendom udgør udover forannævnte matrikkelnumrer endvidere matr. nr. 69 g Røjle By, Strib-Røjleskov af arela 0,0468 ha.

Endvidere anføres at korrekt arela for matr.nr. 69f Røjle By, Strib-Røjleskov udgør 0,9349 ha.

Iøvrigt vedstås pantebrevets bestemmelser i alle ord og punkter.

Middelfart, den 19/5 1994

Karl Erik Jeppesen

Til vitterlighed om underskriftens ægthed, dateringens rigtighed og underskriverens myndighed:

Navn	H.C. REINHOLDT FULDMÆGTIG	Navn	Tommy Ravn fuldmægtig
Stilling	Brahesborgvej 49	Stilling	Æblevænget 26
Bopæl	7000 Fredericia	Bopæl	6600 Vejen

INDFØRT I DAGBOGEN

20.05.94 013013

RETTEN I MIDDELFART
LYST.

Ovenstående gold lyst senest 20/12-1990.

DANFORM/EKSP.

80292 89 05

Justitsministeriets genpartpapir

Afgift: kr. 1.400

Akt: skab V nr. 649
(Udfyldes af tinglysningskontoret)

Ejerlav: Billeshave Hdg., Strib-Røjleskov m.fl.

Matr. nr.: 1o

Ejerlejlighedsnr.:

Gade og husnr.: Ny Billeshavevej 4

Anmelder:
Tlf. nr.:

ADVOKATGRUPPEN

Navn: Torben F. Møller (H)
Michael Sønderskov (H)

Adr.: Danmarksgade 8
DK-7000 Fredericia

Telefon 75 91 10 00

1076637/hb

Påtegning på pantebrev stort opr. kr. 305.000 nedlyst til kr. 220.389,43 udstedt af Karl Erik Jeppesen, Ny Billeshavevej 4, 5500 Middelfart til DLR Kredit. Tinglyst første gang den 20.05.1994.

GENPART 079084 01 0000.0041 10.03.2003 TA
1.400,00 K

Tilladelse meddeles herved til, at

matr. nr. 69g Røjle By, Strib-Røjleskov af areal 0,0468 ha

må udgå af DLR's pant.

Pantebrevet består herefter af 8 sider.

København, den 6. marts 2003

DLR Kredit A/S

A. KJÆRSGAARD

Fl. Sørensen

A 1395 NOV 1996

Justitsministeriets genpartpapir

*** * ***
* * *
* * ***
* * * Retten i Middelfart
* *** *** Tinglysningsafdelingen

Akt.nr.:
B 649

Påtegning på Pantebrev. Dkk 220.389
Vedrørende matr.nr. 1 O m.fl., Billeshave Hgd., Strib-Røjleskov
Ejendomsejer: Karl Erik Jeppesen
Lyst første gang den: 20.05.1994 under nr. 13013
Senest ændret den : 10.03.2003 under nr. 5059

Det relakserede forbliver under pantet indtil matrikulær berigtigelse har fundet sted

Retten i Middelfart den 17.03.2003

Eva Lorentzen, oass.

© JYPA 1395 NOV 1996

Retsafgift: Kr.
Stempelafgift: Kr.

Akt: B skab 649 nr.
(Udfyldes af tinglysningskontoret)

Justitsministeriets genpartpapir

Ejerlav:

Matr. nr.:
(Ejerlejlighedsnr.) 10 Billeshave Hgd., Strib-Røjleskov m.fl.

Gade og husnr.:
Ny Billeshavevej 4

Anmelder:
Tlf.nr.:

Navn:

Adr.:

DEN DANSKE BANK
Middelfart Afdeling
Algade 35-37 Telefon 63 41 40 40
5500 Middelfart Telefax 63 41 40 45

Påtegning på pantebrev stort opr. kr. 305.000,00 udstedt af

Karl Erik Jeppesen,
Ny Billeshavevej 4, 5500 Middelfart

til DANSK LANDBRUGS REALKREDITFOND, tinglyst første gang den, 20.05.1994

Nærværende pantebrev kvitteret herved til aflysning af tingbogen f.s.v. kr. 38.836,75

Pantebrevet står herefter alene tinglyst for kr. 220.389,43

Nærværende pantebrev består herefter af 6 sider.

København, den 26.01.1999

DANSK LANDBRUGS REALKREDITFOND

P. Kjeldsen Claus Mariussen

Justitsministeriets genpartpapir

Retten i Middelfart
Tinglysningsafdelingen

Akt.nr.:
B 649

Påtegning på Pantebrev. Dkk 220.389
Vedrørende matr.nr. 1 O m.fl., Billeshave Hgd., Strib-Røjleskov
Ejendomsejer: Karl Erik Jeppesen
Lyst første gang den: 20.05.1994 under nr. 13013
Senest ændret den : 01.02.1999 under nr. 2115

Retten i Middelfart den 11.02.1999

Merete Nielsen, oass.

© JYPA 1395 NOV 1996

Retsafgift: Kr.
Stempelafgift: Kr.

Akt: skab B nr. 649
(Udfyldes af tinglysningskontoret)

Justitsministeriets genpartpapir

Ejerlav:

Matr. nr.:
(Ejerlejlighedsnr.) 10 Billeshave Hgd., Strib-Røjleskov m.fl.

Gade og husnr.: Ny Billeshavevej 4

Anmelder:

Tlf.nr.:

Navn:

Adr.:

Påtegning på pantebrev stort opr. kr. 305.000,00 udstedt af

Karl Erik Jeppesen
Ny Billeshavevej 4, 5500 Middelfart

til DANSK LANDBRUGS REALKREDITFOND, tinglyst første gang den,

20.05.94

Nærværende pantebrev kvitteres herved til aflysning af tingbogen f.s.v. kr. 45.773,82 .
Pantebrevet står herefter alene tinglyst for kr. 259.226,18 .

Denne påtegning er anført på pantebrevets side 6

København, den 31 JAN. 1997
DANSK LANDBRUGS REALKREDITFOND

P. Kjeldsen I. Christensen

Matr: 1 O .

Billeshave Hgd., Strib-Røjleskov
45.773 A
Retten i : Middelfart
Indført den : 06.02.1997
Lyst under nr.: 2325

nu for 259226,18 kr.

Justitsministeriets genpartpapir. Til skøder skadesløsbreve, kvitteringer til udslettelse og andre påtegninger m. m. (vedr. fast ejendom).

Mtr. nr., ejerlav, sogn:
(i København kvarter)
eller (i de sønderjydske landsdele) bd. og bl. i tingbogen,
art. nr., ejerlav, sogn.

Gade og hus nr.:

Stempel: 25 kr.00

Akt: Skab B nr. 405
(udfyldes af dommerkontoret)

Købers / Kreditors } bopæl:

Anmelder:
EJNAR LARSEN . KNUD LARSEN
ADVOKATER
5500 MIDDELFART

/ej

005375 * -3.JULI 1974

Matr. nr. 22 a og 67 Røjle by, Strib
Røjleskov sogn

D E K L A R A T I O N

Undertegnede:

Middelfart Kommune, som ejer af ejendommen matr. nr. 22 a Røjle by, Strib Røjleskov sogn

og

Bødker Niels P. M. Jørgensen, Røjlemosevej 110, 5500 Middelfart, som ejer af ejendommen matr. nr. 67 Røjle by, Strib Røjleskov sogn

meddeler herved på egne og efterfølgende ejeres vegne Middelfart Kommunale Elværk ret til på de os tilhørende ejendomme matr. nr. 22 a og 67 Røjle by, Strib Røjleskov sogn at have kabler liggende i jorden i tracé som vist på vedhæftede kopi af matrikkelskortet.

Middelfart Kommunale Elværk har endvidere ret

Bestillingsformular D

Jensen & Kjeldskov A/S, København

til senere eventuelt at lægge flere kabler i ovennævnte tracé.

Uden forudgående anmeldelse til Middelfart Kommunale Elværk må omhandlede areal udnyttes til dyrkning af afgrøder herunder behandling med normale markredskaber. Ved andre arbejder i nærheden af kablerne, f.eks. dræning, plantning af træer, opførelse af bygninger og de dermed forbundne jordarbejder, hvorved der kan være fare for en beskadigelse af kablerne, skal anmeldelse om arbejdet foretages mindst 8 dage før dets påbegyndelse til Middelfart Kommunale Elværk der så for egen regning træffer de nødvendige foranstaltninger til sikring af kablerne.

Middelfart Kommunale Elværk eller andet vedkommende personale skal i tjenestemnliggender have fri og uhindret adgang til kablerne med værktøj og materiel Ejerens anvisninger vedrørende færdslen på ejendommen skal efterkommes, og der ydes erstatning for eventuelle forvoldte skader.

Erstatning for eventuelle markskader i forbindelse med fremføring af kablerne, herunder udgifterne ved retablering af ledningsanlæg og hegn, godtgøres af Middelfart Kommunale Elværk. Udgifterne ved udbedring af skader, som først komme for dagen på et senere tidspunkt, godtgøres ligeledes, såfremt skaderne er forvoldt ved kablernes etablering. Skaderne skal forud anmeldes til Middelfart Kommunale Elværk.

Middelfart Kommunale Elværk kan for egen regning lade denne deklaration tinglyse som servitut på den fornævnte os tilhørende ejendommen.

Justitsministeriets genpartpapir. Til fortsættelse af dokumenter.

Påtaleberettiget er Middelfart Kommunale Elværk.

Med hensyn til de på ejendommen i øvrigt hvilende servitutter, byrder og pantehæftelser henvises til ejendommens blad i tingbogen.

Middelfart, 17. juni 1974

Som ejer af matr. nr. 22 a : MIDDELFART BYRÅD
P.B.V.
Herman Jensen
/Henning Nielsen

Middelfart, den 24. juni 1974
Som ejer af matr. nr. 67:

Niels Peter Jørgensen

Bygningsmyndighedens samtykke til deklarationen meddelelse herméd i henhold til byggelovens § 4 stk. 2.

Middelfart Kommune
Bygningsmyndigheden
den 28-6-1974
P.B.V.
Herman Jensen
for/Knud E. Sørensen
H. C. Rasmussen

Bestillings-formular
X
Jensen & Kjeldskov A/S, København

INDFØRT I DAGBOGEN FOR
MIDDELFART [illegible]

- 3 JULI 1974

LYST

Genpartens rigtighed bekræftes.
Dommeren i Middelfart

K. P. Pedersen

Akt: Skab nr.
(udfyldes af dommerkontoret)

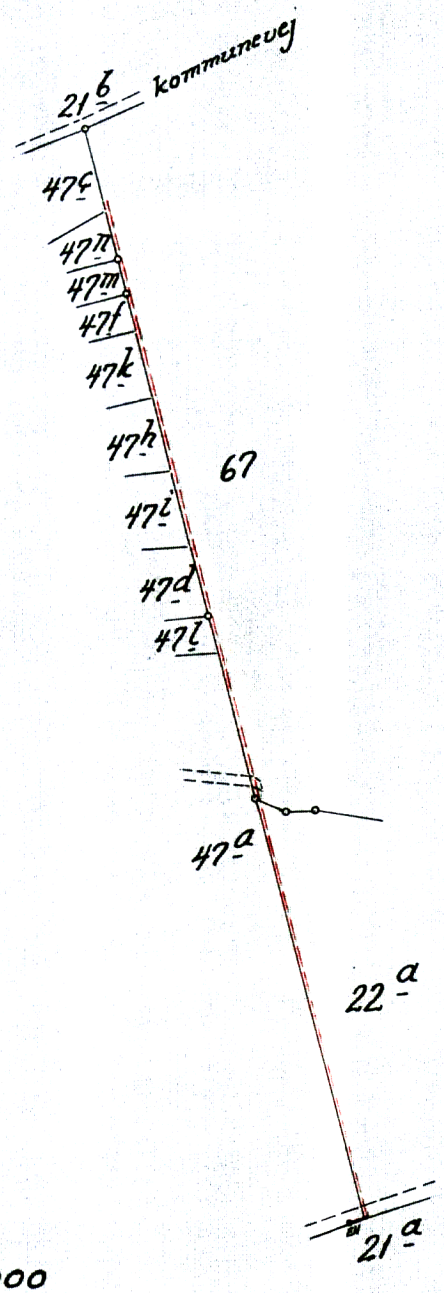

Rids i 1:4000
vedr. matr. nr. 22a og 67,
Röjle by
Strib-Röjleskov sogn.
Udfærdiget i maj 1974 til brug
ved tinglysning.

elkabel: — — —

landinspektör.

J.nr. 74-6153-1

DSS 88303686
40_B_649
Bulk Farve

314223

Jensen & Kjeldskov A/S

R.P.

At denne kort-genpart er nøjagtig genpart af det originale kort vedrørende ejendommen(e)
mtr. nr. ..... d. ..... 19 ..... Navn: .....
attesteres herved.

Justeministeriets genpartskalkerlærred. Til kort.

Bestillingsformular
Y-1 fløj

Mtr. nr., ejerlav, sogn: (i København kvarter) eller (i de sønderjydske landsdele) bd. og bl. i tingbogen, art. nr., ejerlav, sogn.

69^a og 69^f Stempel: kr.

Røjle by
Strib-Røjleskov sogn

Akt: Skab ~~A m.~~ 490.
(udfyldes af dommerkontoret)

Købers / Kreditors bopæl: B-649

Gade og hus nr.:

J.nr.74-6249-2

Anmelder:
ADVOKATERNE
THØGER HJ. JENSEN
ERIK BRODERSEN
MIDDELFART (09) *41 00 75

Servituterklæring

for matr.nr. 69^f Røjle by, Strib-Røjleskov sogn der ved landbrugsministeriets skrivelse af 28.1.1976 er fraskilt matr.nr.69^a smst.

L.22. 1.1912	dokm.ang.afgivelse af jord til off.vej.	Vedr.hverken matr.nr.69^a el.69^f.
L.18. 3.1932	dokm.ang.vej til fælles afbenyttelse for 22^a,24,47^a, 68 og 69.	Vedrører matr.nr.69^f. Vedr.herefter ikke matr.nr.69^a.
L.18. 3.1932	dokm.ang.forpligtelse til at deltage i vedligeholdelse af en over 1^b Røjle førende vej.	Vedr.hverken matr.nr.69^a el.69^f.
L.30.12.1971	dokm.ang.kloakering af områder i og ved Røjle Mose.	Vedrører ikke matr.nr.69^f.

Middelfart, den 04.FEB.1976

landinspektør

DSS 88303686
40_B_649
Bulk Sort / Hvid
314224

Justitsministeriets genpartpapir. Til skøder skadesløsbrève, kvitteringer til udslettelse og andre påtegninger m m. (vedr. fast ejendom)

Bestillingsformular D
Jensen & Kjeldskov A/S, København

Mtr. nr., ejerlav, sogn: (i København kvarter) eller (i de sønderjydske landsdele) bd. og bl. i tingbogen, art. nr., ejerlav, sogn.

1^{v} Billeshave Hovedgård, Strib-Røjleskov Sogn.

Gade og hus nr.:

Stempel: kr. øre

Akt: Skab ~~G~~ nr. ~~439~~ (udfyldes af dommerkontoret)

Købers / Kreditors } bopæl: B-649

Anmelder:

sagf. Th. Jensen

Justitsministeriets genpartpapir. Til skøder skadesløsbreve, kvitteringer til udslettelse og andre påtegninger m. m. (vedr. fast ejendom).

Servituterklæring

for matr.nr. 1^{v} Billeshave Hovedgård, Strib-Røjleskov Sogn, der ved landbrugsministeriets skrivelse af 17.2.1965 er fraskilt matr.nr. 1^{n} smst.

L. 2. 7.1956	dekl. i h.t. statshusmandslovens (l.nr.339/9.juni 1948) kap.V og IV ang.forbud mod yderligere pantsætning samt mod retsforfølgning m.m.	Vedrører matr.nr. 1^{v}.
L. 9. 2.1957	dokm.ang.bygningsafstand fra bivej.	Vedrører matr.nr. 1^{v}.

Middelfart, den 23.februar 1965

landinspektør

Bestillingsformular D

Jensen & Kjeldskov A/S, København.

Justitsministeriets genpartspapir

*** * ***
* * *
* * ***
* * * Retten i Middelfart
* *** *** Tinglysningsafdelingen

Akt.nr.:
B 649

Påtegning på byrde
Vedrørende matr.nr. 1 O m.fl., Billeshave Hgd., Strib-Røjleskov
Ejendomsejer: Karl Erik Jeppesen
Lyst første gang den: 04.09.2007 under nr. 12086
Senest ændret den : 04.09.2007 under nr. 12086

Retten i Middelfart den 13.09.2007

Marianne Westh

Ejerlav: Røjle By, Strib-Røjleskov
Matr.nr.: 22a
Kommune: Middelfart

Akt: Skab nr.

LIFA

Anmelder
LIFA A/S, Landinspektører
Landinspektører
Torvet 1, 2. sal
5500 Middelfart
Tlf. 64418100
J.nr. 20076185

Tinglysningsafgift:
1400,00 kr.

GENPART 156748 02 0000.0017 04.09.2007 TA
1.400,00 K

DEKLARATION
om
byggeretligt skel

Undertegnede ejer af matr. nr. 22a Røjle By, Strib-Røjleskov pålægger mig selv og efterfølgende ejere af ejendommen følgende bestemmelser :

Ved fremtidig bebyggelse på matr. nr. 22a Røjle By, Strib-Røjleskov, skal den efter byggelovgivningen tilladelige bygningshøjde og afstand til naboejendommen matr. nr. 67 smst. beregnes ud fra det på vedhæftede rids angivne byggeretlige skel, der er fastlagt i en afstand af 2,50 m fra den projekterede udvidelse af bebyggelsen på matr. nr. 67.

Påtaleretten tilkommer Middelfart Kommune.

Denne deklaration begæres tinglyst på matr. nr. 22a Røjle By, Strib-Røjleskov med henvisning til byggelovens § 27.

Med henvisning til ejendommens pantegæld, servitutter og andre byrder henvises til tingbogen.

Dato: 11-7-07

Som ejer af matr. nr. 22a :

Karl Erik Jeppesen

Karl Erik Jeppesen

Justitsministeriets genpartpapir

I henhold til § 42 i lovbekendtgørelse nr. 883 af 18-8-2004 om planlægning meddeles herved samtykke til tinglysning af foranstående servitutbestemmelse.

Der foreligger ikke lokalplanpligt.

Dato: 28/8 2007

Middelfart Kommune

Justitsministeriets genpartpapir

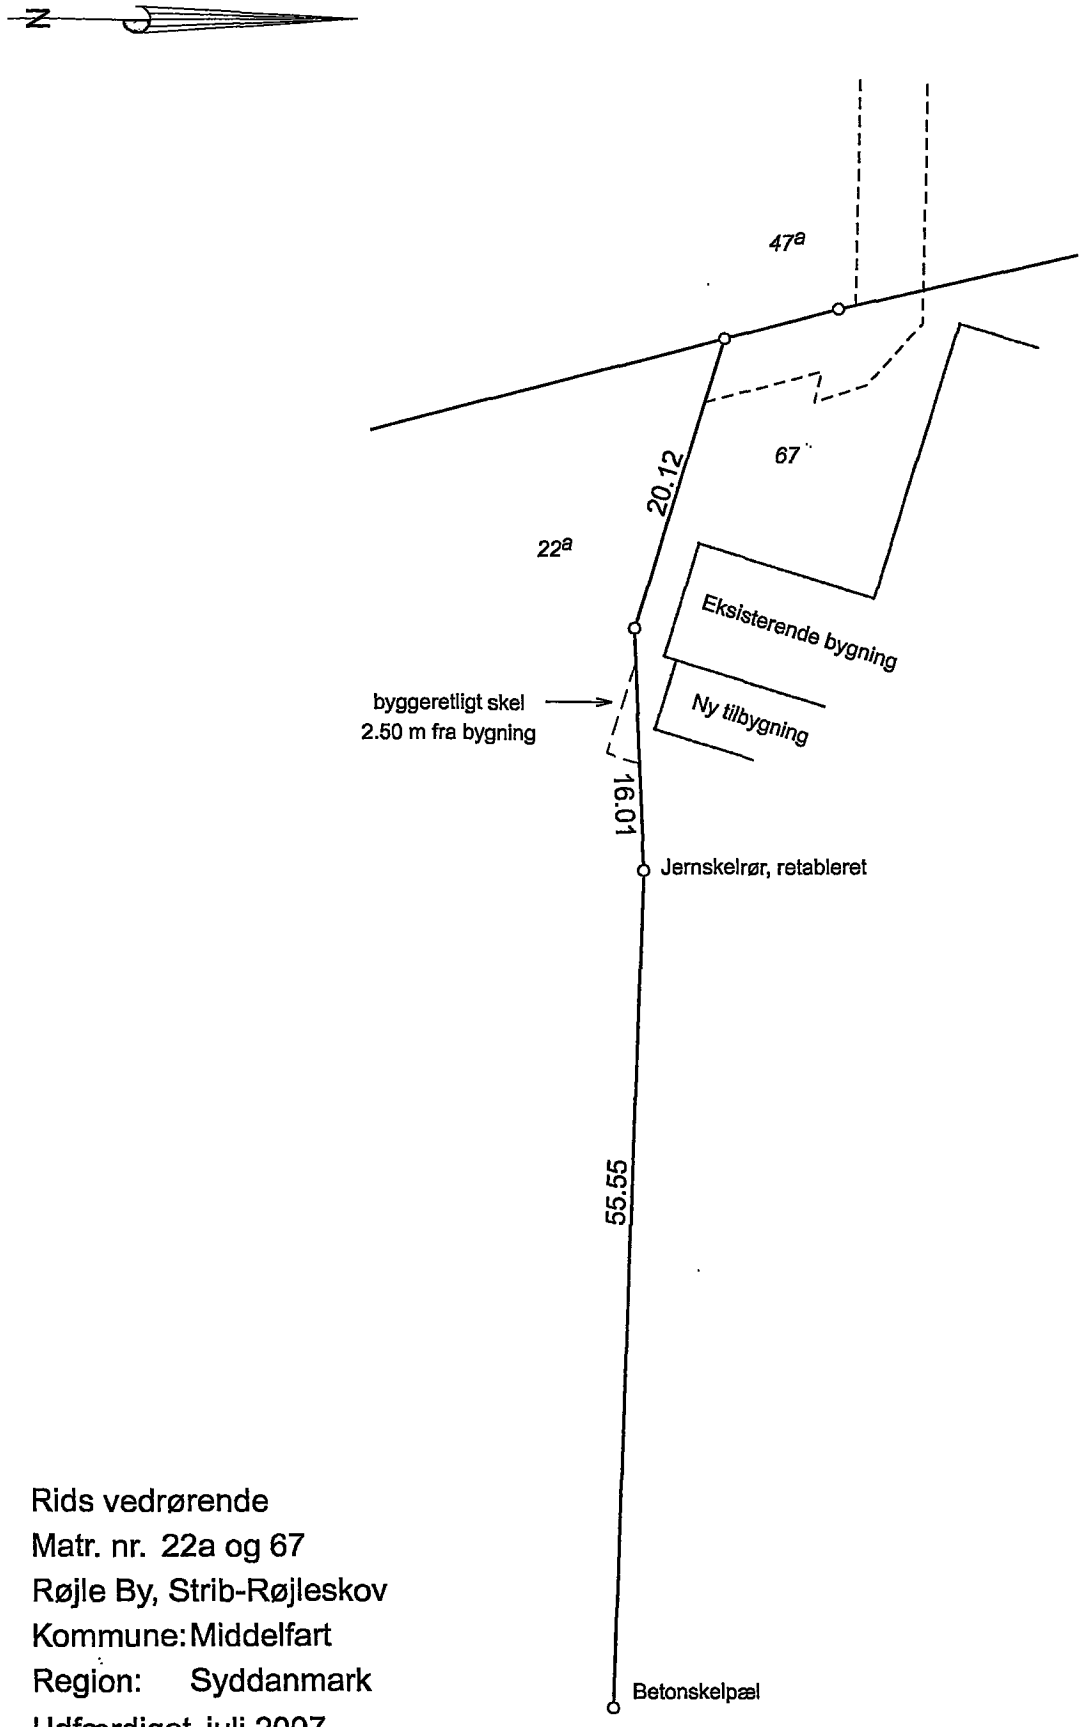

Rids vedrørende
Matr. nr. 22a og 67
Røjle By, Strib-Røjleskov
Kommune: Middelfart
Region: Syddanmark
Udfærdiget juli 2007
i anledning af deklaration om byggeretligt skel

Lsp. j. nr.: 20076185 sib

Mål: 1:500

Signe Beck
Signe Beck
landinspektør

LIFA
Landinspektører A/S

LIFA A/S Torvet 1, 2. sal 5500 Middelfart
Tlf. 64418100 Fax 64417382 E-mail land@lifa.dk
Kontorer: FREDERICIA KERTEMINDE MIDDELFART ODENSE RINGE VEJLE VISSENBJERG

Form. 267 G
Otto B. Wroblewski, Nytorv 19, 1450 København K

Justitsministeriets genpartpapir

*** * ***
* * *
* * ***
* * * Retten i Middelfart
* *** *** Tinglysningsafdelingen

Akt.nr.: 40_B_649

Påtegning på Ejerpantebrev med medd. Dkk 100.000
Vedrørende matr.nr. 1 O m.fl., Billeshave Hgd., Strib-Røjleskov
Ejendomsejer: Karl Erik Jeppesen
Lyst første gang den: 02.12.2008 under nr. 15867
Senest ændret den : 02.12.2008 under nr. 15867

Retten i Middelfart den 04.12.2008

Gitte Ørum Rasmussen

© JYPA 1395 NOV 1996

09-Dec-2008 12242

Justitsministeriets genpartpapir

Afgift: kr. 2.900

Ejerlav: Billeshave Hgd., Strib-Røjleskov m.fl.
Matr.nr.: 1 o m.fl.
Gade og husnr.: Ny Billeshavevej 4

Akt: Skab nr.
(Udfyldes af tinglysningskontoret)

Anmelder:

Navn: Danske Bank A/S

Adresse: Bolig Service
Holmens Kanal 2-12
1092 København K

Tlf.nr.: 33 44 00 00

EJERPANTEBREV
(FAST EJENDOM)

Debitors navn og bopæl: Karl Erik Jeppesen
Ny Billeshavevej 4
Billeshave
5500 Middelfart

GENPART 039460 03 0000.0025 02.12.2008 TA
2.900,00 K

giver herved

Kreditor: sig selv eller den, til hvem dette ejerpantebrev måtte blive overdraget, uden personligt gældsansvar i tilfælde af ejerpantebrevets overdragelse til andre, det være sig til ejendom, pant eller på anden måde, panteret for

Beløb: Kr. 100.000,00
Skriver kroner ethundredetusind 00/100

Rente- og betalingsvilkår: I tilfælde af at den pantsatte ejendom tvangsauktioneres, forrentes ejerpantebrevet fra tidspunktet for tvangsauktionen til betaling finder sted. Renten udgør 10% pr. år over Danmarks Nationalbanks diskonto på tidspunktet for tvangsauktionen.

Opsigelse: Ejerpantebrevet kan til enhver tid opsiges af kreditor eller debitor med 14 dages varsel.

Den pantsatte ejendom: Matr. nr.
1 o, 1 V Billeshave Hgd., Strib-Røjleskov
22 A, 38 B, 69 F Røjle By, Strib-Røjleskov

09-Dec-2008 12243

Nb! Bopælsforandring skal meddeles kreditor.
Ved forsinket betaling af renter og afdrag kan kreditor forlange kapitalen indfriet, se side 4, punkt 9 a.

© JYPA 1393 MAJ 1995
000005

Oprykkende panteret efter:	DLR Kredit A/S kontantlån	DKK	220.389,00

Respekterende Servitutter mv.:

Med hensyn til de på den pantsatte ejendom nu påhvilende servitutter og byrder henvises til ejendommens blad i tingbogen.

Særlige bestemmelser:

Meddelelser i henhold til retsplejelovens kapitel 51 og andre meddelelser, der efter loven skal sendes til pantekreditor, bedes sendt til

Danske Bank A/S
Retail Services
Holmens Kanal 2-12
1092 København K

Danske Bank A/S bemyndiges til på mine vegne at underskrive påtegninger af enhver art på dette pantebrev, herunder kvitterings-, transport-, moderations- og relaktionspåtegninger.
Den i pantebrevets sædvanemæssige tekst (Justitsministeriets pantebrevsformular A) punkt 10 indeholdende tvangsauktionsklausul gælder ikke for dette pantebrev.

Overgang til elektronisk tinglysning

Overgang til elektronisk tinglysning
Debitor giver samtykke til, at Danske Bank digitalt underskriver et enslydende elektronisk dokument på debitors vegne i det tilfælde, at pantebrevet sendes til tinglysning efter at der er indført elektronisk tinglysning i Danmark. Danske Bank kan dog i stedet bede debitor underskrive nye dokumenter, f.eks. en særskilt fuldmagt til brug for Tinglysningsretten.

Pantebrevsformular:

I øvrigt gælder Justitsministeriets pantebrevsformular A (sidste side).

Debitors underskrift:

Hvis ejerpantebrevet alene underskrives af debitor, erklærer denne samtidig at være ugift/ikke at leve i registreret partnerskab, eller at den pantsatte ejendom ikke er omfattet af § 18 i lov om ægteskabets retsvirkninger.

19-11-08	Karl Erik Jeppesen
Dato	Debitor - Karl Erik Jeppesen

Justitsministeriets genpartpapir

Ægtefælles tiltrædelse af pantsætningen:

Hvis debitor er gift/lever i registreret partnerskab, og den pantsatte ejendom er omfattet af § 18 i lov om ægteskabets retsvirkninger, giver medunderskrevne ægtefælle/registrerede partner samtykke til pantsætningen. (Er ægtefællen/den registrerede partner medejer skal der i stedet underskrives som debitor.)

Dato

Som ægtefælle eller registreret partner/som debitor og pantsætter

Vitterlighed

Til vitterlighed om ægte underskrift, dateringens rigtighed og udstederens/ udstedernes myndighed:

Navn		Navn	
Stilling	Henrik Arnold Jung Christensen privatrådgiver	Stilling	Trine Boldt senior privatrådgiver
Adresse	Elleholmvej 5, Ravnebjerg 5250 Odense SV	Adresse	Hyllehøjvej 14 5500 Middelfart
Postnr. og by:		Postnr. og by:	
Underskrift:		Underskrift:	

09-Dec-2008 12:44

© JYPA 1393 MAJ 1995

000007