DSS 88302347
76_O-A_662
Bulk Sort / Hvid
215336

Mtr. nr., ejerlav, sogn: (i København kvarter) eller (i de sønderjydske landsdele) bd. og bl. i tingbogen, art. nr., ejerlav, sogn.

21r, Øster Sundby under Aalborg købstads jorder.

Stempel: 2 kr. 00 øre

Akt: Skab 0 nr. 662 (udfyldes af dommerkontoret)

Justitsministeriets genpartpapir. Til lejekontrakter, servituttdokumenter o. l., fortsattelse af dokumenter, fortegnelse over pantsatte genstande o. l. (vedr. fast ejendom).

Anmelder:
STADSINGENIØRENS KONTOR
AALBORG

-2.OKT.1964* 13578

DEKLARATION.

AALBORG KOMMUNE som ejer af ejendommen matr.nr. 21r, Øster Sundby under Aalborg købstads jorder erklærer herved på egne og fremtidige ejeres vegne, at der pålægges ejendommen følgende servitut:

Den på vedhæftede plan viste kloakledning med tilhørende gennemløbsbrønde skal henligge uforstyrret, og der skal gives de til enhver tid berettigede adgang til eftersyn og rensning samt til at foretage reparations- og vedligeholdelsesarbejder i det omfang, kommunalbestyrelsen skønner det nødvendigt.

Uden forud indhentet tilladelse hos kommunalbestyrelsen er det forbudt på et 5,00 m bredt bælte på begge sider af kloakledningens midtlinie at bygge, foretage beplantning af træer eller buske med dybtgående rødder eller overhovedet iværksætte noget, der kan være til hinder for adgangen til anlæget eller for dets beståen eller til hinder eller skade for eftersyn, reparations- eller vedligeholdelsesarbejder. Der må til enhver tid tåles de ulemper, der kan være forbundet med eventuelle fremtidige eftersyns- eller reparationsarbejder. Erstatning for eventuel herved forvoldt skade fastsættes i mangel af mindelig overenskomst af uvildige mænd, udmeldt af retten.

Nærværende deklaration begæres tinglyst som servitutstiftende på ejendommen matr.nr. 21r, Øster Sundby under Aalborg købstads jorder.

Aalborg byråd er påtaleberettiget.

Med hensyn til de ejendommen påhvilende pantehæftelser, byrder og servitutter henvises til ejendommens blad i tingbogen.

Ifølge Aalborg byråds bemyndigelse:

AALBORG BYRÅDS
UDVALG FOR KASSE- OG REGNSKABSVÆSENET, den 28/8 1964.

Th. Christensen (sign.) Marius Andersen (sign.) Ella Christensen (sign.)

K. Østergaard (sign.) E. Thomsen Støtt (sign.)

/ Hans Nielsen (sign.)

Bestillingsformular H

Jensen & Kjeldskov A/S, København

Indført i dagbogen for
Aalborg rets 3. afd.
den -2.OKT.1964

LYST ekspr. 6/11-1964

Linde

/TT

Der meddeles herved godkendelse af ovenstående deklaration.

Bygningsudvalget i Aalborg, den 5. november 1964.

P.u.v.
E.b.
Vagner Qvist
afd.ark.

Genpartens rigtighed bekræftes.
DOMMEREN I AALBORG RET. 3. AFD

Linde

Nord

Akt: Skab nr. 662
(udfyldes af dommerkontoret)

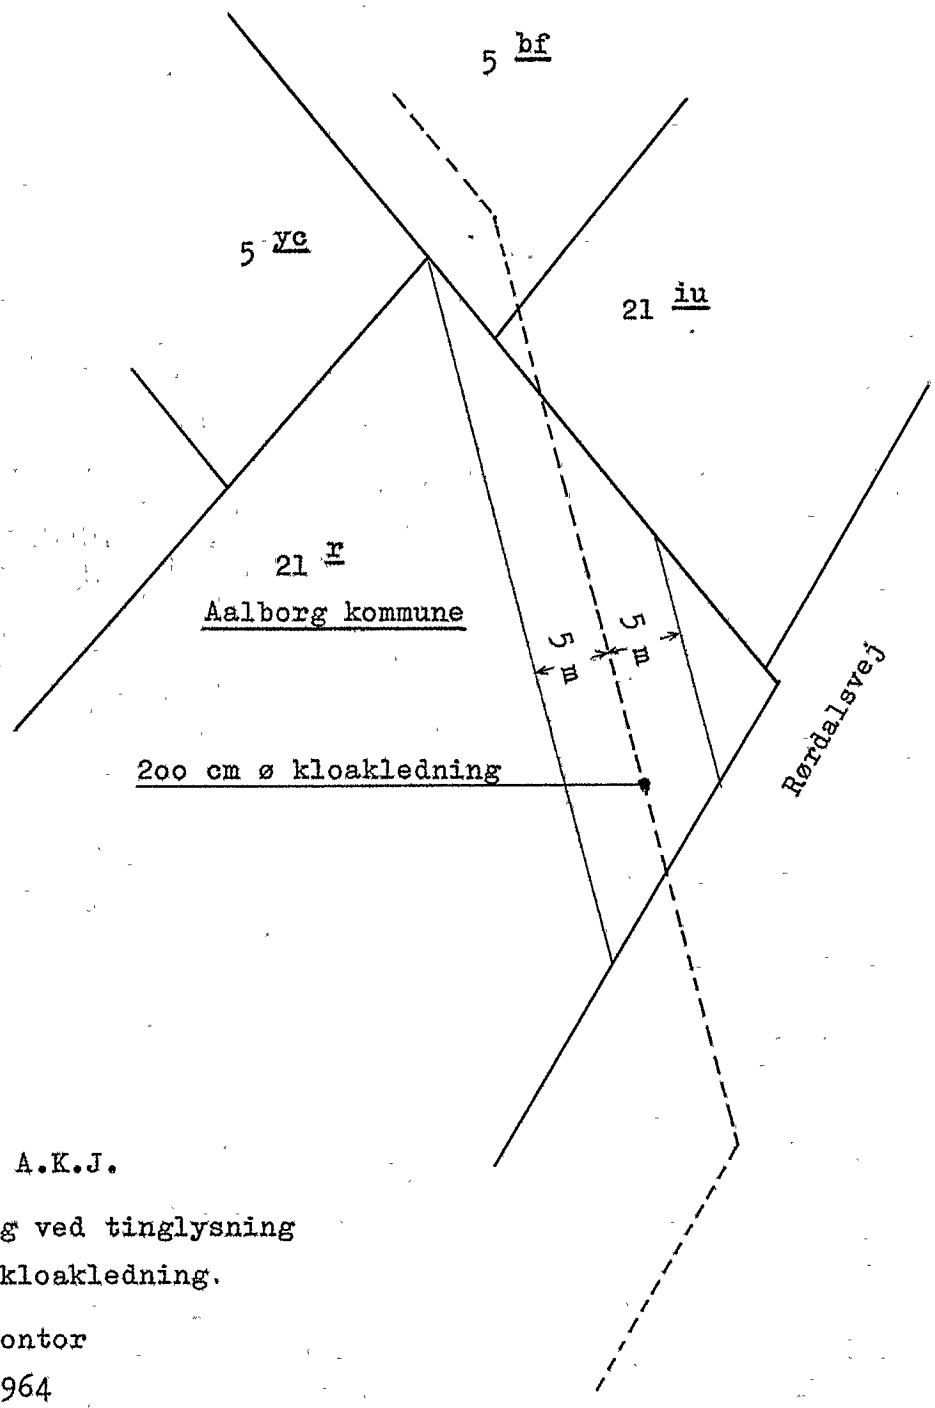

Matr. nr. 21 r
Øster Sundby under A.K.J.

Udfærdiget til brug ved tinglysning
af deklaration om kloakledning.

Stadsingeniørens kontor
Aalborg i august 1964

Målforhold 1:500

At denne kort-genpart er nøjagtig genpart af det originale kort vedrørende ejendommen(e)
mtr. nr. 21 r, Øster Sundby under A.K.J.
attesteres herved. Aalborg d. 20. august 19 64
Navn: afdelingsingeniør
Justitsministeriets genpartkalkerierred. Til kort.

Bestillings-formular
Y-1 fløj
Jensen & Kjeldskov A/S

(HAK-H)

Justitsministeriets genpartspapir. Til lejekontrakter, servitutdokumenter o.l., fortsættelse af dokumenter, fortegnelse over pantsatte genstande o.l. (vedr. fast ejendom).

Mtr. nr., ejerlav, sogn: 21r, 21iu Stempel: kr. øre *Akt: Skab* O *nr.* 662
(udfyldes af dommerkontoret)
(i København kvarter) Øster-Sundby under
eller (i de sønderjydske landsdele) bd. og bl. i tingbogen, Aalborg Købstads
art. nr., ejerlav, sogn. Jorder.

Gade og hus nr.:

Anmelder:
Landinspektørfirmaet
Nellemann, Vesteraa 1,
Aalborg.

**Stempelfri i henhold til
lov nr. 199 af 31. maj 1963
om hovedlandeveje, § 14.**

Deklaration

24.SEP.1970* 15377

I medfør af § 41 i vejbestyrelsesloven (lovbekendtgørelse nr. 342 af 9. december 1964) har Ministeren for offentlige Arbejder pålagt byggelinier på de på vedhæftede plan, udfærdiget i juni 1967 af landinspektør Poul Brassøe, angivne arealer langs de i lov nr. 386 af 4. december 1963 omhandlede motorvejsanlæg, der skal udføres i tilslutning til en tunnelforbindelse under Limfjorden.

Fremtidig bebyggelse, hvad enten bebyggelsen sker på en hidtil ubebygget del af en grund, ved ombygning af en bestående bygning eller i stedet for nedbrændte eller nedrevne bygninger skal holdes bag byggelinierne. Hvad der i henhold til foranstående gælder om bygninger, gælder også om sportspladser, kirkegårde, tankanlæg og andre anlæg af blivende art.

Byggelinierne pålægges i en mindsteafstand fra planumskant (normalt lig vejskel, hvor vejen ligger i terrænhøjde) som angivet på ovennævnte plan, idet det bemærkes, at anvendelsen af den angivne mindsteafstand forudsætter, at bygningen opføres med sin jordlinie i fremtidig vejhøjde. Er dette ikke tilfældet, skal bygningen rykkes så meget længere tilbage, som normalt svarer til 1,5 gange højdeforskellen, foruden den fornødne bredde til passage foran bygningen mindst 1 m.

Indtil det tidspunkt på hvilket Aalborg havnevæsen afhænder det byggeliniepålagte areal eller ophører med at anvende dette som havnesporareal, skal det, uanset forannævnte bestemmelser, gælde, at Aalborg havnevæsen enten ved egen eller ved Danske Statsbaners foranstaltning på det byggeliniepålagte areal kan anlægge havnespor og de dertil hørende, fornødne tekniske installationer.

vend!

Bestillingsformular G

Jensen & Kjeldskov A/S, København

Nærmere oplysninger om byggelinierne vil kunne indhentes hos stadsingeniøren i Aalborg.

Foranstående begæres, i medfør af ovennævnte lovs § 44 med prioritet forud for pantegæld og andre rettigheder over ejendommen, uanset hvornår sådanne rettigheder over ejendommene er erhvervet, tinglyst servitutstiftende for så vidt angår følgende ejendomme, der berøres af byggeliniepålægget:

Matr.nr. 21^{r}, 21^{iu} Øster-Sundby under Aalborg Købstads Jorder.

Påtaleberettiget er Ministeriet for offentlige Arbejder.

Pålagt for Ministeriet for offentlige Arbejder af Aalborg Byråd.

Ifølge Aalborg Byråds bemyndigelse

Aalborg, den 3. august 1970

Hans Brusgaard / Viktor Saaby (sign.)
rådmand sekretariatschef

indført i dagbogen for
Aalborg rets 3. afd.
den 24. SEP. 1970
LYST

Linde

Genpartens rigtighed bekræftes.
DOMMEREN I AALBORG RET 3. AFD.

Linde

AV 615 9
20.100 5

Signaturforklaring:

— — — — : Byggelinie

(HÅK-H)

Akt: Skab nr. 162
(udfyldes af dommerkontoret)

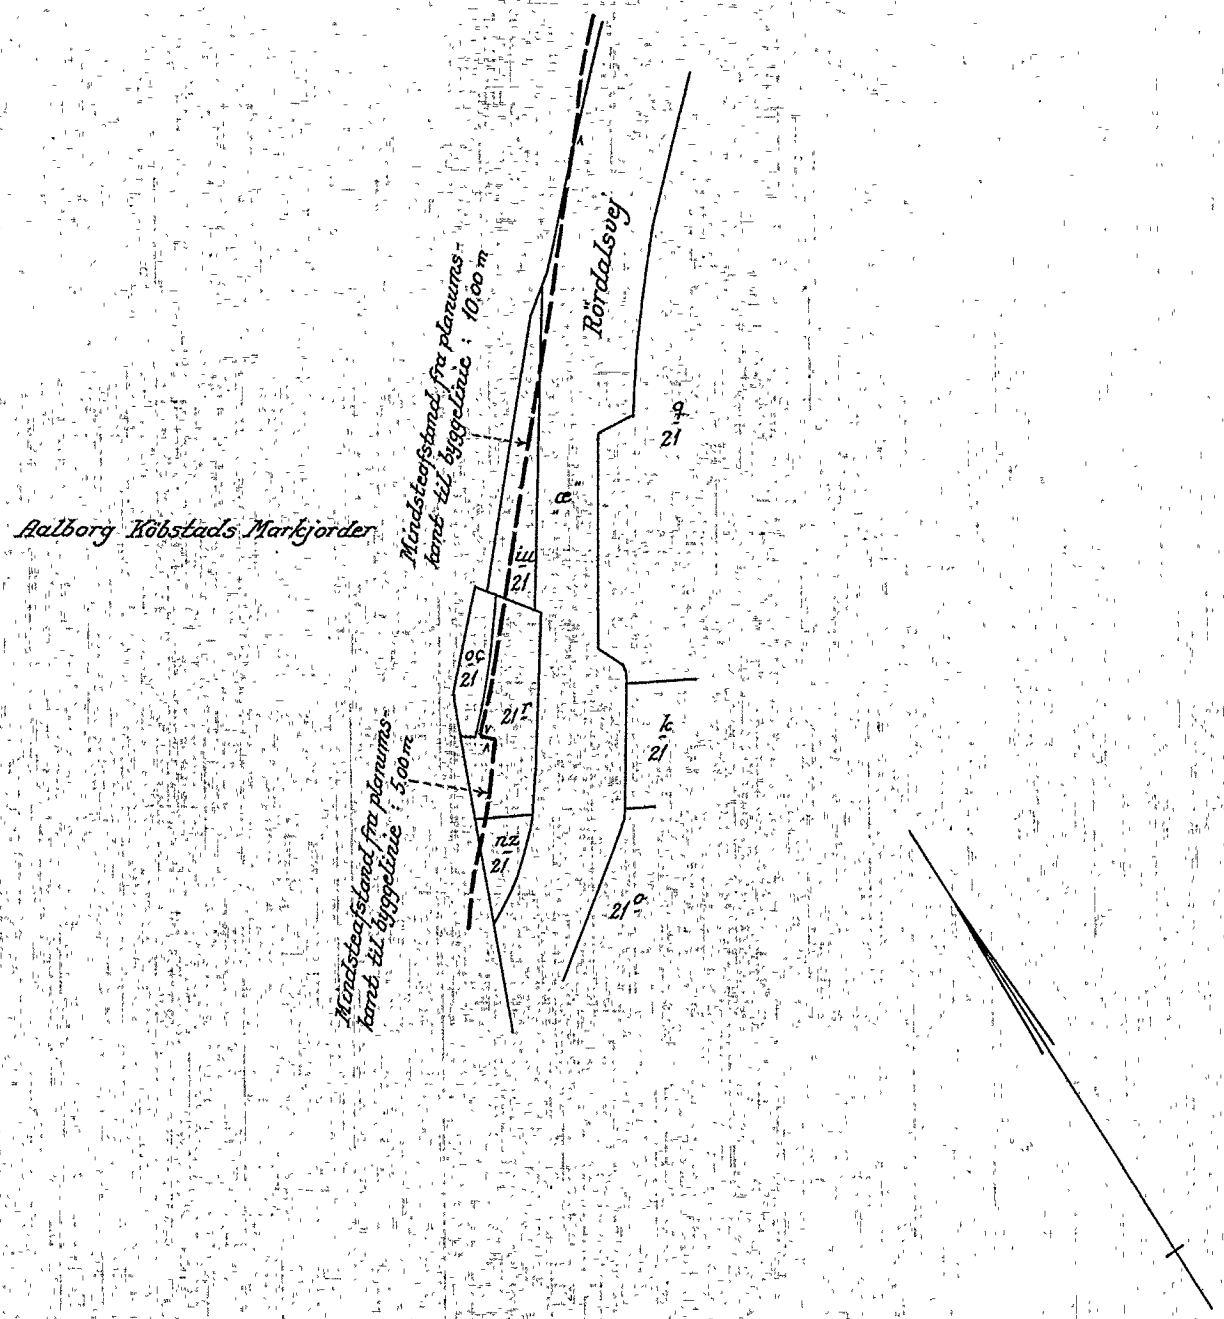

Terræn af

Öster-Sundby - Plan V

under Aalborg Köbstads Jorder

Nærværende kort er d.d. a-jour-ført.

Aalborg, den 20. august 1970

Tom Thykjær
Landinspektør

Udfærdiget til brug ved tinglysning af byggelinier i forbindelse med motorvejsanlæg i tilslutning til limfjordstunnel

Aalborg i juni 1967

Nic. Nellemann - Ib Nellemann - Axel Pedersen

Paul Brasche
Landinspektør

1:4000

At denne kort-genpart er nøjagtig genpart af det originale kort vedrørende ejendommen(e)

mtr. nr. 21 I æ, 21 iu Öster-Sundby under Aalborg Köbstads Jorder

attesteres herved. Aalborg d. 1. juni 1967

Navn: Paul Brasche

Justitsministeriets genparkalkerlærred. Til kort.

Bestillingsformular

Y-1 fløj

Jensen & Kjeldskov A/S
GB