DSS 88303795
40_P_167
Bulk Sort / Hvid
301888

Mtr. nr., ejerlav, sogn: 6 v og 57 f Stempel: 188 kr. 50 øre
(i København kvarter) Røjle m.fl.byer Strib-Røjle-
eller (i de sønderjydske lands- skov sogn
dele) bd. og bl. i tingbogen,
art. nr., ejerlav, sogn.

Akt: Skab P nr. 167
(udfyldes af dommerkontoret)

Købers / Kreditors bopæl: Røjle

Gade og hus nr.: parcel

00205

10 JAN. 1971

Anmelder: Knud Jacobsen
advokat
Middelfart

Justitsministeriets genpartpapir. Til skøder skadesløsbreve, kvitteringer til udslettelse og andre påtegninger m. m. (vedr. fast ejendom).

Betinegt skøde

Underskrevne gårdejer Jens Larsen, Røjle mark, sælger betinget skøder og overdrager herved til ligeledes medunderskrevne Vejlby-Strib ~~xxxxxxx~~ sogneråd på Vejlby-Strib kommunes vegne, under forudsætning aff landbrugsministeriets udstykningsapprobation samt tilladelse fra Assens amtsråd, en parcel af den mig i.h.t. skøde 1.19/5 1960 tilhørende landbrugsejendom:

matr.nr.6 p-9 v-21 c og 57 a Røjle m.fl.byer Strib-Røjleskov sogn, idet bem. at parcellen er opmålt i marken af landinspektøren med et areal af 30.130 m^2, der udstykkes fra matr.nr.6 p.

medens sælgeren vederlagsfrit afgiver 2310 m^2 til en 12 meter bred vej der udstykkes fra matr.nr.57 a, langs hele det østlige skel mod matr.nr 34 Røjle m.fl.byer fra Abelonelundsvejen til Sofiendalsvej, dog under forudsætning af at sælgeren får ret til vederlagsfrit at dyrke jorden til vejen skal anlægges.

Den samlede ejendom er behæftet med følgende servitutter:

decl.ang.ret for ejeren af matr.nr.6 s til vederlagsfrit at tage vand til alm.husholdning fra den på matr.nr.6 p værende brønd, således at hverken denne brønd eller den fra denne førende ledning må fjernes uden samtykke fra begge ejere 1.17/11 1937.

decl.ang.bygningsafstand fra landevej 1.28/9 1932.

decl.ang.el-master m.v.1.10/9 1952 jordfordelingsog kendelse 1.23/11 1954

decl.ang.bygningsafstand fra bivej 1.9/2 1957

decl.ang.do fra do 1.s.d.

decl.ang.bygningsafstand fra bivej 1.3/6 1957

decl.ang.el-master m.v.1.14/11 1958.

I.

Overtagelsen er fastsat til 1ste oktober 1963 og henligger det købte fra denne dato for købernes regning og risiko i enhver henseende. Refusion af skatter og afgifter s.d.

II.

Det erklæres på tro og love:

at: der ikke på det solgte findes fredskov eller fredskovpligtig grund

at: værdien af det solgte ikke overstiger købesummen

at: ejendomsskylden for den samlede ejendom er kr.44.000.00

Bestillingsformular C

Jensen & Kjeldskov A/S, København.

afgiftspligtig grundstigningsskyld kr.o.

at: evt.afgiftspligtig grundstigningsskyld der vil blive pålagt det købte overtages af køberne uden nedslag i købesummen og således at købesummen forhøjes med dette beløb.

at: køberne erklærer sig indforstået med,såfremt der bliver rejst hegn på den del af matr.nr.6 p som købes,ned mod den tilbageværende del af 6 p,at sætte dette hegn en meter fra skellet og at højden ingensinde må være over 2½m.

at: køberne meddeler sælgeren og efterfølgende ejere tilladelse til at lade kloakvand fra den tilbageværende del af 6 p støde til kommunens kloak på den købte del af matr.nr.6 p dog således at tilslutningen betales af sælgeren og skal finde sted i overensstemmelse med lovgivningens regler sp.sundhedsmyndighedernes forlangende.

Nærv.ønskes dog ikke tinglyst som servitutstiftende -.

at: endeligt skøde skal udstedes 1ste oktober 1963.

III.

Købesummen er fastsat til kr.37.662.5o skriver kroner syv og tredive tusinde seks hundrede sekstito 5o/1oo nemlig kr. 1.25 pr.m^2.

der erlægges således:

kontant på overtagelsen 1/1o 1963 betales kr.37.662.5o

ialt købesum.....kr.37.662.5o

IV.

Omkostningerne ved handelen herunder udfærdigelse,stempling og tinglysning af nærv.skøde samt udstykningen betales alene af køberne,medens sælgeren alene sørger for ejendommens frigørelse for pantegæld.

========== ========== ==========

Underskrevne Vejlby-Strib sogneråd på Vejlby-Strib kommunes vegne erklærer at have købt den omhandlede ejendom og forpligter vi os til at overholde nærv.skøde i alle ord og punkter.

Til bekræftelse med vore vidnefaste underskrifter ved nærværelse i

Middelfart,den 22.april 1963.

sælger: Jens H.Larsen

Laura Larsen-

købere:

Åge Warming Aksel Pedersen N.Nielsen O.Schultz

Søren Nielsen Karl E.Riisager O.E.Jensen Jørgen Bertelsen

Åge Hansen S.Askholm.

Til vitterlighed om underskrifternes ægthed, dateringens rigtighed og underskriverens myndighed.
Knud Jacobsen, advokat, Middelfart

Endeligt skøde.

Da parcellen nu ved landbrugsministeriets udstykningsapprobation af 14/11 1963 er udstykket og matrikuleret under matr.nr.6 v Røjle m.fl.byer Strib Røjleskov sogn skyldsat for hartkorn o-2-3-o½ alb areal 3o13o m^2 matr.nr.57 f samme skyldsat for hartkorn o-o-1-o¼ alb.areal 231o m^2 Assens amtsråds tilladelse forreligger købesummen er betalt og det betingede skødes bestemmelser iøvrigt er opfyldt, så meddeler jeg underskrevne sælger, herved køberne endeligt og ubetinget skøde på ejendommen, der her~~efter~~ skal tilhøre Vejlby-Strib kommune uden anden gæld og besvær end foran nævnt og med vanhjemmelspligt for mig efter loven.

Middelfart, den 2o/12 1963.

sælger: Jens H. Larsen

Til vitterlighed om underskriftens ægthed, dateringens rigtighed og underskriverens myndighed.
Knud Jacobsen, advokat, Middelfart

Ifølge landbrugsministeriets approbation af 14 / 11 1963 er matr. nr. 6 v Røjle m.fl. byer, Strib-Røjleskov sogn skyldsat for hartkorn o td. 2 sk. 3 fdk. o½ alb. og tildelt halvårlig tiendeydelse med 2 kr. 63 øre.

Ifølge landbrugsministeriets approbation af 14/ 11 1963 er matr. nr. 57 f Røjle m.fl. byer, Strib-Røjleskov sogn skyldsat for hartkorn o td. o sk. 1 fdk. o¼ alb. og tildelt halvårlig tiendeydelse med – kr. – øre. Arealet, der ikke er særskilt vurderet, er ikke i matriklen noteret som del af en samlet ejendom. Arealet, som ved seneste vurdering pr. 1. september 19 6o er ansat til grundværdi under eet med landbrugsejendommen matr. nr. 6p, 9v m.fl. er en del af en landejendom. jfr. § 26 i landbrugsministeriets bekendtgørelse af 25. september 1951, hvis grundbeløb i henhold til lov om vurdering og beskatning til staten af faste ejendomme udgør 6.8oo kr.
Konto 17333

ASSENS AMTSTUE, den 26. november 1963.

P. Thomsen
fuldmægtig

Indført i dagbogen for retskreds nr. 42
Middelfart købstad m.v., den 10
Akt: skab P nr. 167
Lyst tingbog

Skødet er endeligt.

Parcelkort og Servitutattest forevist

Kommunens Rigtighed bekræftes
Bemyndigen i Middelfart d. 11. 8.

Erik Hansen

Mtr. nr., ejerlav, sogn: 22 a og 3 g af Røjle by, Strib-Røjleskov sogn.
(i København kvarter)
eller (i de sønderjydske landsdele) bd. og bl. i tingbogen,
art. nr., ejerlav, sogn.

Gade og hus nr.:

Stempel: 730 kr. 00 øre

Akt: Skab B nr. 405
(udfyldes af dommerkontoret)

Købers / Kreditors } bopæl: Røjle.

Anmelder:

01213

26 FEB. 1965

Landsretssagfører
EJNAR LARSEN
(fh. Otto Rasmussen & Ejnar Larsen)
MIDDELFART - TELF. 32 og 532

Betinget Skøde.

* * * * * * * * * * * *

Undertegnede privatskiftende arvinger i boet efter frøken Abelone Kathrine Nielsen, Brendewkov pr. Strib, død den 28. august 1964, nemlig:

1) gårdejer Albert Nielsen, Nytoftegård pr. Middelfart, og
2) gårdejer Niels Marius Nielsen, Indslev Tårup pr. Ejby,

erkender herved at have solgt og overdraget betinget af købesummens rette betaling og betinget af Assens Amtsråds sanktion og betinget af at staten ikke gør sin forkøbsret gældende, til Vejlby-Strib Kommune pr. Røjle, den boet tilhørende landbrugsejendom, vurderet og skyldsat under

		for hartkorn:
Matr.nr. 22 a	Røjle by, Strib-Røjleskov sogn:	1 tdr. 7 skp. 0 fdk. 0½ alb.
" " 3 g	" " " " :	0 " 1 " 2 " 0¼ "

og med et areal, der ifølge matrikelskort udfærdiget i oktober 1964 udgør ialt 148.651 m², heraf vej 1.420 m² med de på ejendommen stående bygninger og med samtlige installationer.

Der medfølger hverken besætning, maskiner, redskaber eller avl, derimod medfølger den på gården værende gødning samt kunstgødning.

Ejendommen overdrages Kommunen i den stand, hvori den nu er og forefindes, hvorved bemærkes, at boet er ganske uden ansvar for mangler eller fejl ved bygningerne, og uden noget krav på arvingerne eller boets medhjælper.

Ejendommen overdrages iøvrigt køberen medde rettigheder, byrder og forpligtelser, hvormed den hidtil har været ejet og hvorved bemærkes at ifølge Landbrugsministeriets skrivelse af 12/5-1964 udgør 22 a i forening med 3 g en landbrugsejendom. Endvidere bemærkes, at der på ejendommen er lyst følgende servitutter:

Justitsministeriets genpartpapir. Til skøder skadesløsbreve, kvitteringer til udslettelse og andre påtegninger m. m. (vedr. fast ejendom).

Bestillingsformular C

Jensen & Kjeldskov A/S, København.

1) 14/9 -1903: Dok. ang. vandstandsregulering ang. 3 g.
2) 22/1 -1912: Dok. ang. afgivelse af jord til off. bivej, ang.3g.
3) 18/3--1932: Dok. ang. fælles vej mellem ejerne af 22 a, 24, 47 a, 68 og 69.
4) 25/6 -1955: Dok. ang. forkøbsret for staten i medfør af lov 339 af 9/6-48 § 8 stk. 2.

Handelens vilkår er iøvrigt følgende:

1.

Overtagelsen finder sted den 1. januar 1965 men henligger ejendommen dog allerede fra i dag at regne for Kommunens regning og risiko i enhver henseende, således at Kommunen også i tilfælde af ildsvåde oppebærer bygningernes brandassurancesum til anordningsmæssig anvendelse, hvorved bemærkes, at ejendommen er brandforsikret i Landbygningernes almindelige Brandforsikring for kr. 82.600,oo.

2.

Med overtagelsesdagen som skæringsdag udfærdiges iøvrigt almindelig refusionsopgørelse.

3.

Sælgerne oplyser på tro og love, at der ikke dem bekendt findes flyvehavre på ejendommen.

4.

Kommunen overtager rettigheder og forpligtelser med hensyn til Kolding Andelsslagteri, Røjle Englav.

5.

Sælgerne forpligter sig til inden overtagelsesdagen at have fjernet alt fra ejendommen af maskiner, redskaber, avl, bohave m.v., hvorimod gødningen som foran anført følger med ejendommen.

6.

Købesummen er fastsat til kr. 146.000,oo, hvilke et hun.

Justitsministeriets genpartpapir. Til skøder skadesløsbreve, kvitteringer til udslettelse og andre påtegninger m. m. (vedr. fast ejendom).

Mtr. nr., ejerlav, sogn:
(i København kvarter)
eller (i de sønderjydske landsdele) bd. og bl. i tingbogen,
art. nr., ejerlav, sogn.

Gade og hus nr.:

Stempel: kr. øre

Akt: Skab nr.
(udfyldes af dommerkontoret)

Købers / Kreditors } *bopæl:*

Anmelder:

Indført i dagbogen for retskreds nr. 43:
Middelfart købstad m. v., den 26 FEB. 1965
Akt: skab nr.
Lyst tingbog B 405
Skab I

Skødet er endeligt.

Companions Rigtighed bekræftes
Dommeren i Middelfart d. u. s.

Erik Hansen

Bestillings-formular
D

Jensen & Kjeldskov A/S, København.

drede og firtiseks tusinde kroner oo øre, køberne afgør og berigtiger på følgende måde:

a) Køberne overtager eller indfrier uden ansvar for sælgeren den i ejendommen indestående gæld til Rønnemosegårds Legat stort.....
.....kr. 7.500,oo
Hvad der eventuelt måtte være afdraget på denne gæld kommer sælgerne tilgode.

b) Resten af købesummen....." 138.500,oo
betales kontant og uden renter, såsnart Amtsrådets tilladelse foreligger og endeligt skøde er udfærdiget.

Ialt købesum.....kr.146.000,oo

7.

Omkostningerne ved dette skøde deles lige mellem kommunen og boet. Boet betaler alene mæglersalæret.

* * * * * * * * * * *

Sælgerne erklærer at der ikke på ejendommen findes fredskov, hvorimod der på et lille hjørne står noget kratskov, hvorfor nærværende skøde for alles tilfældes skyld vil blive indsendt til skovtilsynet.

Sælgerne oplyser, at ejendomsskylden andrager kr. 62.000,oo, grundværdien kr. 26.500,oo, afgiftspligtig grundstigningsskyld 0 kr.

Eventuel kommende afgiftspligtig grundstigningsskyld, der vil blive pålagt ejendommen efter nærværende handel overtager køberne uden nedslag i købesummen.

Underskrevne Vejlby-Strib Kommune modtager nærværende betingede skøde, hvis bestemmelser vi underkaster os.

Vi, underskrevne sælgere, forpligter os til såsnart det betingede skødes bestemmelser er opfyldt at udstede endeligt og ubetinget skøde til køberne fri for anden gæld og besvær end foran nævnt og med hjemmelspligt for os efter loven. Vi befuldmægtiger samtidig landsretssagfører Ejnar Larsen, Middelfart, til på vore vegne at modtage og kvittere for købesummen, samt til at udstede endeligt skøde til køberne.

Middelfart, den 23/12-1964.

Som sælgere:

Albert Nielsen

Marius Nielsen

Til

vitterlighed om underskrifternes ægthed, dateringens rigtighed, underskrivernes myndighed:

Dorthy Sørensen	Ejnar Larsen	H. Brinch Hansen
kontorass.	landsretssagfører	kontorass.
Middelfart	Middelfart	Asperup

Røjle, den 30/12-1964.

Som køber:

Aage Warming	Axel Pedersen	
Jørgen Bertelsen	Aage Hansen	
Svend Fogh Sørensen	Karl E. Risager	A. E. Jensen
S. Askholm	Søren Nielsen	
Erik Christoffersen		

Forannævnte ejendom er under løbe nr. 42 pr. 1/9 19 64
vurderet til ejendomsværdi ..... kr. 61.900
heraf grundværdi ..... kr. 26.400
grundbeløb i henhold til lov om vurdering og beskatning til staten af faste ejendomme udgør .. kr. 17.240
~~afgiftspligtig grundstigning i henhold til § 58 i lov om vurdering og beskatning til staten af faste ejendomme udgør ..... kr.~~

Ejendommen udgør en landejendom. Matr. nr. 3 g, 22 a Røjle m.fl. byer,
er i matriklen noteret som landbrug ~~husmandsbrug~~ Strib-Røjleskov sogn
Konto 17316

ASSENS AMTSTUE, den 9. januar 1965.

S. B. Sørensen
Fuldmægtig

E. V. Poulsen
Kt. Ass.

Bestemmelserne i statshusmandslovens § 8, stk. 1-5 er ikke til hinder for tinglysning af nærværende skøde.

Statens Jordlovsudvalg,
den 02. februar 1965
P.U.V.
E.B.
Sten Ryum

E n d e l i g t S k ø d e .

* * * * * * * * * * *

Da køberne nu har berigtiget den akkorderede købesum i overensstemmelse med det betingede skødes bestemmelser, så gøres dette herved endeligt og ubetinget.

Middelfart, den 25. februar 1965.

Som sælger:

Iflg. fuldmagt:

Ejnar Larsen

Til vitterlighed om underskriftens ægthed, dateringens rigtighed samt om underskriverens myndighed:

H. Brinch Hansen	Kirsten Petersen
kontorass.	kontorelev
Asperup	Middelfart

Mtr. nr., ejerlav, sogn:
(i København kvarter)
eller (i de sønderjydske landsdele) bd. og bl. i tingbogen,
art. nr., ejerlav, sogn.

matr.nr.22a
Røjle by m.m.
Strib-Røjleskov sogn

Stempel: 25 kr.

Akt: Skab B nr. 405.
(udfyldes af dommerkontoret)

Købers / Kreditors bopæl:

Gade og hus nr.:

Anmelder:

J.nr.77-6105-2

LANDINSPEKTØRERNE
MØLLER CHRISTENSEN
W. DOLLERUP - FR. RIEGELS
LEHMANN MADSEN
EJLIF BERTELSEN
5500 MIDDELFART - (09) 41 03 82

Justitsministeriets genpartpapir. Til skøder skadesløsbreve, kvitteringer til udslettelse og andre påtegninger m.m. (vedr. fast ejendom).

Deklaration

I forbindelse med byggemodning har Middelfart kommune stillet krav om tinglysning af følgende bestemmelse:

De til enhver tid værende ejere af matr.nr. 22a Røjle by m.m., Strib-Røjleskov sogn, er pligtige til at drage omsorg for, at der på de på vedlagte rids målsatte og med skravering angivne oversigtsarealer, hverken varigt eller midlertidigt forefindes noget af større højde end 1 m over en flade gennem de tilstødende vejes midtlinier. Denne bestemmelse omfatter ikke sne.

Påtaleberettiget er Middelfart byråd.

Foranstående begæres tinglyst på ovennævnte matr.nr. 22a Røjle by m.m., Strib-Røjleskov sogn, idet der med hensyn til de ejendommen påhvilende pantehæftelser, servitutter og andre byrder henvises til tingbogen.

Dato: Som ejer af matr.nr. 22a:

Foranstående deklaration godkendes.

Dato: 6.3.1978 Som kommunalbestyrelse:

P.b.v.

sign/Herman Jensen sign/Knud E.Sørensen

Bestillingsformular D

Jensen & Kjeldskov A/S, København

INDFØRT I DAGBOGEN
20.03.78 03574
RETTEN I MIDDELFART
LYST

Genpartens rigtighed bekræftes.
Dommeren i Middelfart

Akt: Skab nr.
(udfyldes af dommerkontoret)

Justitsministeriets genpartkalkerlærred. Til kort.

At denne kort-genpart er nøjagtig genpart af det originale kort vedrørende ejendommen(e)

mtr. nr. _____ Navn _____

attesteres herved _____ d. _____ 19 _____

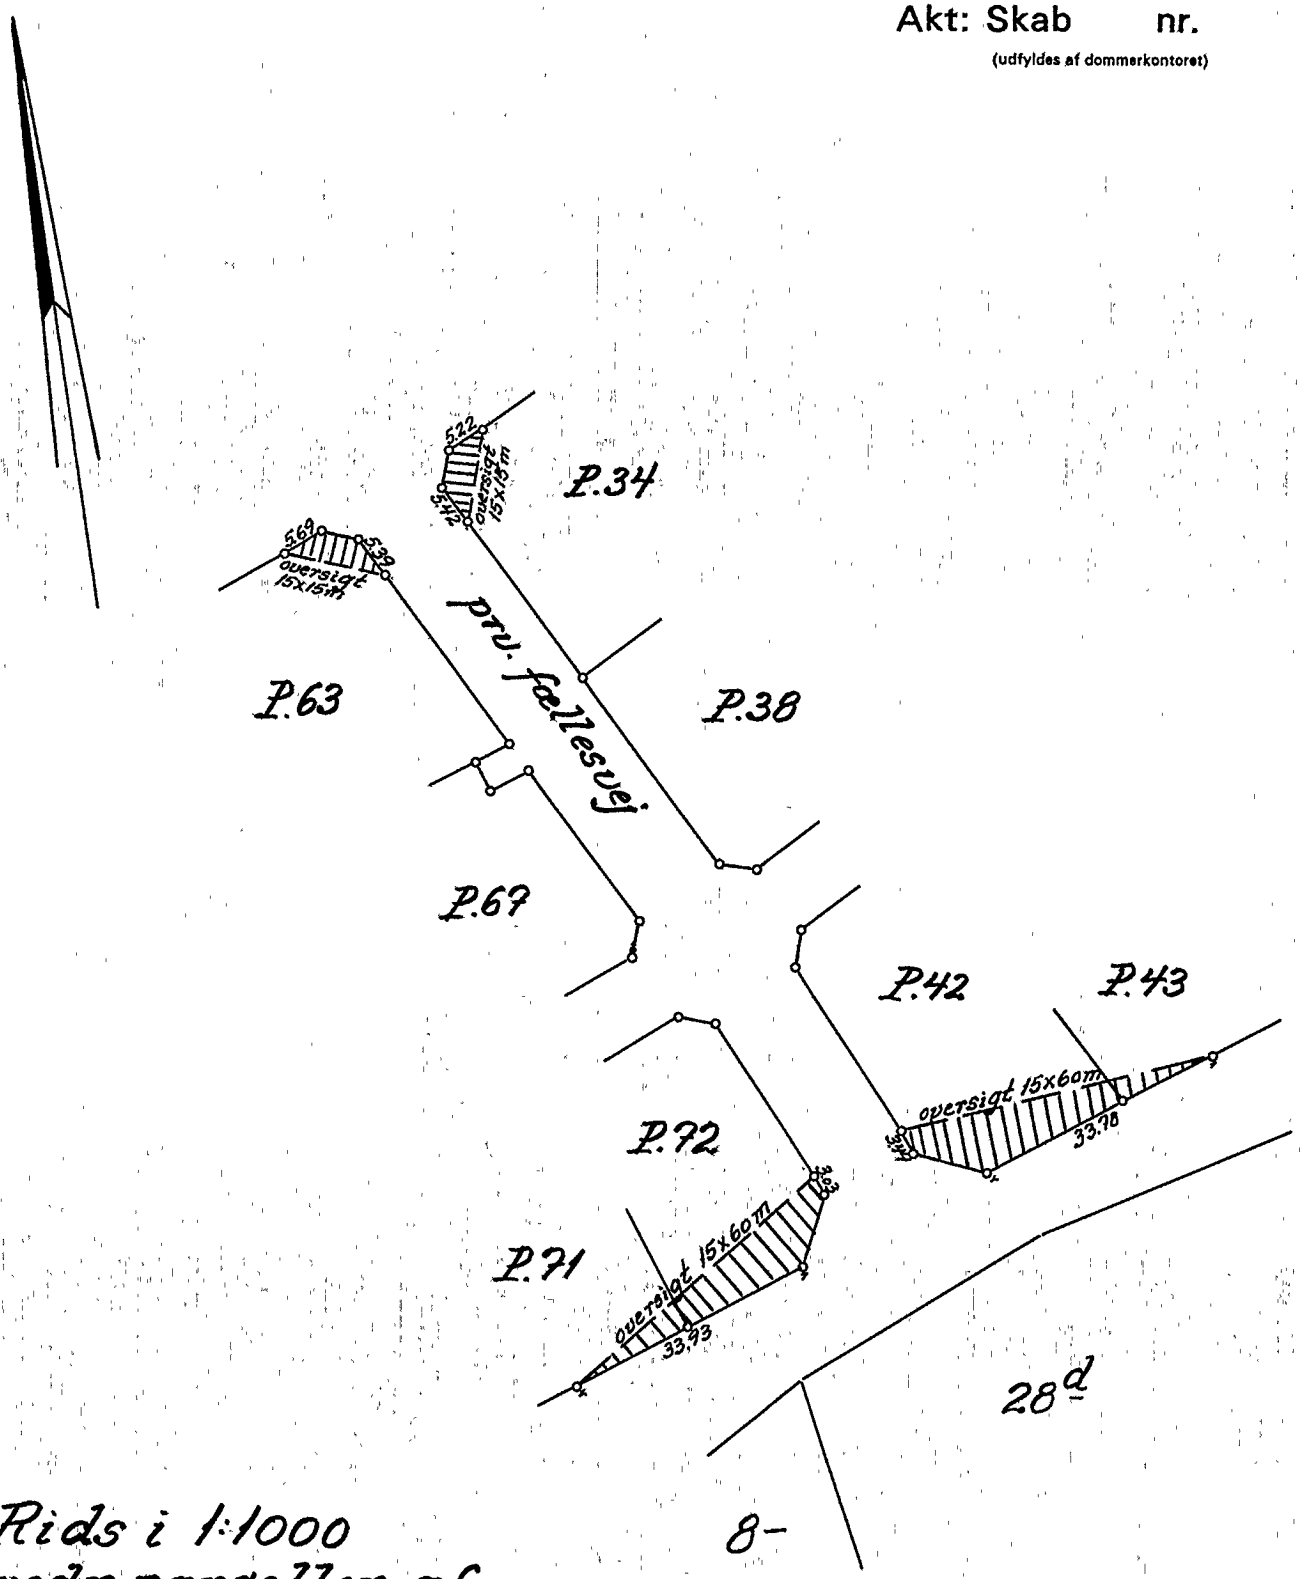

Rids i 1:1000
vedr. parceller af
matr.nr. 22a
Röjle by m.m.
Strib-Röjleskov sogn
Udfærdiget i februar 1978

LANDINSPEKTØRERNE
MØLLER CHRISTENSEN IV. DOMLRUP LEHMANN MADSEN
FR. RIEGELS EJLIF BERTELSEN
landinspektør
8680 ÅRUP (09) 48 12 56
8883 HARBY (09) 79 10 28
8600 MIDDELFART (09) 41 03 82

J.nr. 77-6105-2

Bestillingsformular
Y - 1 fløj
Jensen & Kjeldskov A/S

Mtr. nr., ejerlav, sogn: (i København kvarter) eller (i de sønderjydske landsdele) bd. og bl. i tingbogen, art. nr., ejerlav, sogn.

6^V Røjle by m.m., Strib-Røjleskov sogn.

Stempel: kr. VIO 614 9622

Akt: Skab P nr. 167 (udfyldes af dommerkontoret)

Købers / Kreditors bopæl:

Gade og hus nr.:

M197/73

006817 * 24. JULI 1973

Anmelder:

LANDINSPEKTØRERNE
MØLLER CHRISTENSEN
WILLY DOLI ERUP
LEHMANN MADSEN
FREDERIK RIEGELS
5500 MIDDELFART
TLF. (09) 41 03 82

Deklaration

Som betingelse for udstykningstilladelse har Fyns amtsråd, vejinspektoratet stillet krav om tinglysning af nedennævnte bestemmelser på matr. nr. 6^V Røjle by m.m., Strib-Røjleskov sogn.

Således foranlediget pålægger undertegnede Middelfart byråd som ejer af matr.nr. 6^V Røjle by m.m., Strib-Røjleskov sogn herved nævnte ejendom - jfr. vedhæftede rids - bestemmelser om,

at parcel 2 af matr.nr. 6^V Røjle by m.m., Strib-Røjleskov sogn fremtidig alene har adgang til landevej 614, Stribvejen, ad en overkørsel til brug for regnvandsbassin og

at der af ejeren opsættes og fremtidig vedligeholdes fast ubrudt hegn i skellet mellem parcel 2 og landevejen.

Påtaleberettiget er vejbestyrelsen ved Fyns amtskommune, vejinspektoratet.

Idet der med hensyn til pantehæftelser, servitutter og andre byrder henvises til tingbogen begæres ovenstående tinglyst servitutstiftende på matr.nr. 6^V Røjle by m.m., Strib-Røjleskov sogn.

Dato: 11.7.1973

Som ejer af matr.nr. 6^V:

Middelfart kommune

.....

P.u.v.

sign. Poul Andersen / Knud E. Sørensen

.....

Nærværende deklaration godkendes.

Fyns Amtskommune, Vejinspektoratet. Odense, den 19.7.1973

sign/ C.E. Vested.

Justitsministeriets genpartpapir. Til skøder skadesløsbreve, kvitteringer til udslettelse og andre påtegninger m. m. (vedr. fast ejendom).

Bestillingsformular D

Jensen & Kjeldskov A/S, København

INDFØRT I DAGBOGEN FOR
MIDDELFART KØBSTAD m. v.

24 JULI 1973

LYST

Genpartens ligelydende bekræftes.
Dommeren i Middelfart „d. u. s."

C. H. Henningsen
Retsassessor

Akt: Skab nr.
(udfyldes af dommerkontoret)

Pcl. 1 af 6v

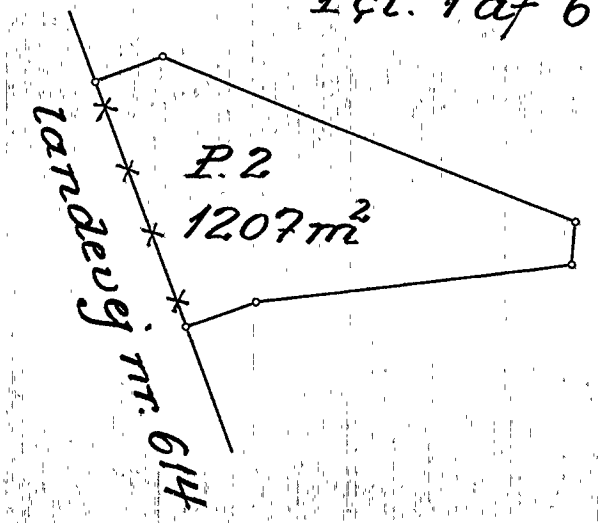

—×—×—×— : fast ubrudt hegn.

Rids i 1:1000 vedr.
matr. nr. 6v
Röjle by m.m.
Strib-Röjleskov sogn

Udfærdiget i juli 1973 til brug ved tinglysning.

landinspektör

Jm. M 197/73

Jensen & Kjeldskov A/S

LANDINSPEKTØRERNE
MØLLER CHRISTENSEN WILLY DOLLERUP LEHMANN MADSEN HENRIK RIEGELS

Justitsministeriets genpartkalkerlærred. Til kort.

At denne kort-genpart er nøjagtig genpart af det originale kort vedrørende ejendommen(e)
mtr. nr. ..... Navn: .....
attesteres herved. ..... d. ..... 19 .....

Bestillingsformular
Y-1 fløj

Mtr. nr., ejerlav, sogn: 3g, 38a, 69a, 68a og 47a.
(i København kvarter)
eller (i de sønderjydske landsdele) bd. og bl. i tingbogen, art. nr., ejerlav, sogn.
Røjle by m.m.
Strib-Røjleskov sogn.

Stempel: 25 kr. — øre

Akt: Skab B nr. 405
(udfyldes af dommerkontoret)

P.1078

Købers / Kreditors bopæl:

Gade og hus nr.: Røjlemose.

Anmelder:

08578
30 DEC. 1971

Middelfart kommunalbestyrelse
v/ Teknisk Udvalg

Vedr.: Kloakering af områder i og ved Røjlemose.

Servitut i henhold til landvæsenskommissionens kendelse af 3o juni 1969.

Den omhandlede servitut, der skal lyses forud for al pantegæld, skal have følgende ordlyd:

a) Det skal tåles, at det af landvæsenskommissionen godkendte anlæg anbringes på den pågældende ejendom, således som vist på en vedhæftet tegning.

b) Anlægget skal henligge uforstyrret, og der skal gives de til enhver tid berettigede adgang til eftersyn og rensning samt til at foretage reparations- og vedligeholdelsesarbejder i det omfang, kommunalbestyrelsen skønner det nødvendigt.

c) Uden forud indhentet tilladelse hos kommunalbestyrelsen er det forbudt på et på tegningen nærmere angivet bælte i en bredde af 2 m til hver side af et lodret plan gennem ledningernes midtlinie at bygge, foretage større træplantninger eller overhovedet iværksætte noget, der kan være til hinder for adgangen til anlægget eller for dets beståen eller til hinder eller skade for eftersyn, reparations- eller vedligeholdelsesarbejder.

d) Der må til enhver tid tåles de ulemper, der kan være forbundet med eventuelle fremtidige eftersyns- og/eller reparationsarbejder. Erstatning for eventuel herved forvoldt skade fastsættes i mangel af mindelig overenskomst af landvæsenskommissionen.

e) Med hensyn til de ejendommen påhvilende byrder og servitutter henvises til ejendommens blad i tingbogen.

f) Påtaleretten tilkommer kommunalbestyrelsen.

P.u.v.

Poul Andersen — Udvalgsformand.

Knud E. Sørensen — Stadsingeniør.

Justitsministeriets genpartpapir. Til skøder skadesløsbreve, kvitteringer til udslettelse og andre påtegninger m. m. (vedr. fast ejendom).

Bestillingsformular D

Jensen & Kjeldskov A/S, København.

INDFØRT I DAGBOGEN FOR
MIDDELFART KØBSTAD m. v.

30 DEC. 1971

LYST på matr. nr.
3g, 38a, 69a, 68a og 47a Røgle

Genpartens rigtighed bekræftes.
Dommeren i Middelfart „d. u. s."

H. P. [illegible]

Spildevandsledning

Regnvandsledning

Rids i 1:1000 vedr. matr. nrr. 3g, 38a, 69a, 68a og 47a.

Røjle by m.m.

Strib-Røjleskov sogn

Udfærdiget i februar 1971 ~~til brug~~ ved tinglysning.

Akt: Skab nr.

(udfyldes af dommerkontoret)

N

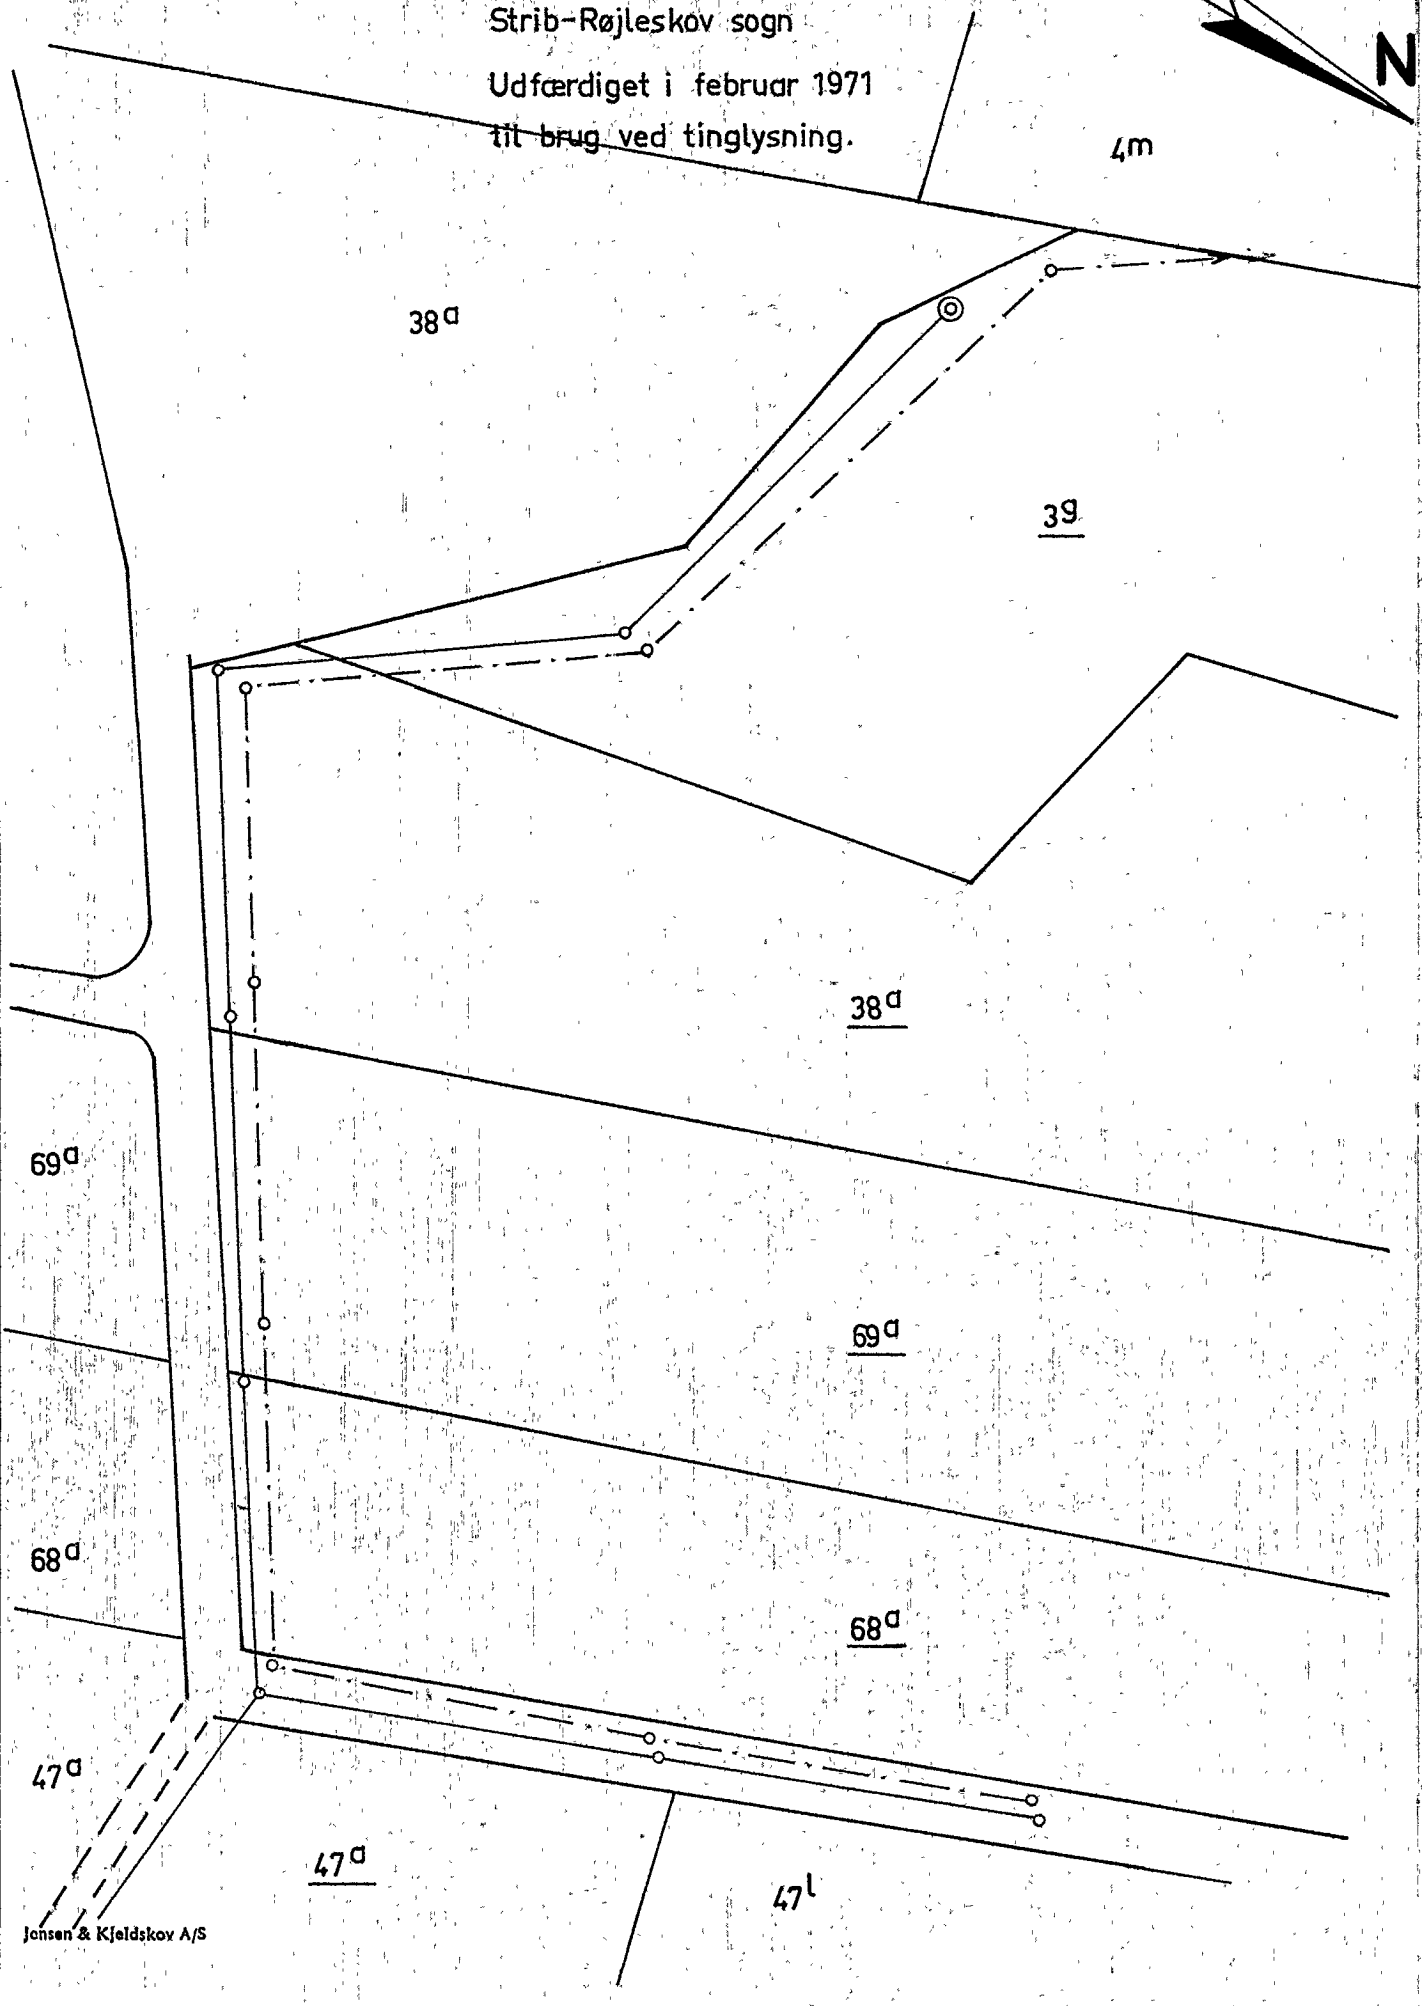

Justitsministeriets genpartskalkerlærred. Til kort.

At denne kort-genpart er nøjagtig genpart af det originale kort vedrørende ejendommen(e)

mtr. nr. _____ attesteres herved. _____ d. _____ 19 _____ Navn: _____

Bestillingsformular

Y-1 fløj

Jensen & Kjeldskov A/S

Mtr. nr., ejerlav, sogn: 57f. Stempel: 28 kr. — øre Akt: Skab P nr. 167
(i København kvarter) Røjle by m.m. (udfyldes af dommerkontoret)
eller (i de sønderjydske landsdele) bd. og bl. i tingbogen, Strib-Røjleskov sogn.
art. nr., ejerlav, sogn.

Gade og hus nr.: Røjlemose.

Købers / Kreditors bopæl:

Anmelder:

Middelfart kommunalbestyrelse.
v/Teknisk Udvalg.

30 DEC. 1971

Vedr.: Kloakering af områder i og ved Røjlemose.

Servitut i henhold til landvæsenskommissionens kendelse af 3o juni 1969.

Den omhandlede servitut, der skal lyses forud for al pantegæld, skal have følgende ordlyd:

a) Det skal tåles, at det af landvæsenskommissionen godkendte anlæg anbringes på den pågældende ejendom, således som vist på en vedhæftet tegning.

b) Anlægget skal henligge uforstyrret, og der skal gives de til enhver tid berettigede adgang til eftersyn og rensning samt til at foretage reparations- og vedligeholdelsesarbejder i det omfang, kommunalbestyrelsen skønner det nødvendigt.

c) Uden forud indhentet tilladelse hos kommunalbestyrelsen er det forbudt på et på tegningen nærmere angivet bælte i en bredde af 2 m til hver side af et lodret plan gennem ledningernes midtlinie at bygge, foretage større træplantninger eller overhovedet iværksætte noget, der kan være til hinder for adgangen til anlægget eller for dets beståen eller til hinder eller skade for eftersyn, reparations- eller vedligeholdelsesarbejder.

d) Der må til enhver tid tåles de ulemper, der kan være forbundet med eventuelle fremtidige eftersyns- og/eller reparationsarbejder. Erstatning for eventuel herved forvoldt skade fastsættes i mangel af mindelig overenskomst af landvæsenskommissionen.

e) Med hensyn til de ejendommen påhvilende byrder og servitutter henvises til ejendommens blad i tingbogen.

f) Påtaleretten tilkommer kommunalbestyrelsen.

P.u.v.

Poul Andersen — Udvalgsformand.

Knud E. Sørensen — Stadsingeniør.

Justitsministeriets genpartpapir. Til skøder skadesløsbreve, kvitteringer til udslettelse og andre påtegninger m. m. (vedr. fast ejendom).

Bestillingsformular D

Jensen & Kjeldskov A/S, København.

INDFØRT I DAGBOGEN FOR
MIDDELFART KØBSTAD m. v.

30 DEC. 1971

LYST på 57 af Røgle

Genpartens rigtighed bekræftes.
Dommeren i Middelfart „d. u. s."

J. R. Rasmussen

Akt: Skab nr.
(udfyldes af dommerkontoret)

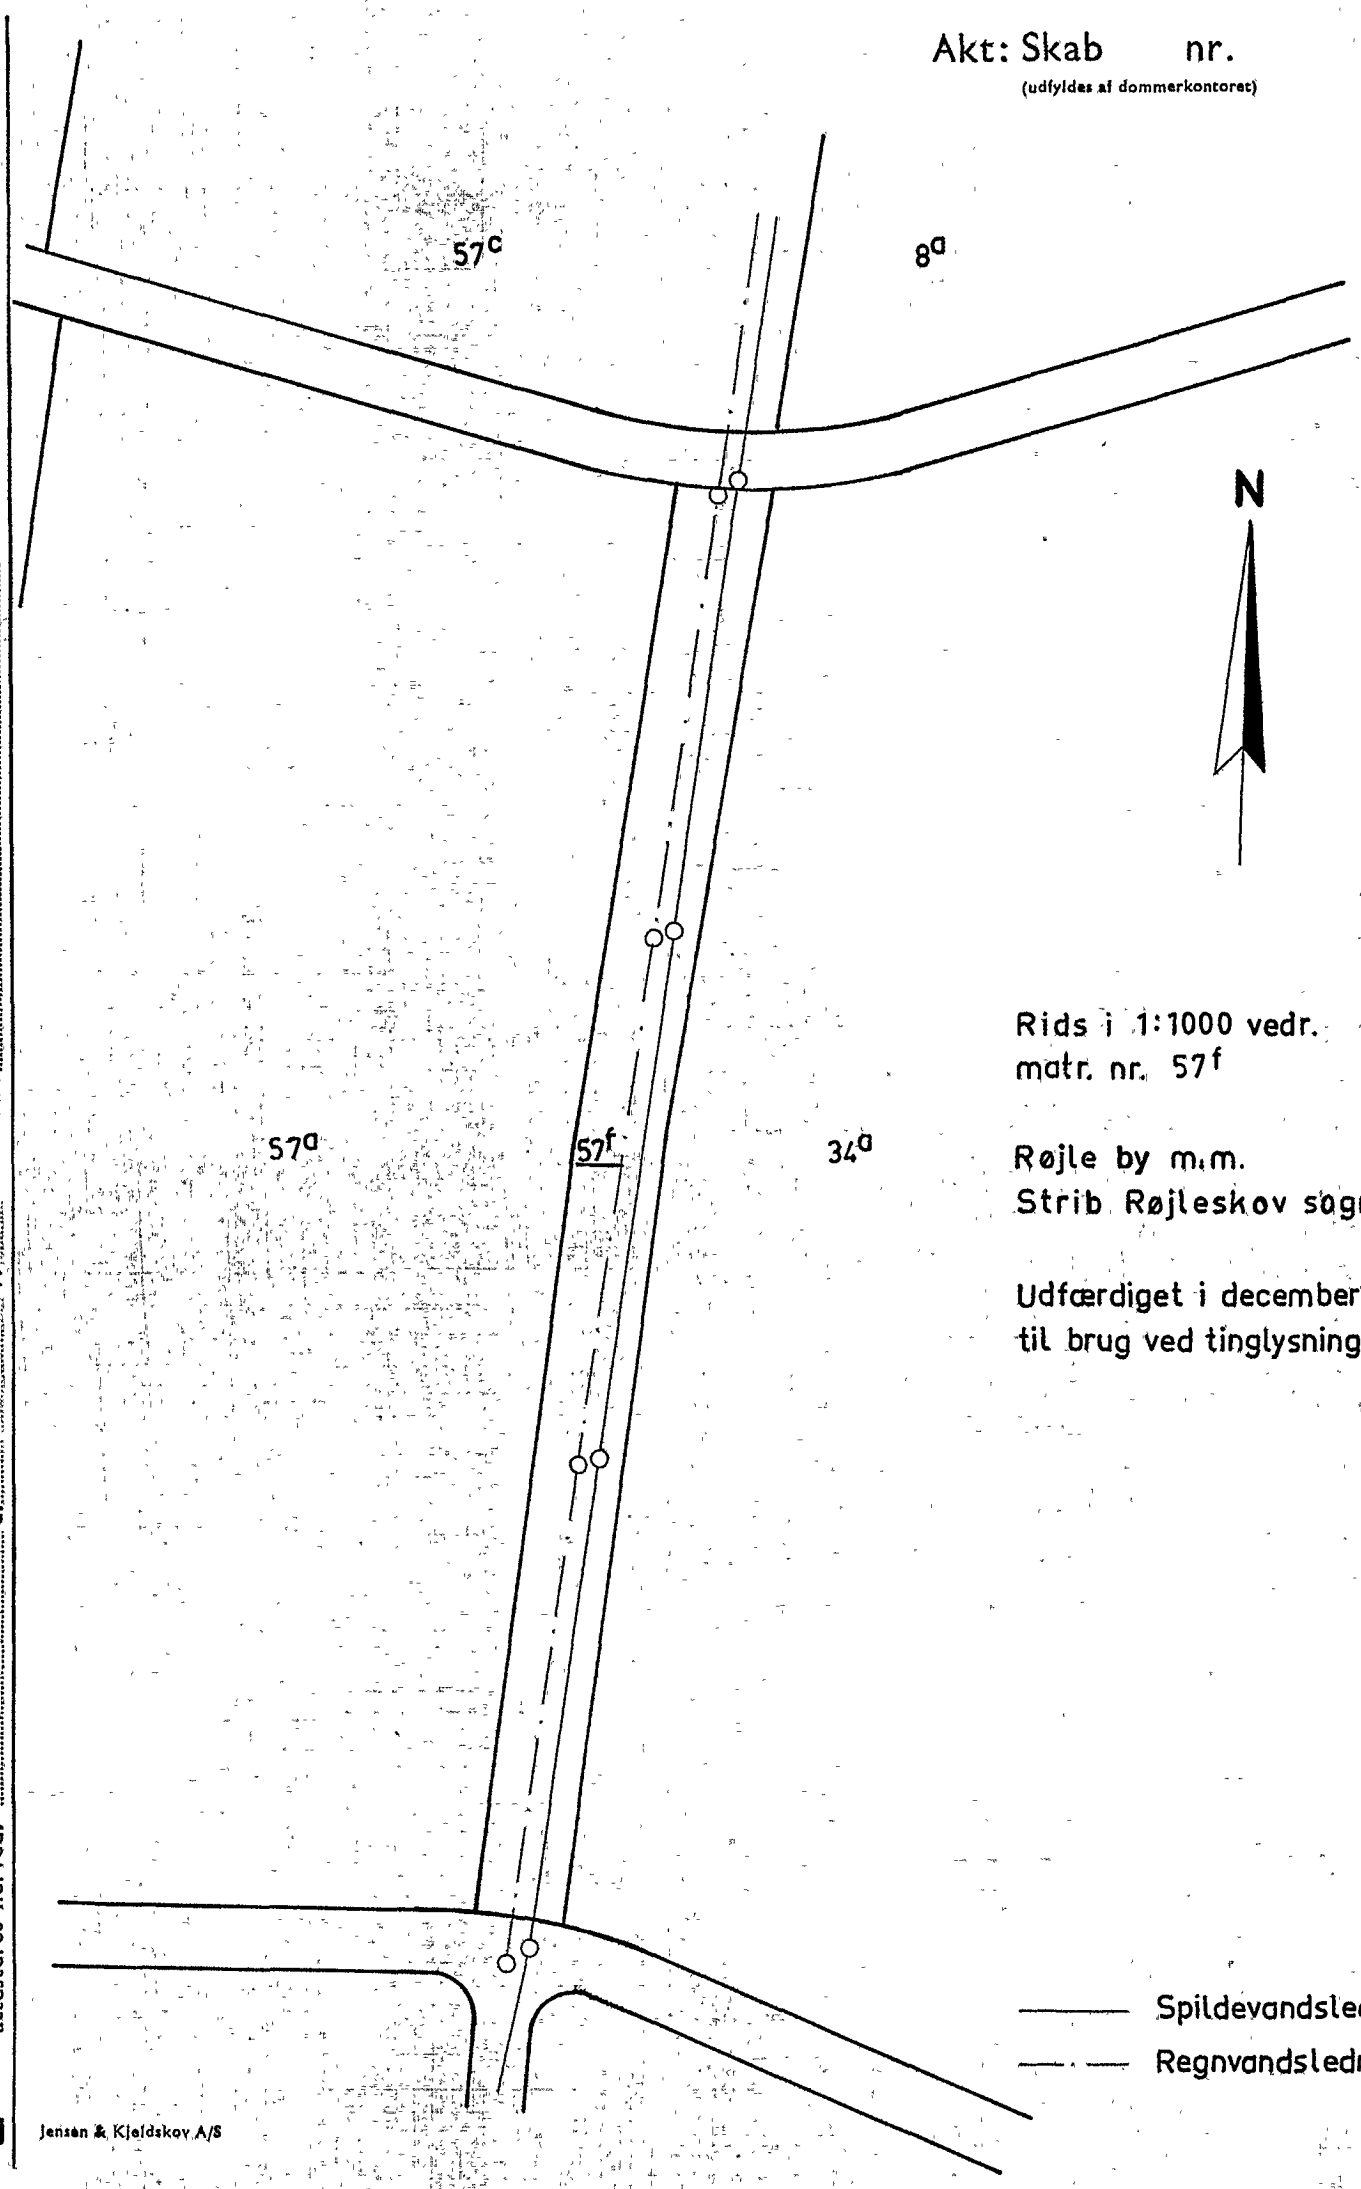

Rids i 1:1000 vedr.
matr. nr. 57f

Røjle by m.m.
Strib Røjleskov sogn

Udfærdiget i december 1971.
til brug ved tinglysning.

Justitsministeriets genpartkalkerlærred. Til kort.

At denne kort-genpart er nøjagtig genpart af det originale kort vedrørende ejendommen(e)
matr. nr. .....
attesteres herved. ..... d. ..... 19..... Navn: .....

Bestillings-formular
Y-1 (lej)

Jensen & Kjeldskov A/S

Justitsministeriets genpartpapir. Til lejekontrakter, servitutdokumenter o. l., fortsættelse af dokumenter, fortegnelse over pantsatte genstande o. l. (vedr. fast ejendom).

Mtr. nr., ejerlav, sogn: *(i København kvarter)* *eller (i de sønderjydske landsdele) bd. og bl. i tingbogen, art. nr., ejerlav, sogn.*	71n, 71m, 22o, 22n og 22f. Røjle by m.m. Strib Røjleskov Sogn,	*Stempel:* kr. øre
Gade og hus nr.: Røjlemose		*Anmelder:* Middelfart kommunalbestyrelse v/ Teknisk Udvalg

Akt: Skab B *nr.* 405 (udfyldes af dommerkontoret)

07650

-4 DEC. 1970

Vedr.: Kloakering af områder i og ved Røjlemose.

Servitut i henhold til landvæsenskommissionens kendelse af 3o juni 1969.

Den omhandlede servitut, der skal lyses forud for al pantegæld, skal have følgende ordlyd:

a) Det skal tåles, at det af landvæsenskommissionen godkendte anlæg anbringes på den pågældende ejendom, således som vist på en vedhæftet tegning.

b) Anlægget skal henligge uforstyrret, og der skal gives de til enhver tid berettigede adgang til eftersyn og rensning samt til at foretage reparations- og vedligeholdelsesarbejder i det omfang, kommunalbestyrelsen skønner det nødvendigt.

c) Uden forud indhentet tilladelse hos kommunalbestyrelsen er det forbudt på et på tegningen nærmere angivet bælte i en bredde af 2 m til hver side af et lodret plan gennem ledningernes midtlinie at bygge, foretage større træplantninger eller overhovedet iværksætte noget, der kan være til hinder for adgangen til anlægget eller for dets beståen eller til hinder eller skade for eftersyn, reparations- eller vedligeholdelsesarbejder.

d) Der må til enhver tid tåles de ulemper, der kan være forbundet med eventuelle fremtidige eftersyns- og/eller reparationsarbejder. Erstatning for eventuel herved forvoldt skade fastsættes i mangel af mindelig overenskomst af landvæsenskommissionen.

e) Med hensyn til de ejendommen påhvilende byrder og servitutter henvises til ejendommens blad i tingbogen.

f) Påtaleretten tilkommer kommunalbestyrelsen.

P.u.v.

Poul Andersen	Knud E. Sørensen
Udvalgsformand.	Stadsingeniør.

Bestillingsformular G

Jensen & Kjeldskov A/S, København

INDFØRT I DAGBOGEN FOR
MIDDELFART KØBSTAD m. v.

- 4 DEC. 1970

LYST

Anm: Samtidig hermed er lyst en tilsvarende dekl. på 22-f og 22-a i.h.t. kendelse af 19/6-1970.

Genpartens rigtighed bekræftes.
Dommeren i Middelfart „d. u. s."

Akt: Skab nr.
(udfyldes af dommerkontoret)

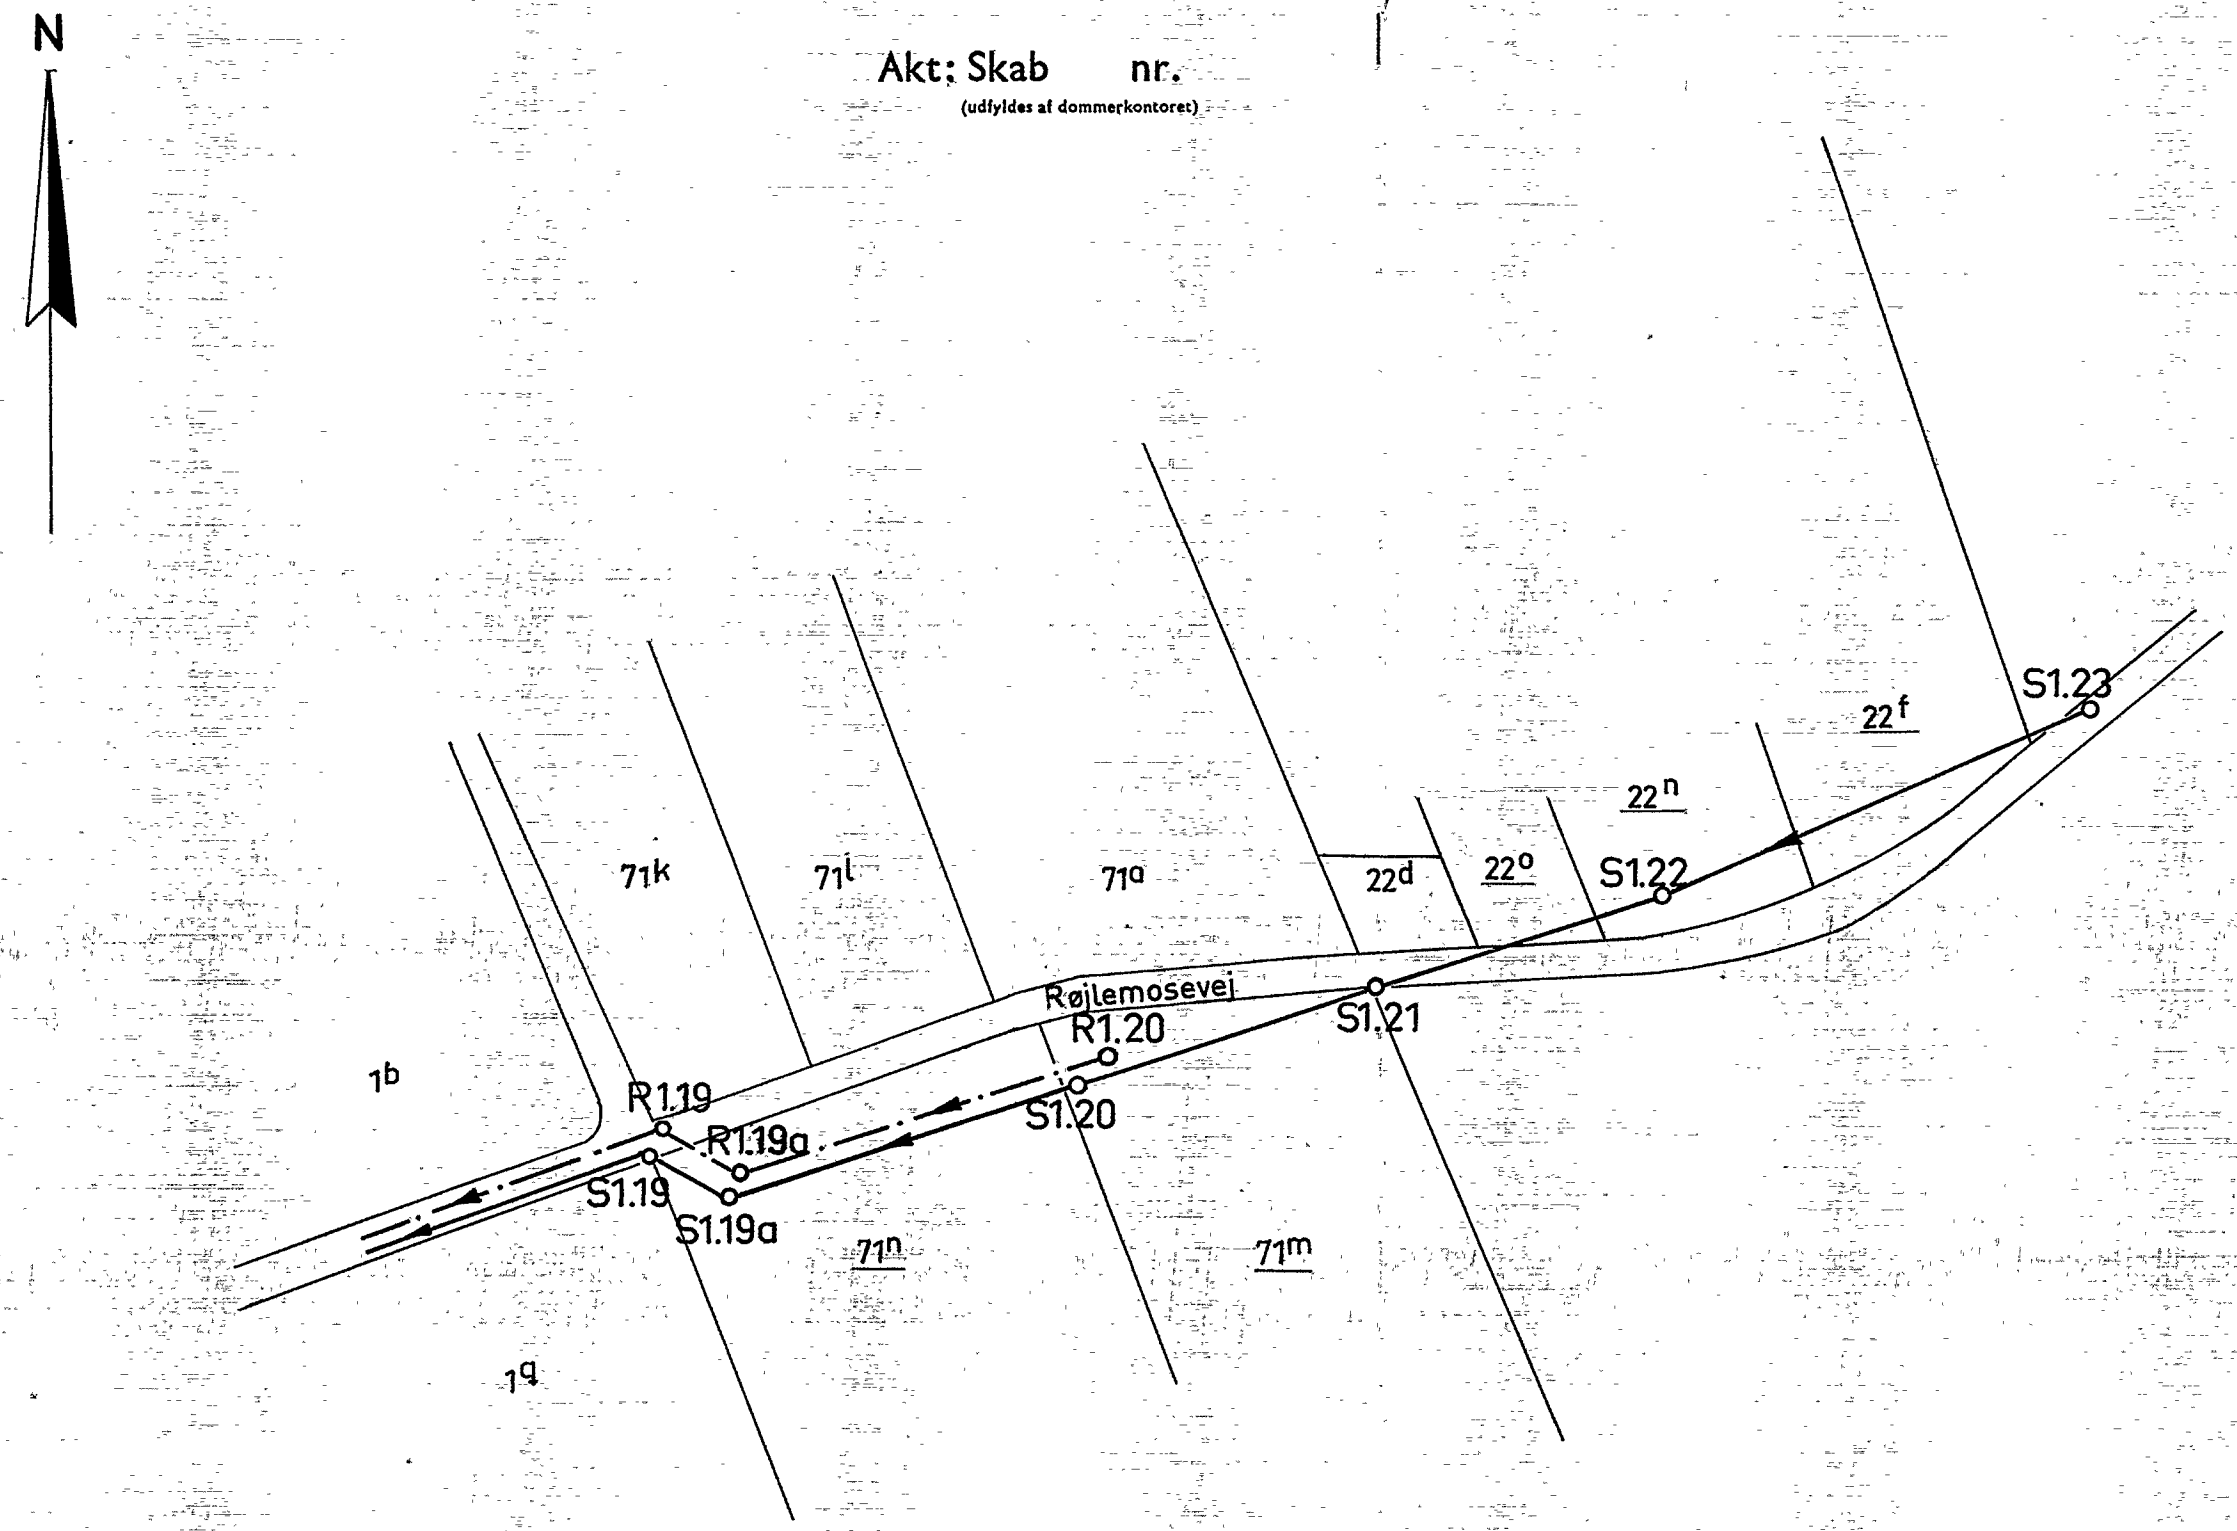

Rids i 1:1000 vedr.
matr. nrr. 71^n, 71^m, 22°, 22^n, 22^f.

Røjle by m.m.
Strib-Røjleskov sogn
Udfærdiget i oktober 1970
til brug ved tinglysning.

Spildevandsledning
Regnvandsledning

Justitsministeriets genpartskalkerlærred. Til kort.
At denne kort-genpart er nøjagtig genpart af det originale kort vedrørende ejendommen(e)
mtr. nr. ..... Navn: .....
attesteres herved. ..... d. ..... 19.
Bestillingsformular
Y-2 fløj
Jensen & Kjeldskov A/S,

Justitsministeriets genpartpapir. Til lejekontrakter, servitutdokumenter o. l., fortsættelse af dokumenter, fortegnelse over pantsatte genstande o. l. (vedr. fast ejendom).

Mtr. nr., ejerlav, sogn: *(i København kvarter)* *eller (i de sønderjydske landsdele) bd. og bl. i tingbogen, art. nr., ejerlav, sogn.*	Stempel: kr. øre	*Akt: Skab* B *nr.* 405 (udfyldes af dommerkontoret)
	22f, 22o, 22g, 22i, 22e, 7ol, 7ok, 7oi, 7oh, 7og, 7ob, 71c, 38a, 3g. Røjle by m.m. Strib Røjleskov sogn.	
Gade og hus nr.: Røjlemose		*Anmelder:* Middelfart kommunalbestyrelse v/ Teknisk Udvalg

07651
-4 DEC. 1970

Vedr.: Kloakering af områder i og ved Røjlemose.

Servitut i henhold til landvæsenskommissionens kendelse af 19 juni 197o.

Den omhandlede servitut, der skal lyses forud for at pantegæld, skal have følgende ordlyd:

a) Det skal tåles, at de af landvæsenskommissionen approberede ledninger og brønde m.v. nedlægges på den pågældende ejendom, således som vist på en vedhæftet tegning.

b) Anlægget skal henligge uforstyrret, og der skal gives de til enhver tid berettigede adgang til eftersyn og rensning samt til at foretage reparations- og vedligeholdelsesarbejder i det omfang, kommunalbestyrelsen skønner det nødvendigt.

c) Uden forud indhentet tilladelse hos kommunalbestyrelsen er det forbudt på et på tegningen nærmere angivet bælte i en bredde af 2 m til hver side af et lodret plan gennem ledningernes midtlinie at bygge, foretage større træplantninger eller overhovedet iværksætte noget, der kan være til hinder for adgangen til anlægget eller for dets beståen eller til hinder eller skade for eftersyn, reparations- eller vedligeholdelsesarbejder.

d) Der må til enhver tid tåles de ulemper, der kan være forbundet med eventuelle fremtidige eftersyns- og/eller reparationsarbejder. Erstatning for eventuel herved forvoldt skade fastsættes i mangel af mindelig overenskomst af landvæsenskommissionen.

e) Med hensyn til de ejendommen påhvilende byrder og servitutter henvises til ejendommens blad i tingbogen.

f) Påtaleretten tilkommer kommunalbestyrelsen.

P.u.v.

Poul Andersen — Knud E. Sørensen

Poul Andersen — Knud E. Sørensen

Udvalgsformand. — Stadsingeniør.

INDFØRT I DAGBOGEN FOR
MIDDELFART KØBSTAD m. v.

- 4 DEC. 1970

LYST

Anm: Samtidig hermed en lyst en tilsvarende dekl. på 22-f og 22-o i h.t. kendelse af 30/6-1969.

Genpartens rigtighed bekræftes.
Dommeren i Middelfart „d. u. s."

Akt: Skab nr.
(udfyldes af dommerkontoret)

Justitsministeriets genpartskalkerlerred. Til kort.

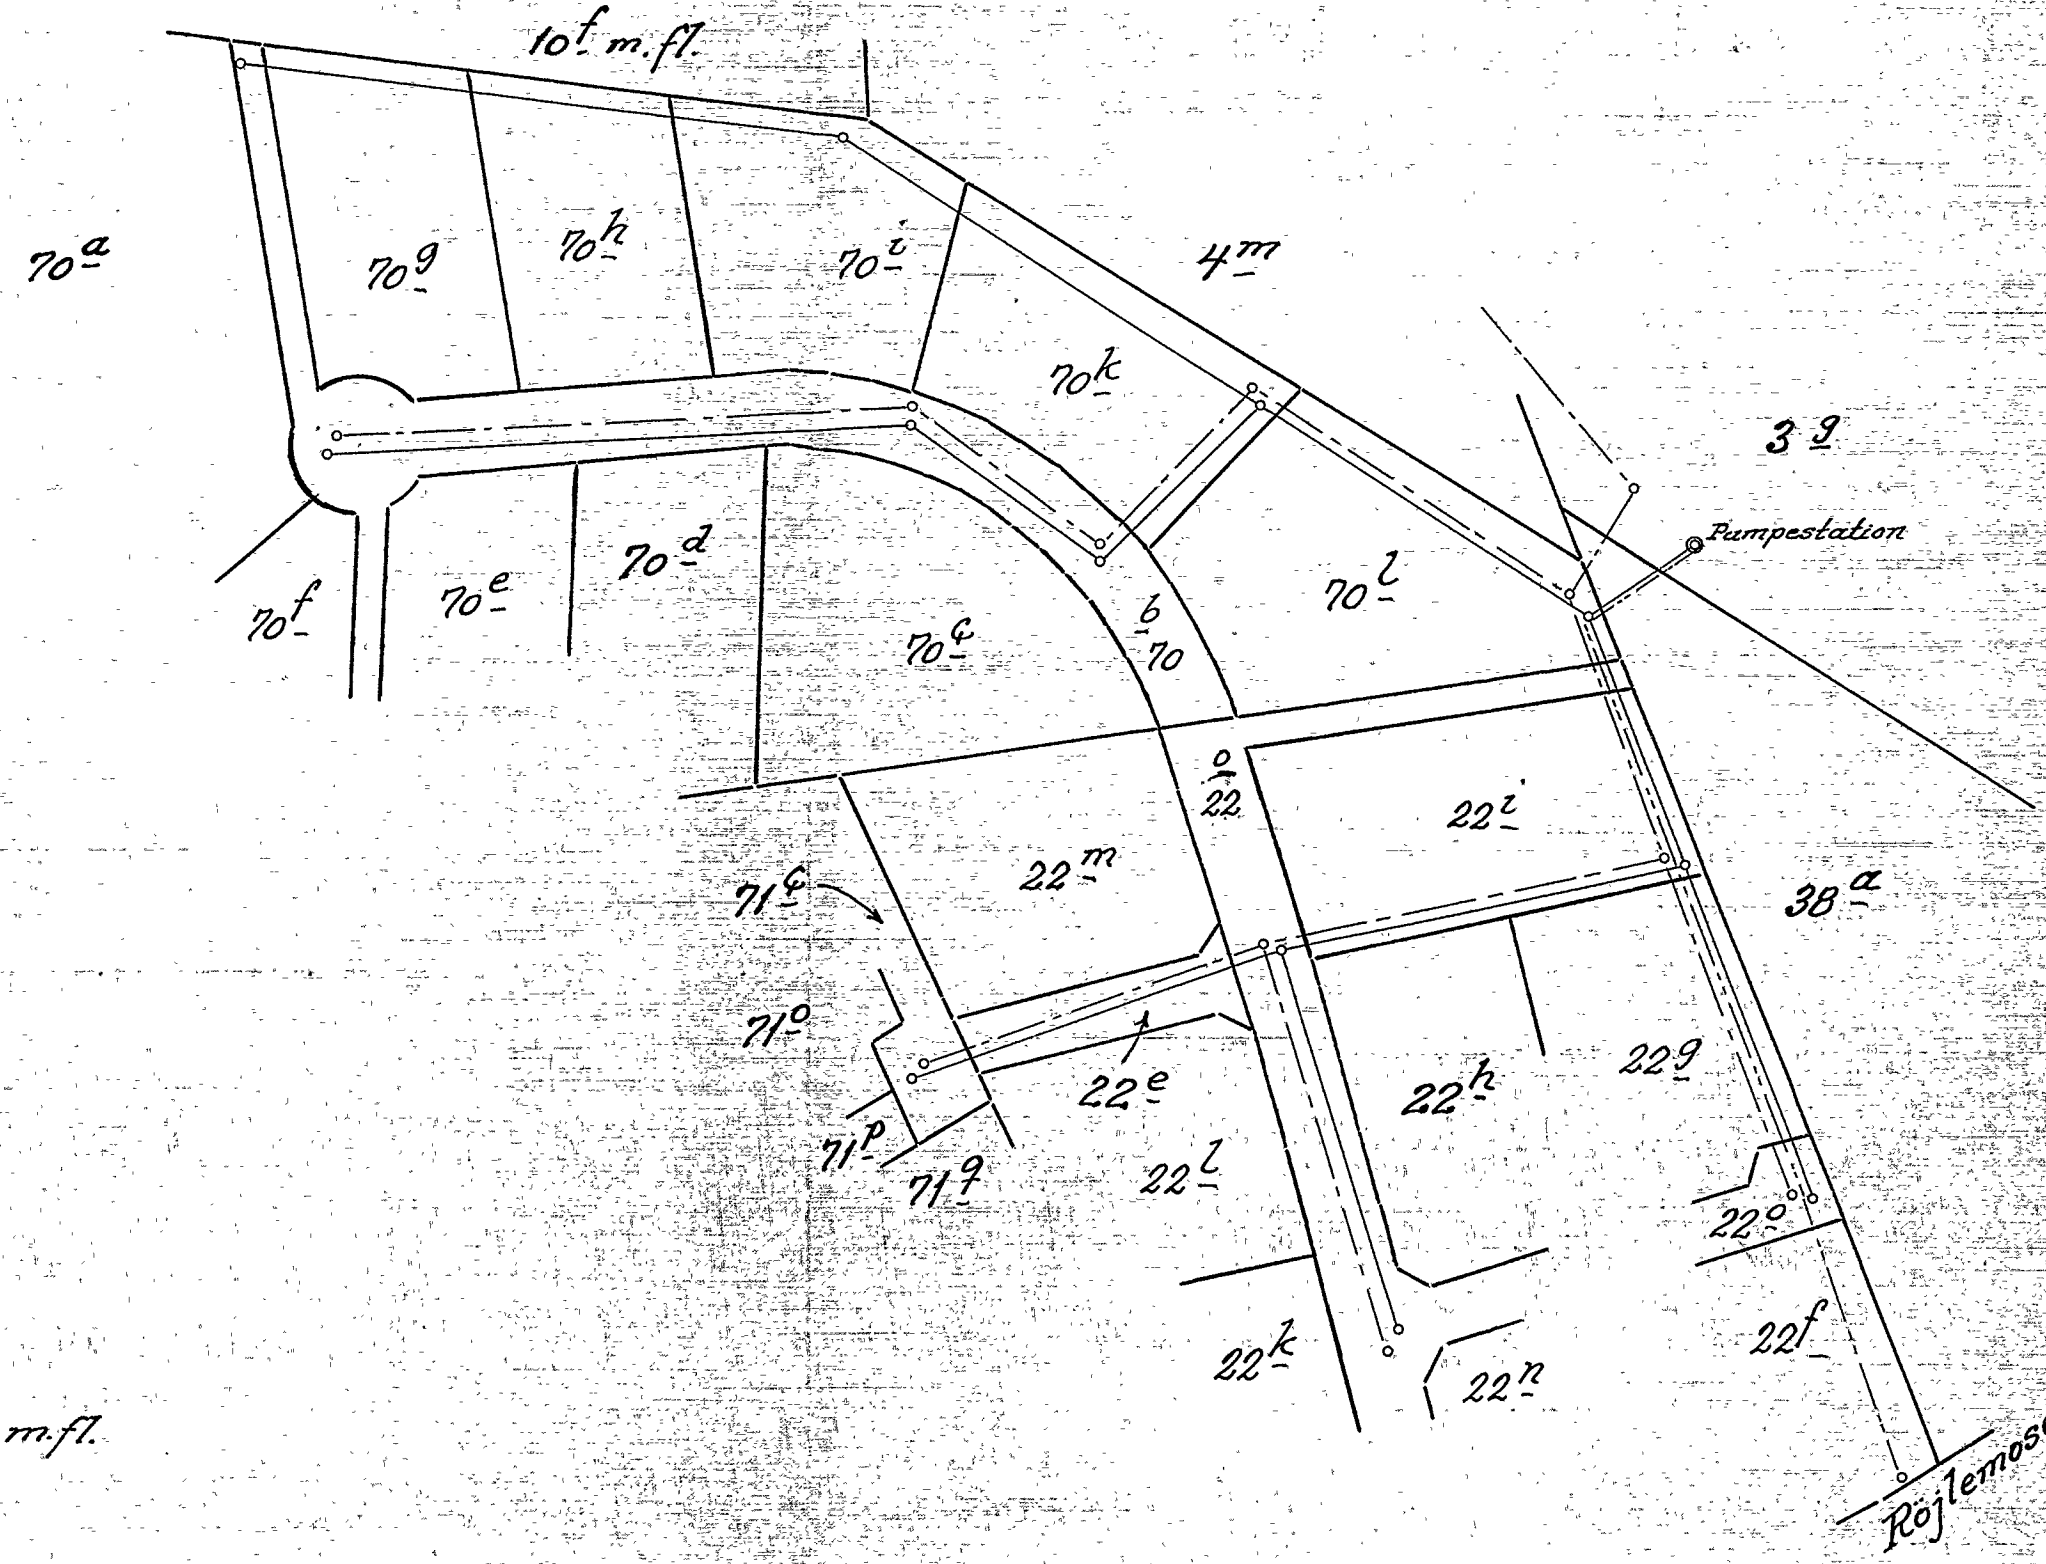

Rids i 1:1000 vedr.
matr. nr. 70a, 70b og 22a m.fl.
Röjle by m.m.
Strib-Röjleskov sogn

Udfærdiget i aug. 1970 til brug
ved tinglysning.

——————— : spildevandsledning.
— — — — — : regnvandsledning.
— · — · — · — : el-kabel og prç.-trykledning.

landinspektør

j.nr. 206/70

At denne kort-genpart er nøjagtig genpart af det originale kort vedrørende ejendommen(e)
mtr. nr. ..... d. ..... 19 ..... Navn: .....
attesteres herved.

Bestillingsformular
Y-2 fløj
Jensen & Kjeldskov A/S

Justitsministeriets genpartspapir. Til skøder skadesløsbreve, kvitteringer til udslettelse og andre påtegninger m. m. (vedr. fast ejendom).

Mtr. nr., ejerlav, sogn: (i København kvarter) eller (i de sønderjydske landsdele) bd. og bl. i tingbogen, art. nr., ejerlav, sogn.

6^{v} og 45^{d} Røjle By m.m. Strib-Røjleskov Sogn.

Stempel: 4 kr. — øre

Akt: Skab P nr. 167 (udfyldes af dommerkontoret)

Gade og hus nr.:

Købers / Kreditors } bopæl:

Anmelder:

Møller Christensen & Lehmann Madsen landinspektører Middelfart

05732

-1 OKT. 1965

Deklaration

Undertegnede Vejlby-Strib kommune, som ejer af matr.nr. 6^{v} Røjle By m.m., Strib-Røjleskov Sogn og undertegnede Marius C.Christiansen som ejer af matr.nr. 45^{d} smst., pålægger herved nævnte ejendomme oversigtsservitut således:

De til enhver tid værende ejere af matr.nr. 6^{v} og 45^{d} Røjle By m.m., Strib-Røjleskov Sogn er pligtig at drage omsorg for, at der på de på vedlagte rids med skravering angivne og i forhold til skel målsatte oversigtsarealer hverken varigt eller midlertidigt forefindes noget af større højde end 1 m over en flade gennem de tilstødende vejes midtlinier.Denne bestemmelse omfatter ikke sne.

Påtaleberettiget er Assens amtsråd ved amtsvejvæsenet.

Foranstående begæres tinglyst som servitut på ovennævnte matr.nr. 6^{v} og 45^{d} Røjle By m.m., Strib-Røjleskov Sogn, idet der med hensyn til de ejendommene nu påhvilende servitutter og andre byrder henvises til tingbogen.

Dato: 30.sept.1965 Som ejer af matr.nr. 6^{v}: Vejlby-Strib kommune sign. Aage Warming

Dato: 30.sept.1965 Som ejer af matr.nr.45^{d}: sign.M.Christiansen

Indført i dagbogen for retskreds nr. 43: Middelfart købstad m.v., den -1 OKT. 1965
Akt: skab P nr. 167
Lyst tingbog

Skab I

Landinspektørfirmaet Møller Christensen & Lehmann Middelfart A.S.

Bestillingsformular D

Jensen & Kjeldskov A/S, København

Akt: Skab P nr. 169 3
(udfyldes af dommerkontoret)

Justitsministeriets genpartkalkerlærred. Til kort.

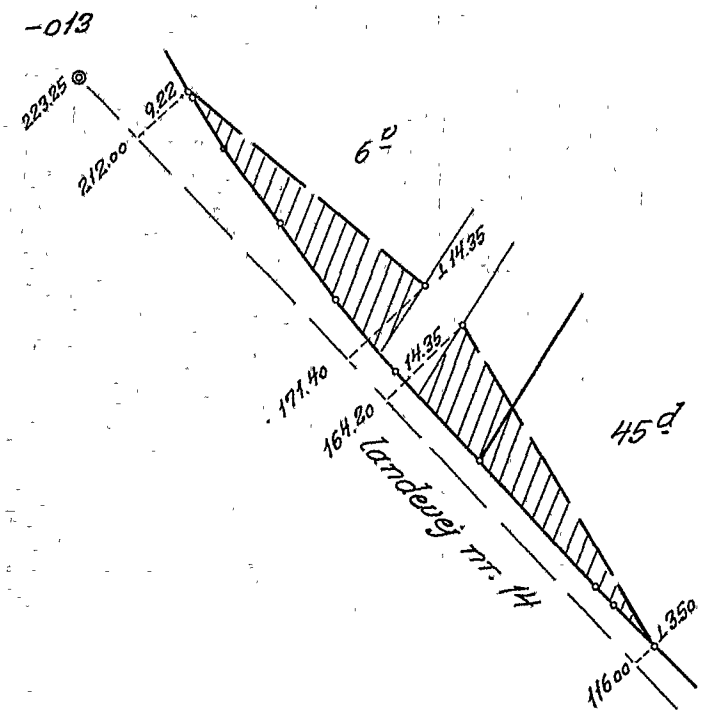

40-17-012

Terræn af
Röjle by m.m.
Strib-Röjleskov sogn
Udfærdiget i sept. 1965 til brug ved tinglysning.

Landinspektör

At denne kort-genpart er nøjagtig genpart af det originale kort vedrørende ejendommen(e)
mtr. nr. ..... d. ..... 19 ..... Navn: .....
attesteres herved.

Bestillings-formular
Y-1 fløj
Jensen & Kjeldskov A/S

1:1000

2814
18/3 1932.

P. 107 B-405 Akt: Skab E Nr. 498x
(Udfyldes af Dommerkontoret) D-490 D-501

Justitsministeriets Genpartpapir. Til Skøder, Skadesløsbreve, Kvitteringer til Udslettelse og andre Paategninger m. m. (vedr. fast Ejendom).

Mtr. Nr., Ejerlav, Sogn: (i København Kvarter) eller (i de sønderjydske Landsdele) Bd. og Bl. i Tingbogen, Art. Nr., Ejerlav, Sogn. 22a. 24. 47a. 68. 69 Røjle, Taarup og Bøgelund Byer, Vejlby Sogn

Købers / Kreditors Bopæl: Brøndeskov pr. Skive.

Anmelderens Navn og Bopæl (Kontor): Politiassistent Sørensen. Skive.

Gade og Hus Nr.: (hvor saadant findes)

Stempel: 2 Kr. Øre.

Declaration.

Mellem undertegnede;

Gaardejer Niels Hansen Nielsen, Røjle Mose,

Ejer af Matr. Nr. 69 af Røjle, Taarup og Bøgelund Byer, Vejlby Sogn,

Gaardejer Anders Troelsen, Røjle Mose,

som Ejer af Matr. Nr. 68 og 47a sammesteds,

Gaardejerske Abelone Kathrine Nielsen, Brøndeskov,

som Ejer af Matr. Nr. 22a sammesteds,

Gaardejerske Niels Larsens Enke, "Sølyst", Røjle Skov,

som Ejer af Matr. Nr. 24 sammesteds,

indgaaes herved følgende Overenskomst vedrørende en

V E J,

løbende fra omtrentlig Midten af Matr. Nr. 69 over Matr. Nr. 68, 47a, 22a til Matr. Nr. 24 ;

Vejen skal løbe - som paa nedenstaaende Skitse vist - langs de sydlige Skel af de nævnte Ejendomme.

R.R.855,476,592,440,507.

Bestillings-Formular D

Jensen & Kjeldskov, A/S, København

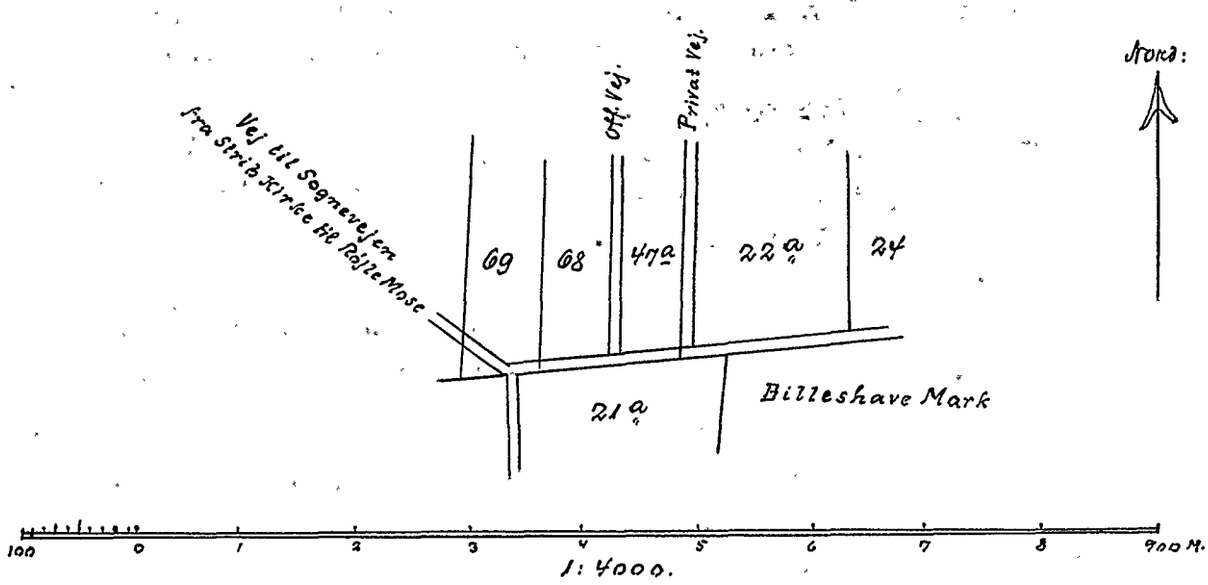

Vejen skal have en Bredde af 6 - sex - Alen i sin hele Længde.

Den skal være til udelukkende Brug for og Afbenyttelse af os og efterfølgende Ejere af vore ovennævnte Ejendomme.-

Vejen vedligeholdes af Ejerne af Matr. Nr. 22a og 24 i Forening, og disse skulle have Pantaleretten med Hensyn til Vejen.-

For Vejens Udlægning betales intet Vederlag af nogen af Parterne.

Nærværende Declaration ønskes tinglyst som Hæftelse paa vore fornævnte Ejendomme, idet vi angaaende Behæftelser paa disse henvise til Ejendommenes Folier i Thingbøgerne.-

Til Bekræftelse med vore vidnefaste Underskrifter.

Røjle Mose, Brændeskov og Røjle Skov, den 14' Marts 1932.-

Niels Hansen Nielsen,	Anders Troelsen.
Som Hustru:	Som Hustru:
Andrea Nielsen.	Vilhelmine K. Troelsen.
Katrine Nielsen.	Johanne Larsen.

Til Vitterlighed om Underskrifternes Ægthed, Dateringens Rigtighed samt om Underskrivernes Fuldmyndighed:

J. Sørensen. E. Sørensen.

Politiassistent og Hustru.

Indført i Dagbogen for Retskreds Nr. 43, Middelfart Kobstad m. v., Strib.
Frodag 18'Marts 1932.

Genpartens Rigtighed bekræftes.
Dommeren i Middelfart m. v., den 28/7 1932

Lyst. Tinglæser Ed. Vejlby Bl. 507 D 490
/Karl Andersen Fm.

Mtr. nr., ejerlav, sogn: (i København kvarter) eller (i de sønderjydske landsdele) bd. og bl. i tingbogen, art. nr., ejerlav, sogn.

22a Røjle by m.m., Strib-Røjleskov sogn

Stempel: kr.

Akt: Skab B nr. 405 (udfyldes af dommerkontoret)

Købers / Kreditors bopæl:

Gade og hus nr.:

Anmelder:

J.nr. 77-6105-2

Servituterklæring

I anledning af en påtænkt skelforandring mellem matr.nr. 22a og 8ao Røjle by m.m., Strib-Røjleskov sogn, hvorved overføres:

"XX" 263 m2 fra matr.nr. 22a til matr.nr. 8ao

erklærer undertegnede herved, at skelforandringen ikke ændrer de bestående servitutforhold.

Middelfart, den 11. APR. 1978

landinspektør

Justitsministeriets genpartpapir. Til skøder skadesløsbreve, kvitteringer til udslettelse og andre påtegninger m.m. (vedr. fast ejendom).

Bestillings-formular D

Jensen & Kjeldskov A/S, København

Mtr. nr., ejerlav, sogn: (i København kvarter) eller (i de sønderjydske landsdele) bd. og bl. i tingbogen, art. nr., ejerlav, sogn.

22^z Røjle by, Strib-Røjleskov sogn.

Stempel: kr.

Akt: Skab B nr. 405 (udfyldes af dommerkontoret)

Købers / Kreditors bopæl:

Gade og hus nr.:

Anmelder:

J.nr. 77-6003-2

Servituterklæring.

for matr.nr. 22^z Røjle by, Strib-Røjleskov sogn, der ved landbrugsministeriets skrivelse af 21.11.1978 er fraskilt matr.nr. 22^a smst.

L. 18. 3.1932 Dokument angående fælles vej mellem ejerne af matr.nr. 22^a, 24; 47^a, 68 og 69.
Vedrører ikke matr.nr. 22^z.

L. 29. 5.1970 Deklaration angående hegn, bebyggelse, godkendelse af bygningstegninger, forbud mod at drive handel, industri m.m. eller oplagsplads, forbud mod husdyrhold, dog ikke stuedyr, forbud mod at drive virksomhed til gene for omboende m.v.
Vedrører hverken matr.nr. 22^a eller matr.nr. 22^z.

L. 22. 6.1973 Partiel byplanvedtægt nr. 8.
Vedrører matr.nr. 22^z, vedrører herefter ikke matr.nr. 22^a.

L. 23. 4.1974 Tillæg nr. 1 til partiel byplanvedtægt nr. 8.
Vedrører matr.nr. 22^z, vedrører herefter ikke matr.nr. 22^a.

L. 3. 7.1974 Deklaration angående anbringelse af kabler i tracé.
Vedrører ikke matr.nr. 22^z.

L. 20. 3.1978 Deklaration angående oversigtsarealer.
Vedrører matr.nr. 22^z, vedrører herefter ikke matr.nr. 22^a.

Middelfart, den 1978-11-27

landinspektør

Justitsministeriets genpartpapir. Til skøder skadesløsbreve, kvitteringer til udslettelse og andre påtegninger m.m. (vedr. fast ejendom).

Bestillingsformular D

Jensen & Kjeldskov A/S, København

Mtr. nr., ejerlav, sogn: (i København kvarter) eller (i de sønderjydske landsdele) bd. og bl. i tingbogen, art. nr., ejerlav, sogn.

22^{z} m.fl.

Røjle by m.m.,

Strib-Røjleskov sogn.

Gade og hus nr.:

Stempel: kr.

Akt: Skab B nr. 405
(udfyldes af dommerkontoret)

Købers / Kreditors bopæl:

Anmelder:
JOHAN LADEGAARD
LANDSRETSSAGFØRER
ALBANIGADE 44 - 5000 ODENSE C
TLF. (09) 12 43 44 . GIRO 2 02 34 82

J.nr.77-6105-2

Servituterklæring.

for matr.nr. 22^{ae},22^{af},22^{ag},22^{ah},22^{ai},22^{ak},22^{al},22^{am},22^{an},22^{ao},22^{ap},22^{aq},22^{ar},
22as,22^{at},22^{au},22^{av},22^{ax},22^{ay},22^{az},$22^{aæ}$,$22^{aø}$,22^{ba},22^{bb},22^{bc},22^{bd},22^{be},22^{bf},22^{bg},
22^{bh},22^{bi},22^{bk},22^{bl},22^{bm},22^{bn},22^{bo},22^{bp},22^{bq},22^{br},22^{bs},22^{bt},22^{bu},22^{bv},22^{bx},22^{by},
22^{bz},$22^{bæ}$,$22^{bø}$,22^{ca},22^{cb},22^{cc},22^{cd},22^{ce},22^{cf},22^{cg},22^{ch},og 22^{ci} Røjle by m.m.,
Strib-Røjleskov sogn,der ved landbrugsministeriets skrivelse af 5.12.1978 er fraskilt matr.nr. 22^{z} smst.

L.22.6.1973 partiel byplanvedtægt nr. 8. (K462)
(5874) Vedrører de nye matr.nre.

L.23.4.1974 tillæg nr. 1 til partiel byplanvedtægt nr. 8. (D449)
(3010) Vedrører de nye matr.nre.

L.20.3.1978 dekl.ang. nærmere bestemte oversigtsarealer m.v. (B.405)
(3574) Vedrører matr.nr.22^{ay},22^{be},22^{bf},$22^{bø}$,22^{ch} og 22^{ci}.
Vedrører ikke de øvrige nye matr.nre.
Vedrører herefter ikke matr.nr. 22^{z}.

Middelfart,den 11.12.1978

landinspektør

Justitsministeriets genpartpapir Til skader skadesløsbreve, kvitteringer til udslettelse og andre påtegninger m.m. (vedr. fast ejendom)

Bestillingsformular D

Jensen & Kjeldskov, Diaprint A/S 01-140887

Mtr. nr., ejerlav, sogn: $6^y, 6^z, 6^{æ}$ Stempel: kr.
(i København kvarter)
eller (i de sønderjydske landsdele) bd. og bl. i tingbogen,
art. nr., ejerlav, sogn.
Røjle by m.m.
Strib-Røjleskov
sogn.

Akt: Skab P nr. 167.
(udfyldes af dommerkontoret)

Købers / Kreditors } bopæl:

Gade og hus nr.:

Anmelder:

J.nr. 185/71

Servituterklæring.

for matr.nr. $6^y, 6^z$ og $6^{æ}$, Røjle by m.m., Strib-Røjleskov sogn, der ved landbrugsministeriets skrivelse af 10.4.1972 er fraskilt matr. nr. 6^v smst.

L.28. 9.1932	dokm.ang. bygningsafstand fra landevej.	Vedr. ikke de nye matr.nre.
L.10. 9.1952	dokm.ang. el-master.	Vedr.matr.nr. 6^v og 6^y. Vedr. ikke matr.nr. 6^z og $6^{æ}$.
L.23.11.1954	endelig jordfordelingskendelse.	Vedr.de nye matr.nre.
L. 9. 2.1957	dokm.ang. bygningsafstand fra bivej.	Vedr.de nye matr.nre.
L.14.11.1958	Dokm.ang. el-master	Vedr.ikke de nye matr.nre.
L.10.10.1964	Overenskomst ang. rørledning.	Vedr. de nye matr.nre.
L. 1.10.1965	dekl.ang. oversigtsservitut.	Vedr.ikke de nye matr.nre.
L.30.12.1971	dekl.ang. kloakering af områder i og ved Røjlemose i h,t. landvæsensnævnskendelse af 30/6-1969,	Vedr.ikke de nye matr.nre.

Middelfart, den 12. april 1972

landinspektør.

Justitsministeriets genpartpapir. Til skøder skadesløsbreve, kvitteringer til udslettelse og andre påtegninger m. m. (vedr. fast ejendom).

Bestillingsformular D

Jensen & Kjeldskov A/S, København

Mtr. nr., ejerlav, sogn: (i København kvarter) eller (i de sønderjydske landsdele) bd. og bl. i tingbogen, art. nr., ejerlav, sogn. 6^{aa} Røjle by Strib-Røjleskov sogn

Stempel: kr. øre

Akt: Skab X nr. 584 (udfyldes af dommerkontoret) P 167.

Købers / Kreditors } bopæl:

Gade og hus nr.:

Anmelder:

Justitsministeriets genpartpapir. Til skøder skadesløsbreve, kvitteringer til udslettelse og andre påtegninger m. m. (vedr. fast ejendom).

J.nr. M.197/73

Servituterklæring

for matr.nr. 6^{aa}, Røjle by, Strib-Røjleskov sogn, der ved landbrugsministeriets skrivelse af 3.12.1973 er fraskilt matr.nr. 6^{v} smst.

L.28. 9.1932	dok.ang. bygningsafstand fra landevej.	Vedr. matr.nr. 6^{aa}.
L.10. 9.1952	dok.ang. elmaster.	Vedr. ikke matr.nr. 6^{aa}.
L.23.11.1954	endelig jordfordelingskendelse	Vedr. ikke matr.nr. 6^{aa}.
L. 9. 2.1957 (489)	dok.ang. bygningsafstand fra bivej.	Vedr. ikke matr.nr. 6^{aa}.
L. 9. 2.1957 (490)	dok.ang. do.	Vedr. ikke matr.nr. 6^{aa}.
L.14.11.1958	dok.ang. elmaster.	Vedr. ikke matr.nr. 6^{aa}.
L.10.10.1964	overenskomst ang. rørledning.	Vedr. matr.nr. 6^{aa}.
L. 1.10.1965	dekl.ang. oversigtsservitut.	Vedr. ikke matr.nr. 6^{aa}.
L.30.12.1971	dekl.ang. kloakering af områder i og ved Røjlemose i h.t. landvæsensnævnskendelse af 30.6.1969.	Vedr. matr.nr. 6^{aa}.
L.22. 6.1973	Partiel byplanvedtægt nr. 8	Vedr. matr.nr. 6^{aa}.
L.24. 7.1973	dekl.om at pc. 2 af 6^{v} alene har adgang til landevej 614 ad en overkørsel til brug for regnvandsbassin og ang. opsættelse og vedligeholdelse af fast ubrudt hegn i skellet mellem pc. 2 og landevejen.	Vedr. matr.nr. 6^{aa}. Vedr. herefter ikke matr.nr. 6^{v}.

Middelfart, den 10. DEC. 1973

landinspektør.

Bestillingsformular C

Jensen & Kjeldskov A/S, København

Mtr. nr., ejerlav, sogn: 6^{v} og 57^{f} Stempel: kr. øre Akt: Skab P nr. 167
(udfyldes af dommerkontoret)
(I København kvarter) Røjle m.fl. Byer,
eller (i de sønderjydske landsdele) bd. og bl. i tingbogen, Strib-Røjleskov Sogn.
art. nr., ejerlav, sogn.
Købers / Kreditors bopæl:
Gade og hus nr.: Tinglyst på tinglysningskontoret for retskreds nr. 43, Middelfart købstad m. v., den 10/1 1964 ad nr. 205 1964.
Anmelder:

Justitsministeriets genpartpapir. Til skader skadesløsbrøve, kvitteringer til udslettelse og andre påtegninger m. m. (vedr. fast ejendom).

Servituterklæring

for matr.nr. 6^{v} Røjle m.fl. Byer, Strib-Røjleskov Sogn, der ved landbrugsministeriets skrivelse af 14. november 1963 er fraskilt matr.nr. 6^{p} smst.

L. 28/9 1932	Dokm.ang. bygningsafstand fra landevej.	Vedrører matr.nr. 6^{v}.
L. 10/9 1952	Dokm.ang. el- master m,v., ikke til hinder for pant.	Vedrører matr.nr. 6^{v}.
L. 23/11 1954	Endelig jordfordelingskendelse.	Vedrører matr.nr. 6^{v}.
L. 9/2 1957	Dokm.ang. bygningsafstand fra bivej. (vedr. 6^{p}, 9^{v} og 57^{a})	Vedrører matr.nr. 6^{v}.
L. 14/11 1958	Dokm.ang. el- master m.v. på 6^{v}, 21^{c} og 57^{a}.	Vedrører matr.nr. 6^{v}.

og for matr.nr. 57^{f} smst., der ved landbrugsministeriets ovennævnte skrivelse er fraskilt matr.nr. 57^{a} smst.

L. 23/11 1954	Endelig jordfordelingskendelse.	Vedrører matr.nr. 57^{f}.
L. 9/2 1957	Dokm.ang. bygningsafstand fra bivej. (vedr. 6^{p}, 9^{v} og 57^{a})	Vedrører matr.nr. 57^{f}.
L. 9/2 1957	Dokm.ang. bygningsafstand fra bivej. (vedr. 57^{a})	Vedrører matr.nr. 57^{f}.
L. 14/11 1958	Dokm.ang. el- master m.v. på 6^{v}, 21^{c} og 57^{a}.	Vedrører matr.nr. 57^{f}.

Middelfart, den 19. november 1963

landinspektør

Bestillingsformular D

Jensen & Kjeldskov A/S, København